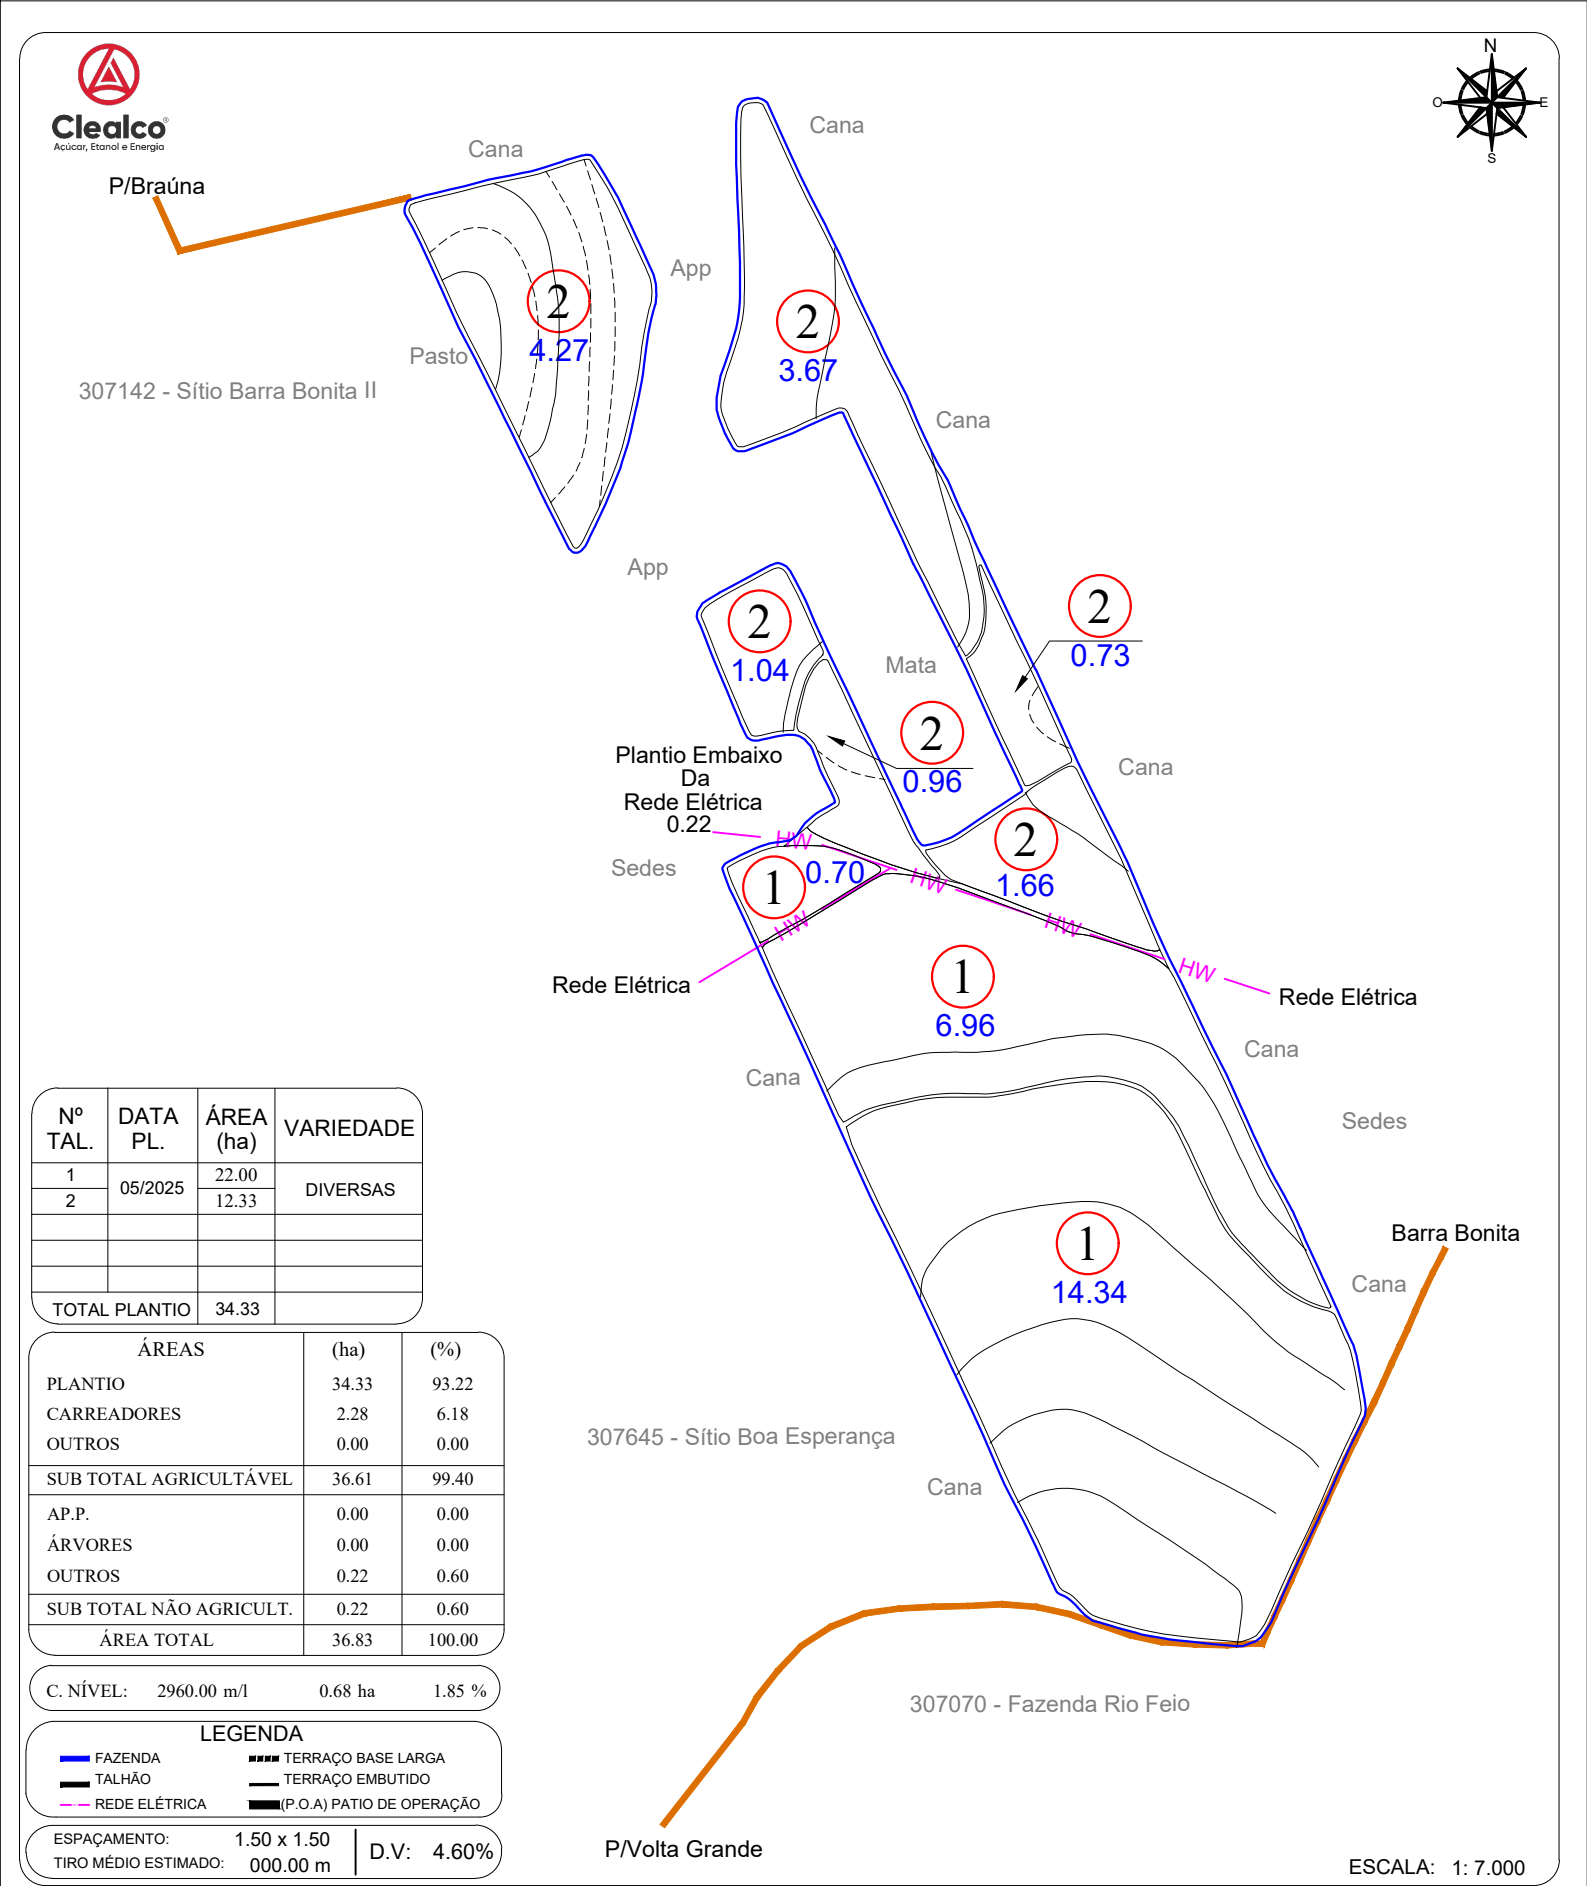


Nº TAL.	DATA PL.	ÁREA (ha)	VARIEDADE
1	05/2025	22.00	DIVERSAS
2		12.33	
TOTAL PLANTIO		34.33	

ÁREAS	(ha)	(%)
PLANTIO	34.33	93.22
CARREADORES	2.28	6.18
OUTROS	0.00	0.00
SUB TOTAL AGRICULTÁVEL	36.61	99.40
AP.P.	0.00	0.00
ÁRVORES	0.00	0.00
OUTROS	0.22	0.60
SUB TOTAL NÃO AGRICULT.	0.22	0.60
ÁREA TOTAL	36.83	100.00


C. NÍVEL: 2960.00 m/l 0.68 ha 1.85 %

LEGENDA

- FAZENDA
- TALHÃO
- REDE ELÉTRICA
- TERRAÇO BASE LARGA
- TERRAÇO EMBUTIDO
- (P.O.A) PATIO DE OPERAÇÃO

ESPAÇAMENTO: 1.50 x 1.50
TIRO MÉDIO ESTIMADO: 000.00 m
D.V: 4.60%

CROQUI DE ACESSO

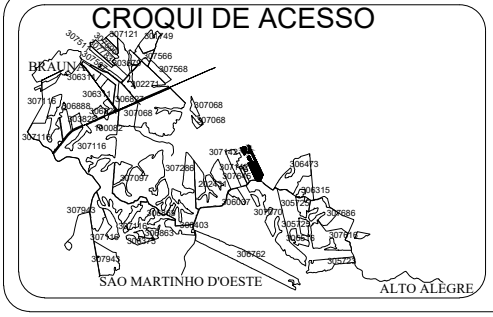

SÍTIO KURAMOTO

PROPRIETÁRIO: PAULO CÉSAR LOPES
COMPRADOR: CLEALCO
MUNICÍPIO: PENÁPOLIS- SP

DISTÂNCIAS (km):
UNID. I - Asfalto: 26.50 Terra.: 6.50
UNID.I I - Asfalto: 38.00 Terra.: 5.70

COORDENADAS: E(X): 577963.18 N(Y): 7618296.94
LAT: -21°32'11.0608" LONG: -50°14'49.6816"

CLEALCO - AÇÚCAR E ALCOOL S/A - DEPARTAMENTO DE GEOTECNOLOGIA

LEVANTAMENTO VIA:
- SATÉLITE
- GPS / VANT
- GOOGLE

UNIDADE: I
PARTE: A/A
FUNDO AGRÍCOLA: 306355

M:\01-Mapa de safra\Mapas Atualizados\Terceiro\306355 - Sítio Kuramoto I (Paulo Cesar Lopes)\306355 - Sitio Kuramoto I (Paulo Cesar Lopes).dwg

Bruno Gamboa 27/01/26