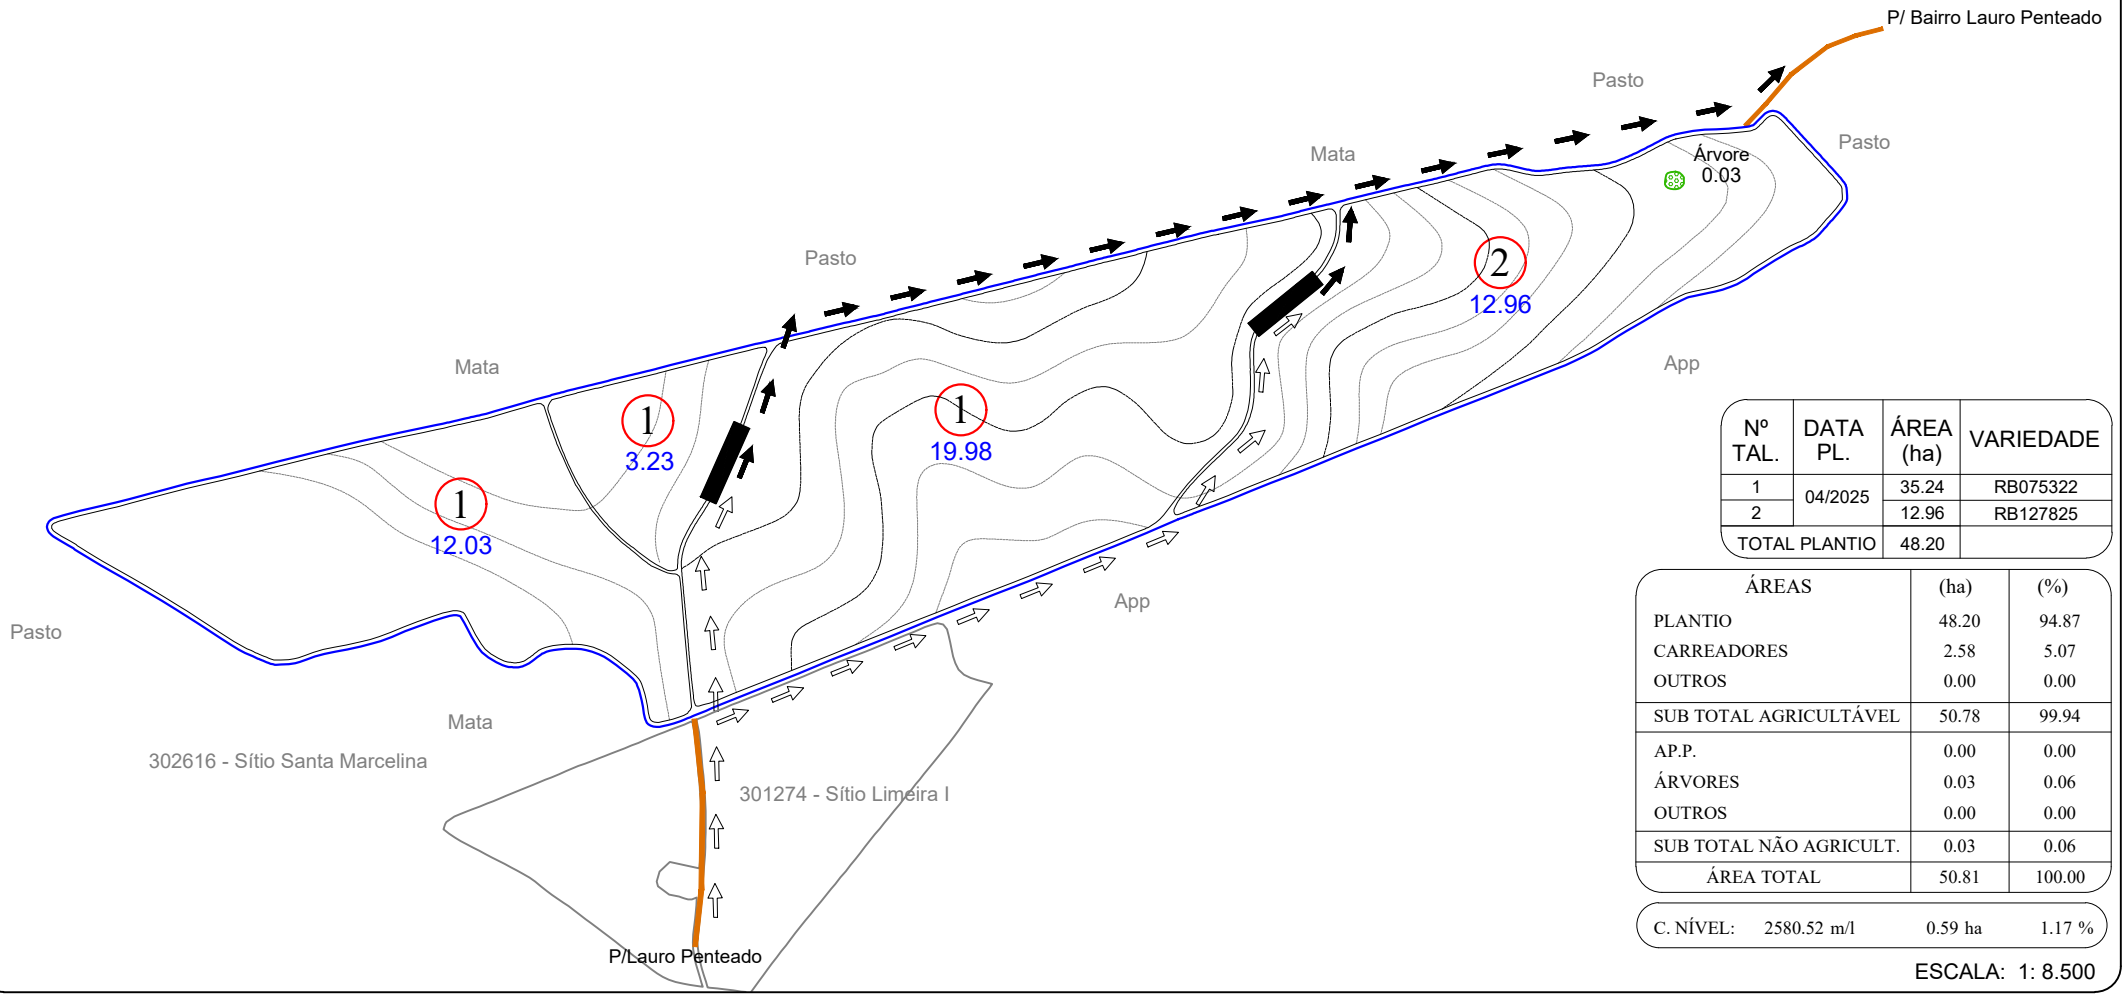


Nº TAL.	DATA PL.	ÁREA (ha)	VARIEDADE
1	04/2025	35.24	RB075322
2		12.96	RB127825
TOTAL PLANTIO		48.20	

ÁREAS	(ha)	(%)
PLANTIO	48.20	94.87
CARREADORES	2.58	5.07
OUTROS	0.00	0.00
SUB TOTAL AGRICULTÁVEL	50.78	99.94
AP.P.	0.00	0.00
ÁRVORES	0.03	0.06
OUTROS	0.00	0.00
SUB TOTAL NÃO AGRICULT.	0.03	0.06
ÁREA TOTAL	50.81	100.00

C. NÍVEL: 2580.52 m/l 0.59 ha 1.17 %


ESCALA: 1: 8.500

LEGENDA

- FAZENDA
- TALHÃO
- REDE ELÉTRICA
- TERRAÇO BASE LARGA
- TERRAÇO EMBUTIDO
- VAZIO
- CARREGADO

ESPAÇAMENTO: 1.50 x 1.50
TIRO MÉDIO ESTIMADO: 232.66 m
D.V: 5.09 %

CROQUI DE ACESSO

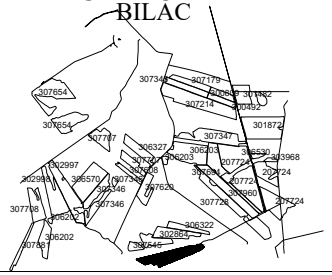

SÍTIO SÃO JOSÉ

PROPRIETÁRIO: JORGE LUIZ ZAGO
COMPRADOR: CLEALCO
MUNICÍPIO: BILAC - SP

DISTÂNCIAS (km):
UNID. I - Asfalto: 21.00 Terra.: 1.77
UNID.I I - Asfalto: 70.00 Terra.: 3.00

COORDENADAS: E(X): 555584.73 N(Y): 7626075.96
LAT: -21°28'1.0558" LONG: -50°27'48.5450"

CLEALCO - AÇÚCAR E ALCOOL S/A - DEPARTAMENTO DE GEOTECNOLOGIA

UNIDADE: I
PARTE: A/A
FUNDO AGRÍCOLA: 306357

M:\01-Mapa de safra\Mapas Atualizados\Terceiro\306357 - Sítio Sao José (Jorge Luíz Zago)\306357 - Sítio Sao José (Jorge Luíz Zago).dwg

Bruno Gamboa 03/12/25