

Clealco
Açúcar, Etanol e Energia

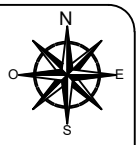

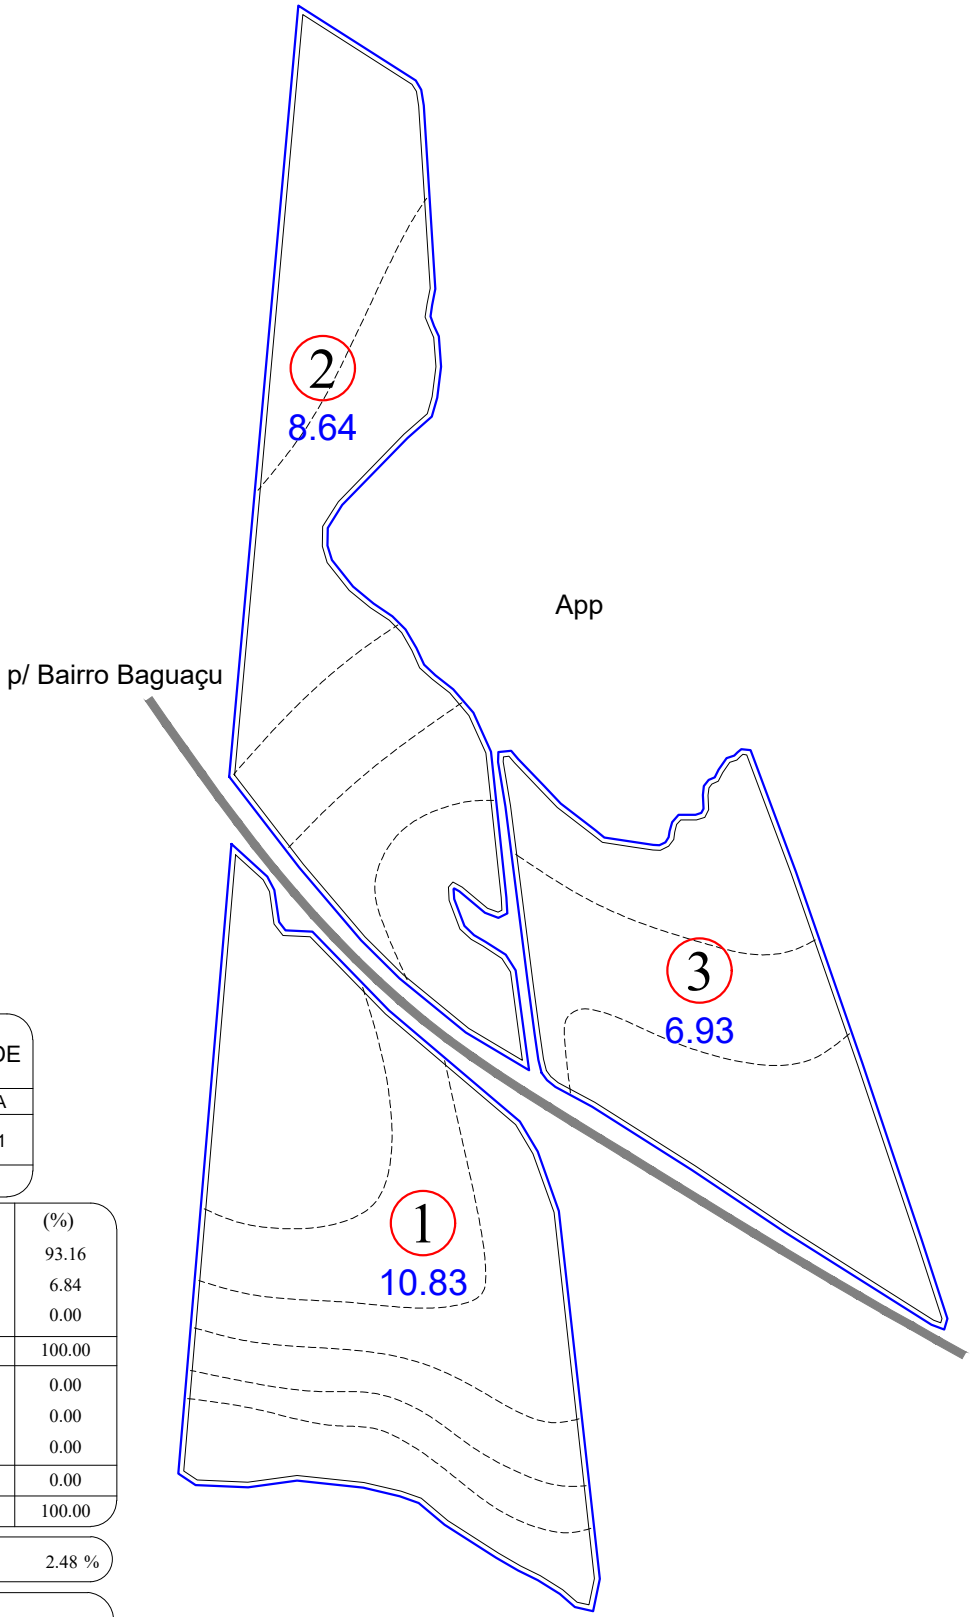

Nº TAL.	DATA PL.	ÁREA (ha)	VARIEDADE
1	2026	10.83	REFORMA
2	04/2020	8.64	RB 975201
3	04/2021	6.93	
TOTAL PLANTIO		26.40	

ÁREAS	(ha)	(%)
PLANTIO	26.40	93.16
CARREADORES	1.94	6.84
OUTROS	0.00	0.00
SUB TOTAL AGRICULTÁVEL	28.34	100.00
AP.P.	0.00	0.00
ÁRVORES	0.00	0.00
OUTROS	0.00	0.00
SUB TOTAL NÃO AGRICULT.	0.00	0.00
ÁREA TOTAL	28.34	100.00

C. NÍVEL: 3057.79 m/l 0.70 ha 2.48 %


LEGENDA

- FAZENDA
- TALHÃO
- REDE ELÉTRICA
- TERRAÇO BASE LARGA
- TERRAÇO EMBUTIDO
- (P.O.A) PATIO DE OPERAÇÃO

ESPAÇAMENTO: 1.50 x 1.50
TIRO MÉDIO ESTIMADO: 000.00 m
D.V: 0.00 %

ESCALA: 1: 6.000

CROQUI DE ACESSO

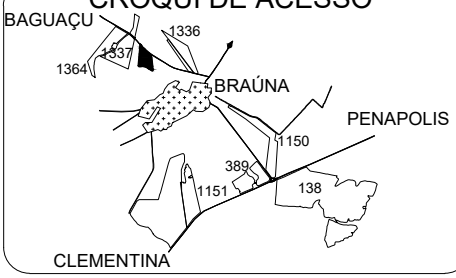

SITIO SÃO LUÍZ

PROPRIETÁRIO: RODOLFO SERISAVA PITA
COMPRADOR: CLEALCO
MUNICÍPIO: COROADOS - SP

DISTÂNCIAS (km):
UNID. I - Asfalto: 23.50 Terra.: 0.00
UNID.I I - Asfalto: 75.00 Terra.: 0.00

COORDENADAS: E(X): 569599.80 N(Y): 7623290.24
LAT: -21°29'29.9002" LONG: -50°19'41.1571"

CLEALCO - AÇÚCAR E ALCOOL S/A - DEPARTAMENTO DE GEOTECNOLOGIA

LEVANTAMENTO VIA:
- SATÉLITE
- GPS / VANT
- GOOGLE

UNIDADE: I
PARTE: A/A
FUNDO AGRÍCOLA: 306361

M:\01-Mapa de safra\Mapas Atualizados\Terceiro\306361 - Sitio Sao Luiz (Rodolfo Serisava Pitta)\306361 - Sitio Sao Luiz (Rodolfo Serisava Pitta).dwg

Benati 05/03/2026