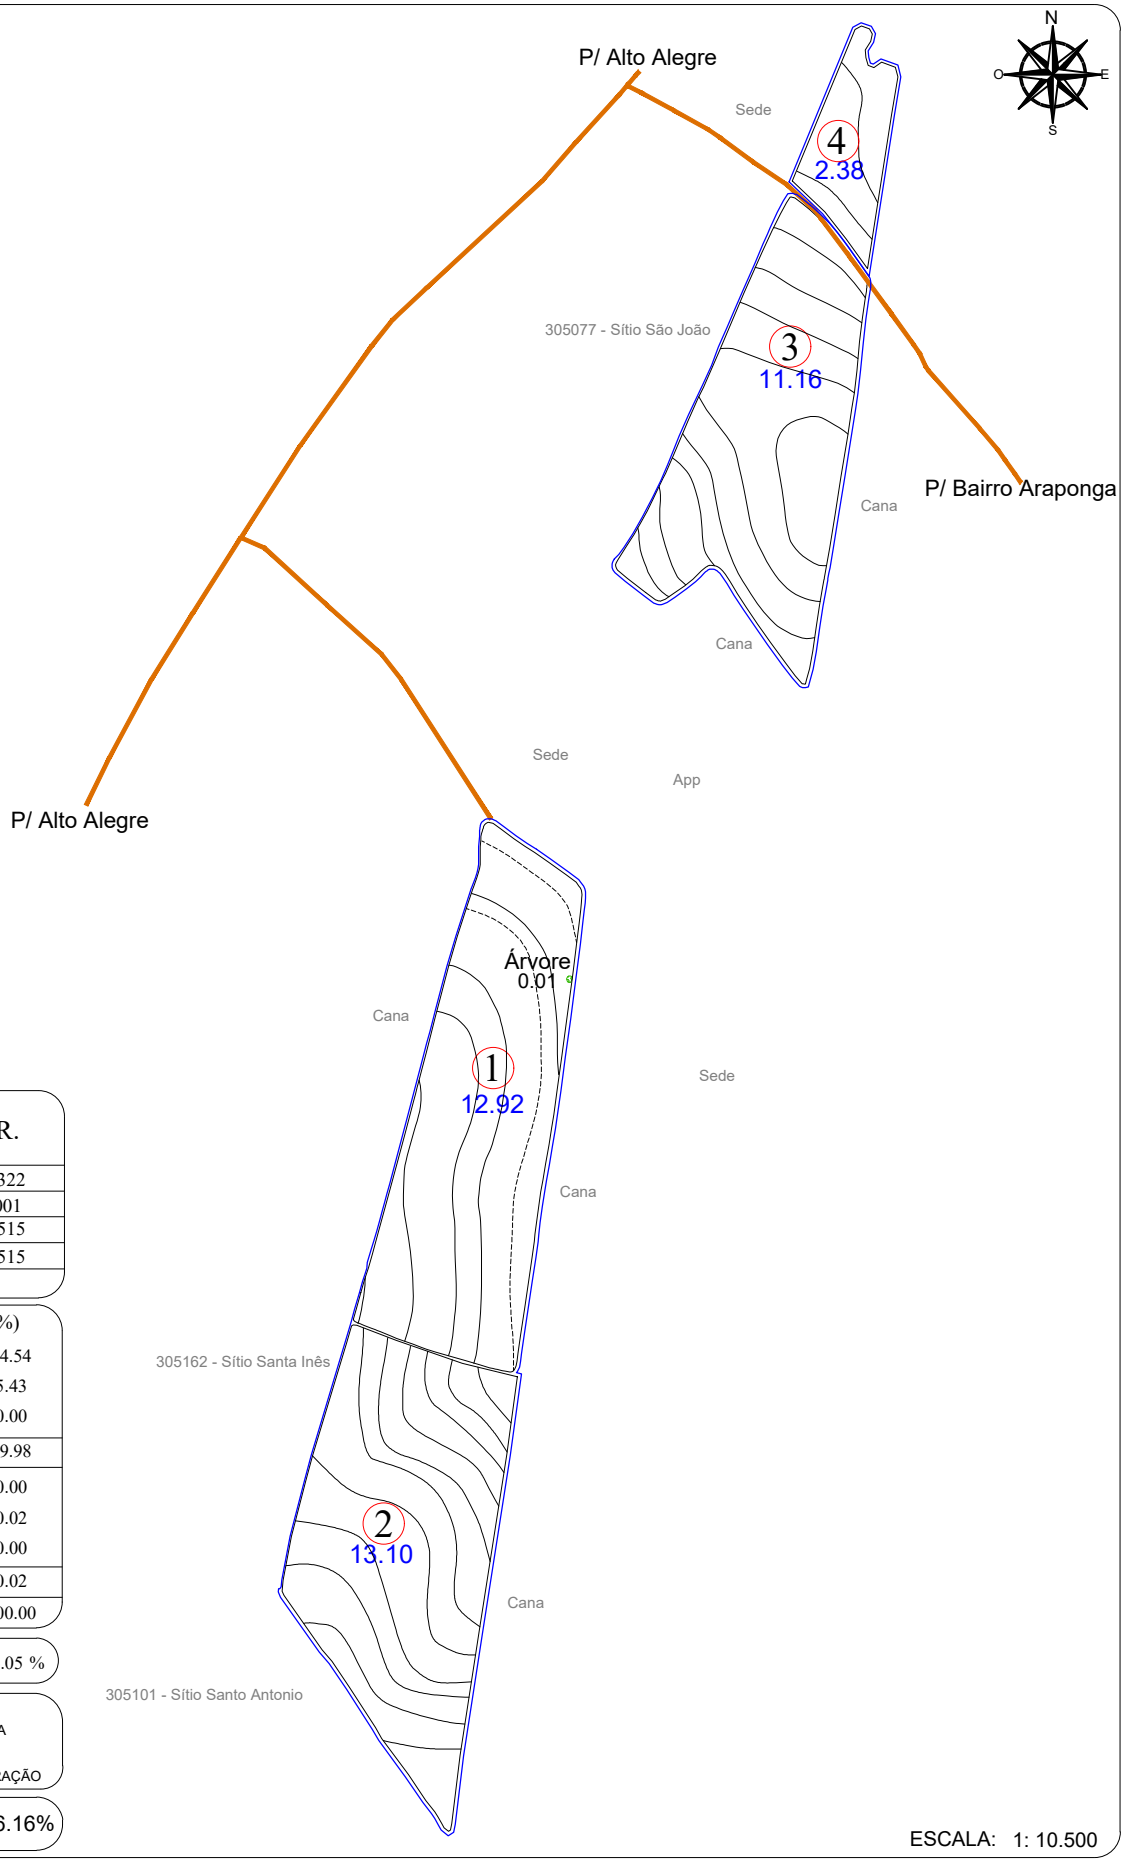


ZONA	Nº TAL.	DATA PL.	ÁREA (ha)	VAR.
1	1	04/2026	12.92	RB07 5322
999	2	03/2022	13.10	CTC 9001
1	3	04/2025	11.16	RB86 7515
999	4	05/2024	2.38	RB86 7515
TOTAL PLANTIO			39.56	

ÁREAS	(ha)	(%)
PLANTIO	39.56	94.54
CARREADORES	2.27	5.43
OUTROS	0.00	0.00
SUB TOTAL AGRICULTÁVEL	41.83	99.98
AP.P.	0.00	0.00
ÁRVORES	0.01	0.02
OUTROS	0.00	0.00
SUB TOTAL NÃO AGRICULT.	0.01	0.02
ÁREA TOTAL	41.84	100.00

C. NÍVEL: 7363.79 m/l 1.69 ha 4.05 %


LEGENDA

- FAZENDA
- TALHÃO
- REDE ELÉTRICA
- TERRAÇO BASE LARGA
- TERRAÇO EMBUTIDO
- (P.O.A) PATIO DE OPERAÇÃO

ESPAÇAMENTO: 1.50 x 1.50
TIRO MÉDIO ESTIMADO: 178.32 m
D.V: 6.16%

ESCALA: 1: 10.500

CROQUI DE ACESSO

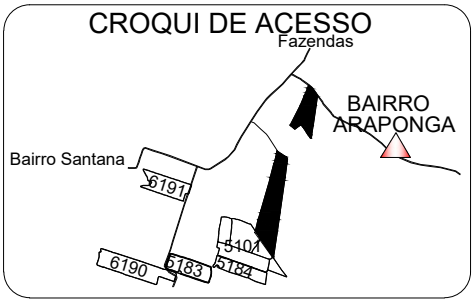

SITIO SANTA CLARA I

PROPRIETÁRIO: MARIA JOSÉ DE A. CRIVELLARO
COMPRADOR: CLEALCO
MUNICÍPIO: PENAPOLIS - SP

DISTÂNCIAS (km):
UNID. I - Asfalto: 51.60 Terra.: 6.20
UNID.I I - Asfalto: 48.00 Terra.: 4.00

COORDENADAS: E(X): 594440.31 N(Y): 7614519.44
LAT: -21°34'11.0550" LONG: -50°5'16.1515"

CLEALCO - AÇÚCAR E ALCOOL S/A - DEPARTAMENTO DE GEOTECNOLOGIA

LEVANTAMENTO VIA:
- SATÉLITE
- GPS / VANT
- GOOGLE

UNIDADE: II
PARTE: A/A
FUNDO AGRÍCOLA: 306366

M:\01-Mapa de safra\Mapas Atualizados\Terceiro\306366 - Sítio Santa Clara I (Maria José Andrade Crivellaro)\306366 - Sítio Santa Clara I (Maria José Andrade Crivellaro).dwg

Bruno Gamboa 27/08/26