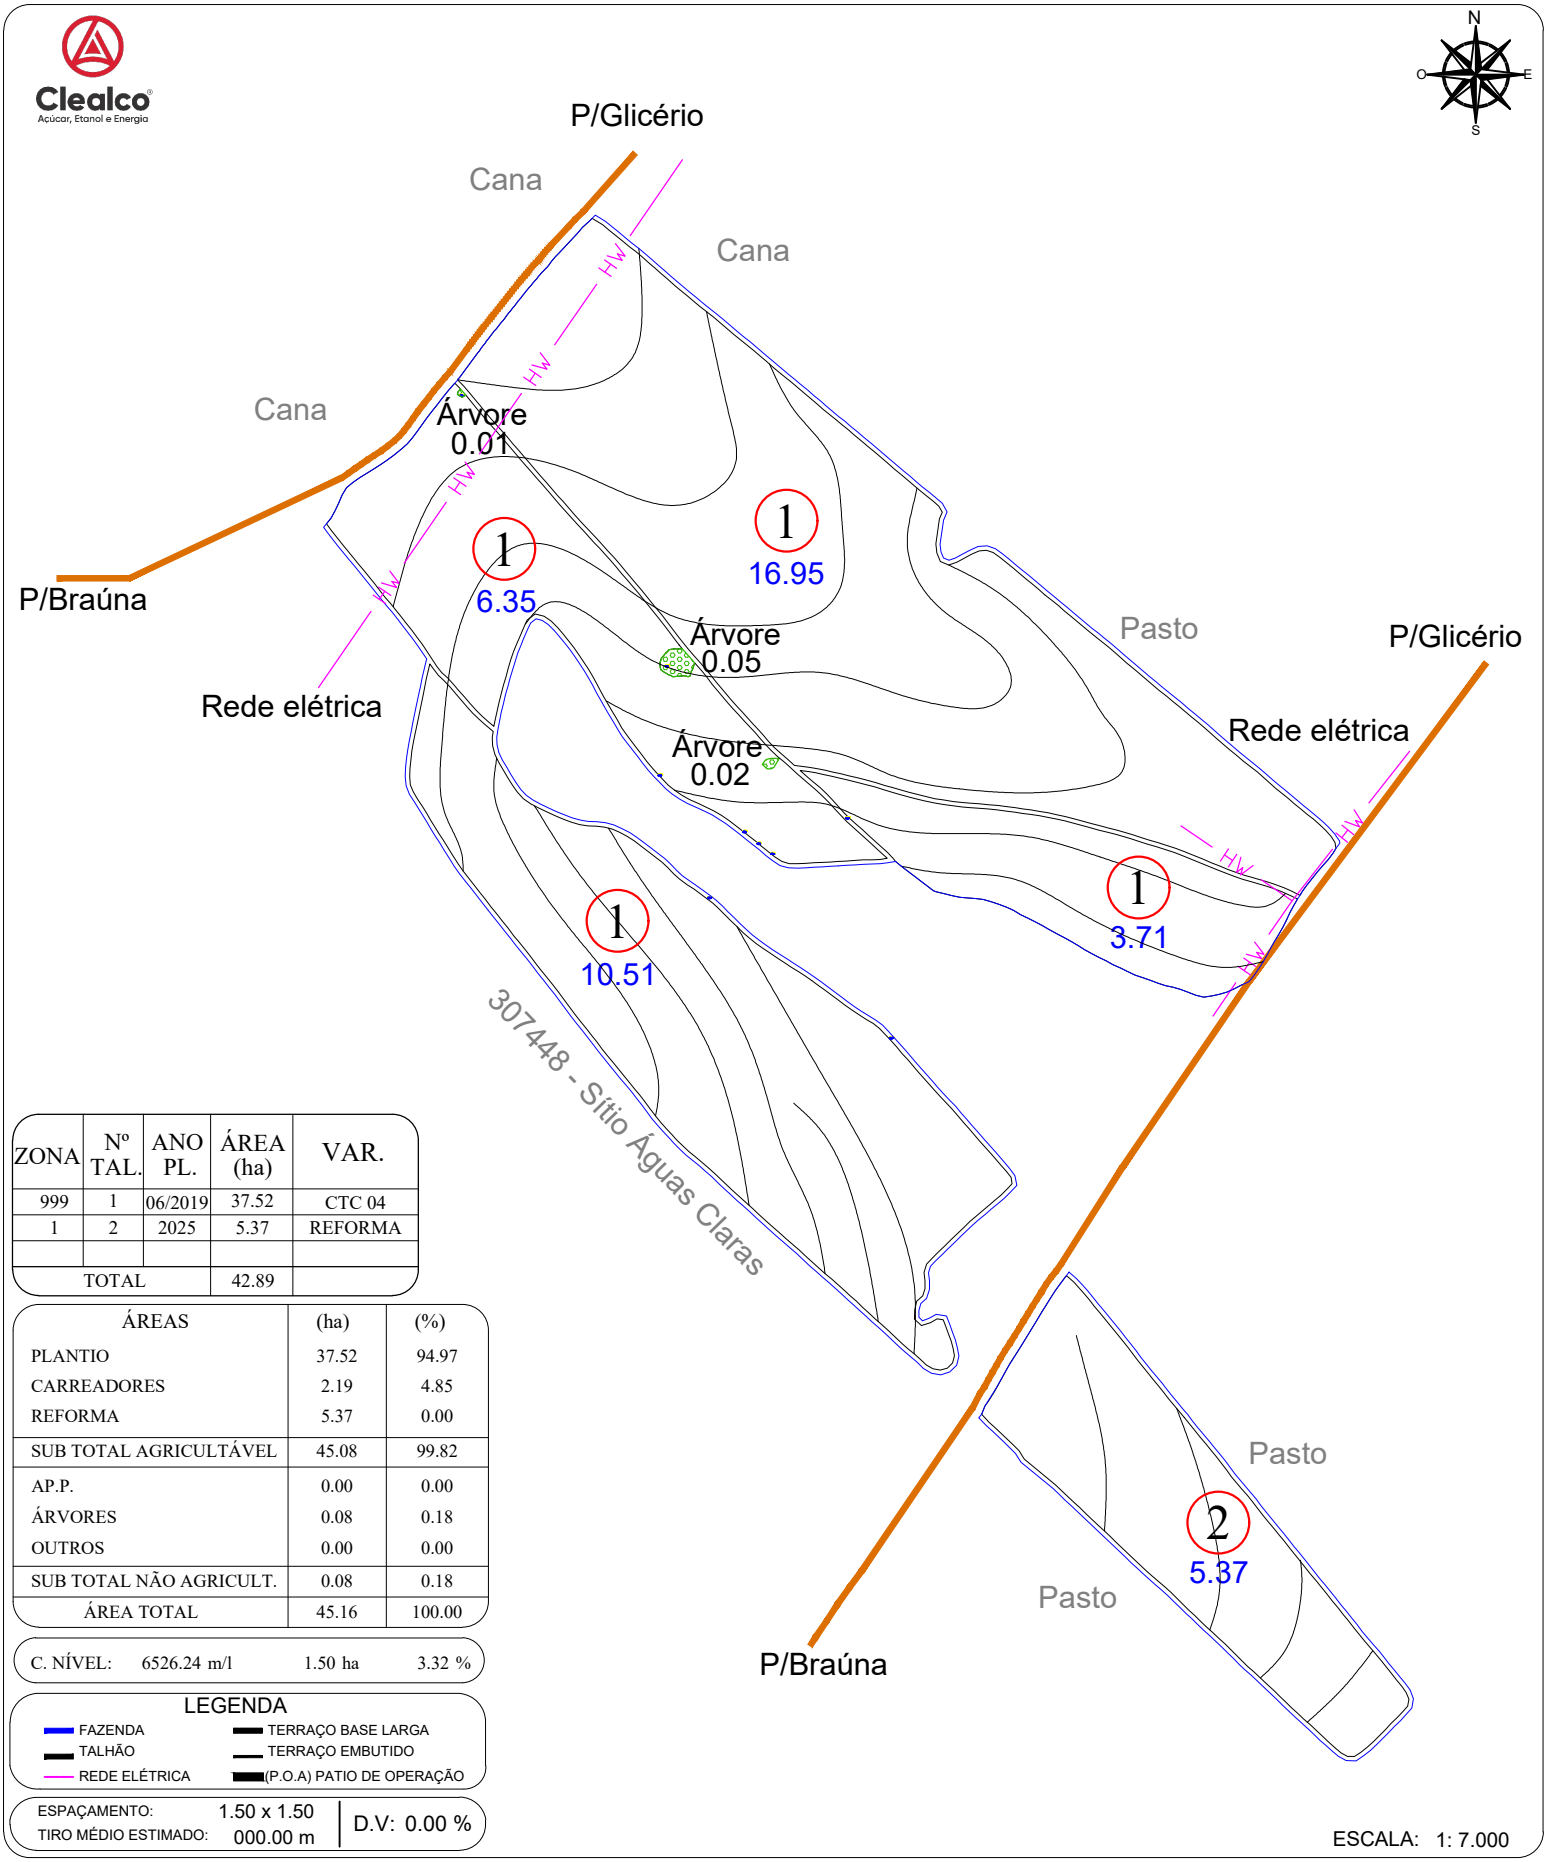


ZONA	Nº TAL.	ANO PL.	ÁREA (ha)	VAR.
999	1	06/2019	37.52	CTC 04
1	2	2025	5.37	REFORMA
TOTAL			42.89	

ÁREAS	(ha)	(%)
PLANTIO	37.52	94.97
CARREADORES	2.19	4.85
REFORMA	5.37	0.00
SUB TOTAL AGRICULTÁVEL	45.08	99.82
AP.P.	0.00	0.00
ÁRVORES	0.08	0.18
OUTROS	0.00	0.00
SUB TOTAL NÃO AGRICULT.	0.08	0.18
ÁREA TOTAL	45.16	100.00

C. NÍVEL: 6526.24 m/l 1.50 ha 3.32 %


LEGENDA

- FAZENDA
- TALHÃO
- REDE ELÉTRICA
- TERRAÇO BASE LARGA
- TERRAÇO EMBUTIDO
- (P.O.A) PATIO DE OPERAÇÃO

ESPAÇAMENTO: 1.50 x 1.50
TIRO MÉDIO ESTIMADO: 000.00 m
D.V: 0.00 %

ESCALA: 1: 7.000

CROQUI DE ACESSO

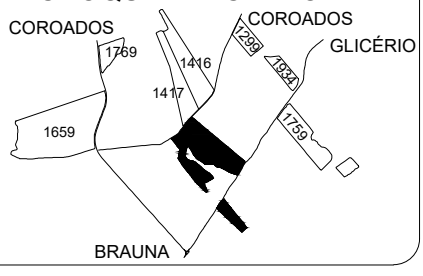

SÍTIO ÁGUA LIMPA

PROPRIETÁRIO: ALCIDES SOLCIA
COMPRADOR: CLEALCO
MUNICÍPIO: BRAÚNA - SP

DISTÂNCIAS (km):
UNID. I - Asfalto: 30.70 Terra.: 7.50
UNID.I I - Asfalto: 36.50 Terra.: 0.00

COORDENADAS: E(X): 572210.75 N(Y): 7624077.32
LAT: -21°29'3.9292" LONG: -50°18'10.5443"

CLEALCO - AÇÚCAR E ALCOOL S/A - DEPARTAMENTO DE GEOTECNOLOGIA

LEVANTAMENTO VIA:
- SATÉLITE
- GPS / VANT
- GOOGLE

UNIDADE: I
PARTE: A/A
FUNDO AGRÍCOLA: 306399

M:\01-Mapa de safra\Mapas Atualizados\Terceiro\306399 - Sitio Agua Limpa (Alcides Solcia)\306399 - Sitio Agua Limpa (Alcides Solcia).dwg

Bruno Gamboa 24/07/25