
Clealco
Açúcar, Etanol e Energia

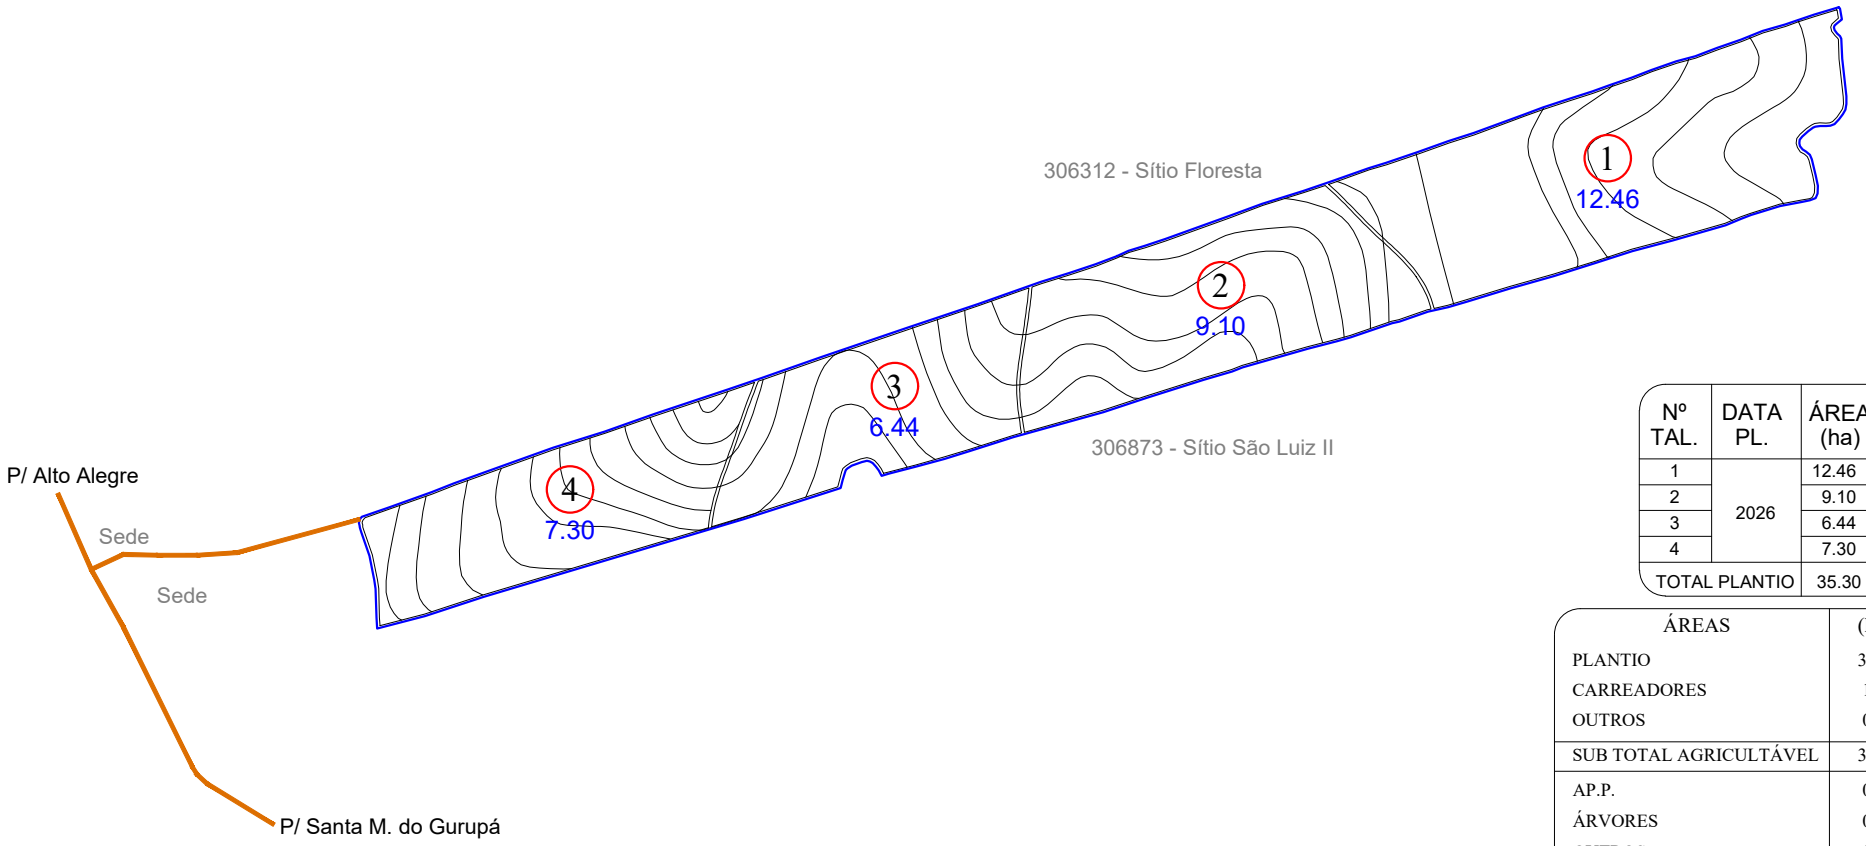

Nº TAL.	DATA PL.	ÁREA (ha)	VARIEDADE
1	2026	12.46	REFORMA
2		9.10	
3		6.44	
4		7.30	
TOTAL PLANTIO		35.30	

ÁREAS	(ha)	(%)
PLANTIO	35.30	96.10
CARREADORES	1.43	3.90
OUTROS	0.00	0.00
SUB TOTAL AGRICULTÁVEL	36.73	100.00
AP.P.	0.00	0.00
ÁRVORES	0.00	0.00
OUTROS	0.00	0.00
SUB TOTAL NÃO AGRICULT.	0.00	0.00
ÁREA TOTAL	36.73	100.00


C. NÍVEL: 7500.28 m/l 1.73 ha 4.70 %

ESCALA: 1: 10.000

LEGENDA
- FAZENDA
- TALHÃO
- REDE ELÉTRICA
- TERRAÇO BASE LARGA
- TERRAÇO EMBUTIDO
- VAZIO
- CARREGADO

ESPAÇAMENTO: 1.50 x 1.50
TIRO MÉDIO ESTIMADO: 175.50 m
D.V: 5.70 %

CROQUI DE ACESSO

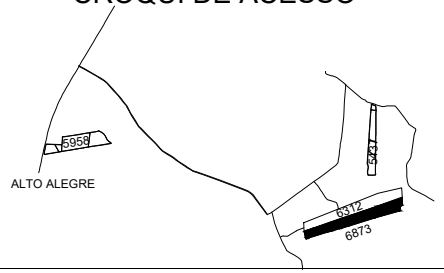

SÍTIO SÃO LUIZ II

PROPRIETÁRIO: JOSÉ CARLOS D. GILBERTO
COMPRADOR: CLEALCO
MUNICÍPIO: ALTO ALEGRE - SP

DISTÂNCIAS (km):
UNID. I - Asfalto: 49.20 Terra.: 5.60
UNID.I I - Asfalto: 50.00 Terra.: 6.50

COORDENADAS: E(X): 596770.53 N(Y): 7616617.98
LAT: -21°33'2.3574" LONG: -50°3'55.5713"
CLEALCO - AÇÚCAR E ALCOOL S/A - DEPARTAMENTO DE GEOTECNOLOGIA

LEVANTAMENTO VIA:
- SATÉLITE
- GPS / VANT
- GOOGLE

UNIDADE: I
PARTE: A/A
FUNDO AGRÍCOLA: 306418

M:\01-Mapa de safra\Mapas Atualizados\Terceiro\306418 - Sítio São Luiz II (José Carlos Donizete Gilberto)\306418 - Sítio São Luiz II (José Carlos Donizete Gilberto).dwg

Bruno Gamboa 26/03/26