ZONA DV	Nº TAL.	DATA PL.	ÁREA (ha)	VARIEDADE
999	1	05/2023	13.12	RB966928
5.69 %	2	05/2022	33.23	CTC 9001
TOTAL PLANTIO			46.35	--------

ÁREAS	(ha)	(%)
PLANTIO	46.35	96.72
CARREADORES	1.35	2.82
OUTROS	0.00	0.00
SUB TOTAL AGRICULTÁVEL	47.70	99.54
AP.P.	0.00	0.00
ÁRVORES	0.22	0.46
OUTROS	0.00	0.00
SUB TOTAL NÃO AGRICULT.	0.22	0.46
ÁREA TOTAL	47.92	100.00

C. NÍVEL: 8288.70 m/l 1.91 ha 3.98 %

LEGENDA

FAZENDA	CONFRONTANTE
TALHÃO	REDE ELÉTRICA
CURVA DE NÍVEL	TRAJETO VAZIO
CARREADOR	TRAJETO CARREGADO

PLANTIO MANUAL - ESPAÇAMENTO: 1.50 X 1.50
TIRO MÉDIO ESTIMADO: 248.14m

Clealco
Açúcar, Etanol e Energia

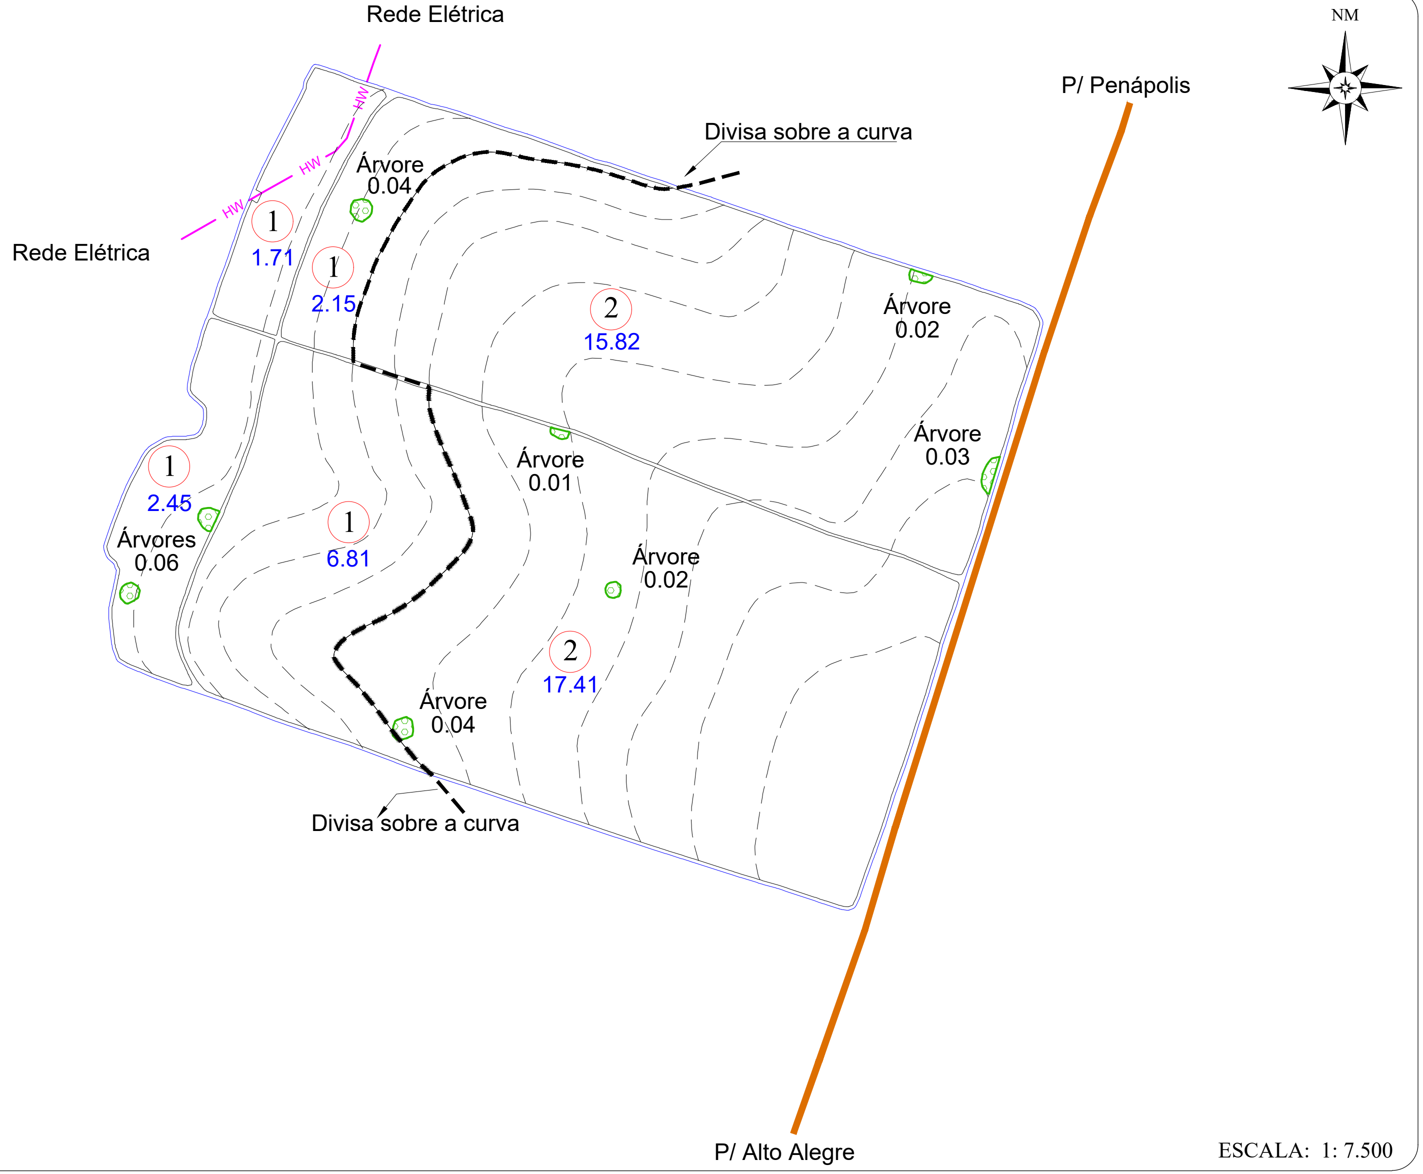

ESCALA: 1: 7.500

CROQUI DE ACESSO

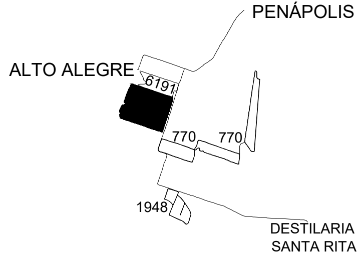

SÍTIO SÃO FRANCISCO

PROPRIETÁRIO: ANTÔNIO I. DE ANDRADE
COMPRADOR: CLEALCO S/A
MUNICÍPIO: PENÁPOLIS

DISTÂNCIAS (km):

	Asfalto	Terra
UNID. I	57.00	1.00
UNID. I I	46.00	4.00
UNID. III	18.00	1.00

COORDENADAS: E(X): 592851.78 N(Y): 7614372.44
LAT: -21°34'16.1354" LONG: -50°6'11.3530"

CLEALCO - AÇÚCAR E ALCOOL S/A - DEPARTAMENTO DE TOPOGRAFIA

UNIDADE:
I

PARTE:
A/A

FUNDO AGRÍCOLA:
306422

M:\03-Projetos (Sistematização, Pré, Pós e outros)\Terceiro\2023\Joao\Pós Plantio\306422 - Sitio São Francisco (Antonio Irvando de Andrade) - Pos plantio.dwg

Bruno Gamboa 22/01/24