ZONA DV	CLA	Nº TAL.	DATA PL.	ÁREA (ha)	VAR.
999		1	05/2018	11.34	CTC 04
		2	06/2020	21.96	
		3		34.69	
		4		7.11	
		5		10.11	
		6		36.28	
		7		27.81	
TOTAL PLANTIO				149.30	--------


ÁREAS	(ha)	(%)
PLANTIO	149.30	89.70
CARREADORES	8.62	5.39
OUTROS	0.00	0.00
SUB TOTAL AGRICULTÁVEL	157.92	--------
SEDE	8.06	0.00
ÁRVORE	0.06	0.00
REDE ELÉTRICA	0.12	0.00
SUB TOTAL NÃO AGRICULT.	0.00	0.00
ÁREA TOTAL	166.16	--------

C. NÍVI 12032.39 m/l 2.77 ha 276.74 %

LEGENDA


- FAZENDA
- TALHÃO
- CURVA DE NÍVEL
- CARREADOR
- CONFRONTANTE
- REDE ELÉTRICA
- TRAJETO VAZIO
- TRAJETO CARREGADO

TIPO DE PLANTIO: CONVENCIONAL: 149.05 ha
ESPAÇAMENTO: 0.00 MECANIZADO: 0.00 ha

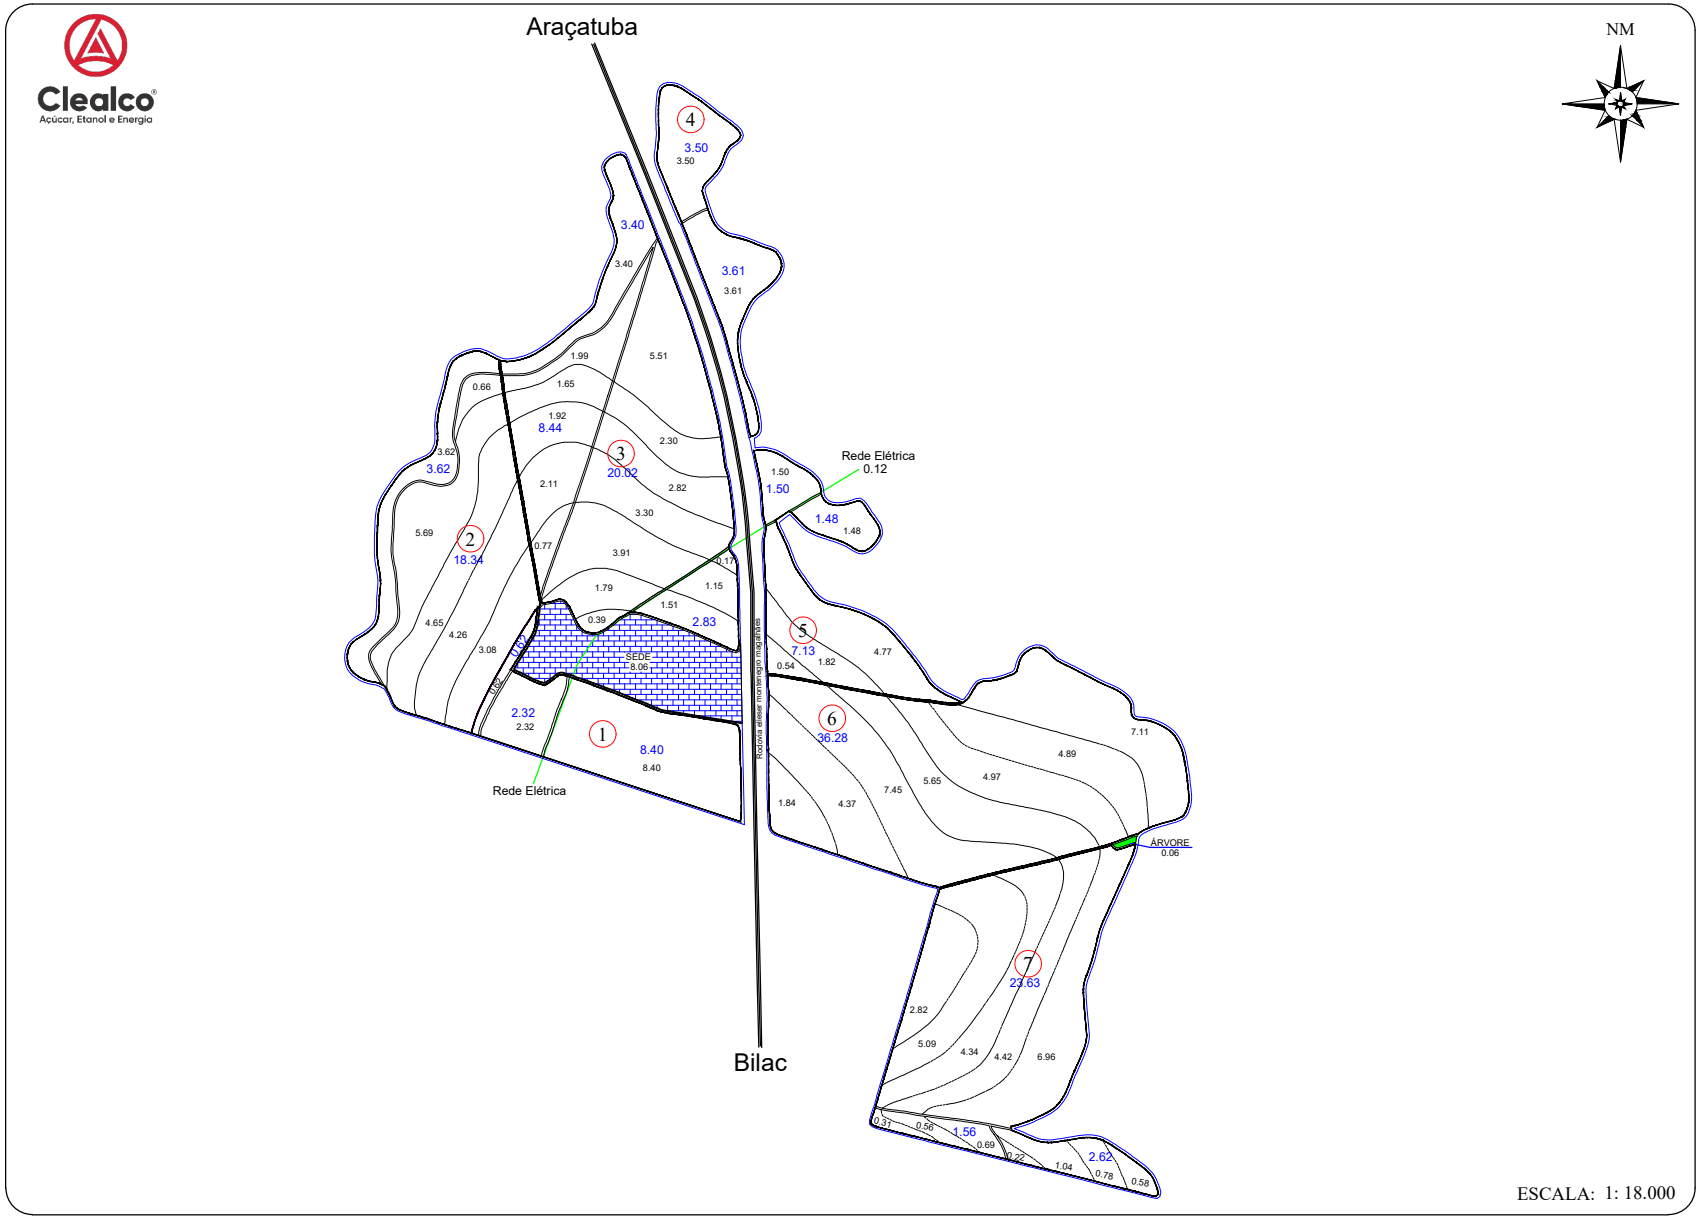

ESCALA: 1: 18.000

CROQUI DE ACESSO

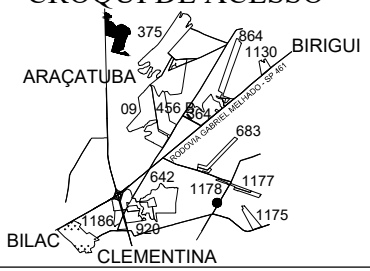

FAZENDA DOIS CORREGOS

PROPRIETÁRIO: RODRIGO DE SOUZA E EUTROS
COMPRADOR: CLEALCO S/A
MUNICÍPIO: BILAC

DISTÂNCIAS (km):
UNID. I - Asfalto: 30.50 Terra.: 0.00
UNID.I I - Asfalto: 98.00 Terra.: 0.00
UNID. III -Asfalto: 58.18 Terra.: 0.00

COORDENADAS: E(X): 555441 N(Y): 7642286
LAT: 21°19'13,00000" LONG: 50°27'55,00000"

CLEALCO - AÇÚCAR E ALCOOL S/A - DEPARTAMENTO DE TOPOGRAFIA

UNIDADE: I
PARTE: A/A
FUNDO AGRÍCOLA: 306426