ZONA D.V.	Nº TAL.	DATA PL.	ÁREA (ha)	VARIEDADE
999 3.85 %	1	05/2023	29.71	CTC 04
TOTAL PLANTIO			29.71	--------

ÁREAS	(ha)	(%)
PLANTIO	29.71	94.70
CARREADORES	1.49	4.76
OUTROS	0.08	0.25
SUB TOTAL AGRICULTÁVEL	31.28	99.71
AP.P.	0.00	0.00
ÁRVORES	0.00	0.00
OUTROS	0.09	0.29
SUB TOTAL NÃO AGRICULT.	0.09	0.29
ÁREA TOTAL	31.37	100.00

C. NÍVEL:	1660.32 m/l	0.38 ha	1.22 %

LEGENDA

▬ FAZENDA	▬ CONFRONTANTE
▬ TALHÃO	-·- REDE ELÉTRICA
▪▪▪ CURVA DE NÍVEL	—▷ TRAJETO VAZIO
— CARREADOR	—► TRAJETO CARREGADO

PLANTIO MANUAL - ESPAÇAMENTO: 1.50 X 1.50
TIRO MÉDIO ESTIMADO: 376.99 m

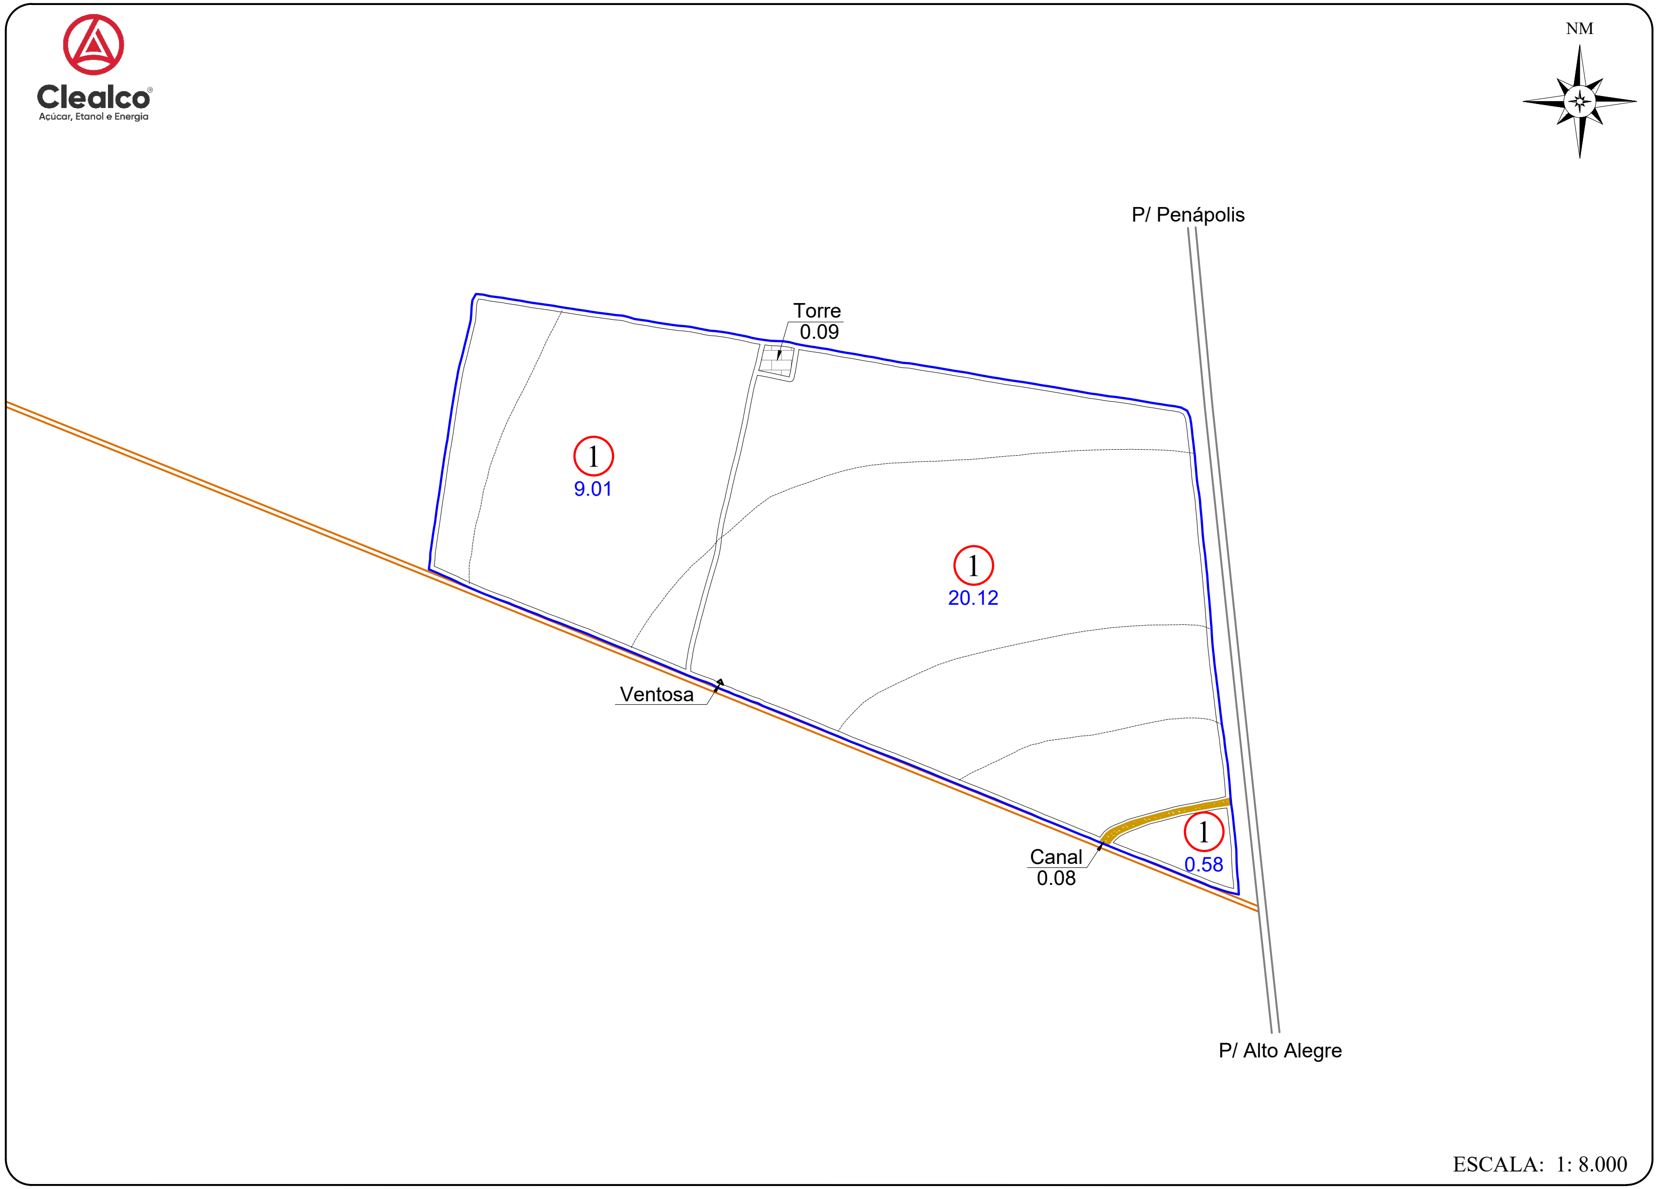
Clealco®
Açúcar, Etanol e Energia
NM
P/ Penápolis
Torre
0.09
1
9.01
1
20.12
Ventosa
1
0.58
Canal
0.08
P/ Alto Alegre

ESCALA: 1: 8.000

CROQUI DE ACESSO

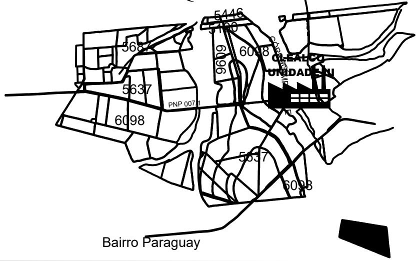
5446
5100
5687
6098
9609
CLEALCO
UNIDADE II
5637
PNP 0071
6098
5637
6098
Bairro Paraguay

FAZENDA CAMPESTRE

PROPRIETÁRIO: VALDIR PEREIRA DE SOUZA
COMPRADOR: CLEALCO S/A
MUNICÍPIO: PENÁPOLIS

DISTÂNCIAS (km):

UNID. I -	Asfalto:	60.70	Terra.:	2.50
UNID.I I -	Asfalto:	49.50	Terra.:	2.50
UNID. III -	Asfalto:	0.00	Terra.:	2.50

COORDENADAS: E(X):	592212.89	N(Y):	7622175.95
LAT:	-21°30'2.4664"	LONG:	-50°6'35.1138"

CLEALCO - AÇÚCAR E ALCOOL S/A - DEPARTAMENTO DE TOPOGRAFIA

UNIDADE:
I

PARTE:
A/A

FUNDO AGRÍCOLA:
306445

M:\03-Projetos (Sistematização, Pré, Pós e outros)\Terceiro_2024\Familia Andrade\306445 A - Fazenda Campestre (Valdir Pereira de Souza) - 2024.dwg

Fernanda Bezerra 26/10/23