
Clealco
Açúcar, Etanol e Energia

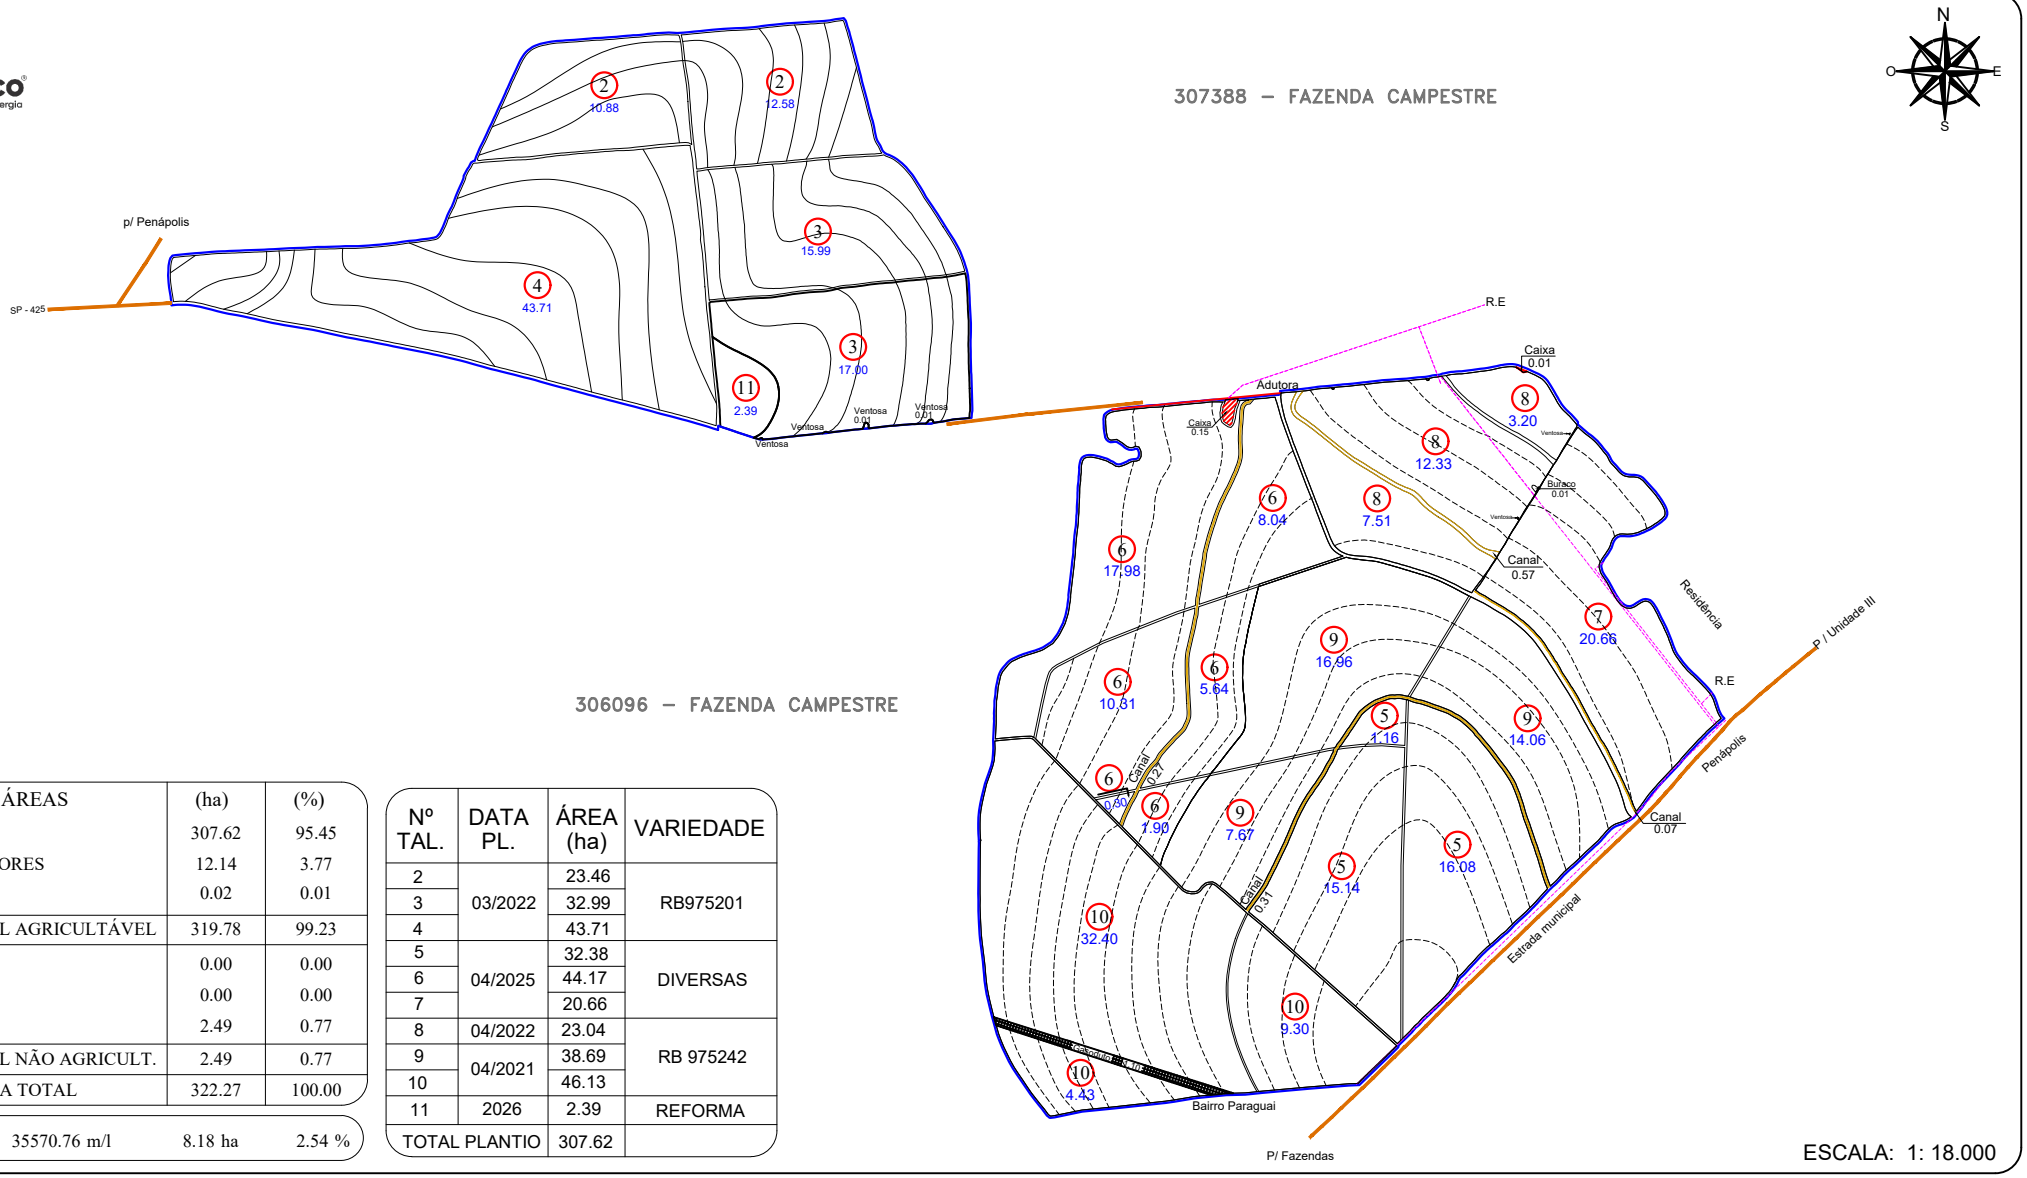

ESCALA: 1: 18.000

ÁREAS	(ha)	(%)
PLANTIO	307.62	95.45
CARREADORES	12.14	3.77
OUTROS	0.02	0.01
SUB TOTAL AGRICULTÁVEL	319.78	99.23
AP.P.	0.00	0.00
ÁRVORES	0.00	0.00
OUTROS	2.49	0.77
SUB TOTAL NÃO AGRICULT.	2.49	0.77
ÁREA TOTAL	322.27	100.00

C. NÍVEL: 35570.76 m/l 8.18 ha 2.54 %


Nº TAL.	DATA PL.	ÁREA (ha)	VARIEDADE
2	03/2022	23.46	RB975201
3		32.99	
4		43.71	
5	04/2025	32.38	DIVERSAS
6		44.17	
7		20.66	
8	04/2022	23.04	RB 975242
9	04/2021	38.69	
10		46.13	
11	2026	2.39	REFORMA
TOTAL PLANTIO		307.62	

LEGENDA

- FAZENDA
- TALHÃO
- REDE ELÉTRICA
- TERRAÇO BASE LARGA
- TERRAÇO EMBUTIDO

ESPAÇAMENTO: 1.50 x 1.50
TIRO MÉDIO ESTIMADO: 000.00 m
D.V: 0.00 %

CROQUI DE ACESSO

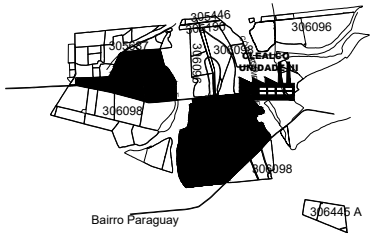

FAZENDA CAMPESTRE

PROPRIETÁRIO: VALDIR PEREIRA DE SOUZA
COMPRADOR: CLEALCO
MUNICÍPIO: PENÁPOLIS

DISTÂNCIAS (km):
UNID. I - Asfalto: 60.70 Terra.: 2.50
UNID.I I - Asfalto: 49.50 Terra.: 2.50

COORDENADAS: E(X): 588794.42 N(Y): 7624777.32
LAT: -21°28'38.4840" LONG: -50°8'34.4091"

CLEALCO - AÇÚCAR E ALCOOL S/A - DEPARTAMENTO DE GEOTECNOLOGIA

LEVANTAMENTO VIA:
- SATÉLITE
- GPS / VANT
- GOOGLE

UNIDADE: I
PARTE: A/A
FUNDO AGRÍCOLA: 306445

M:\01-Mapa de safra\Mapas Atualizados\Terceiro\306445 - Fazenda Campestre (Valdir Pereira de Souza)\306445 B - Fazenda Campestre (Valdir Pereira de Souza).dwg

Benati 10/03/2026