
Clealco
Açúcar, Etanol e Energia

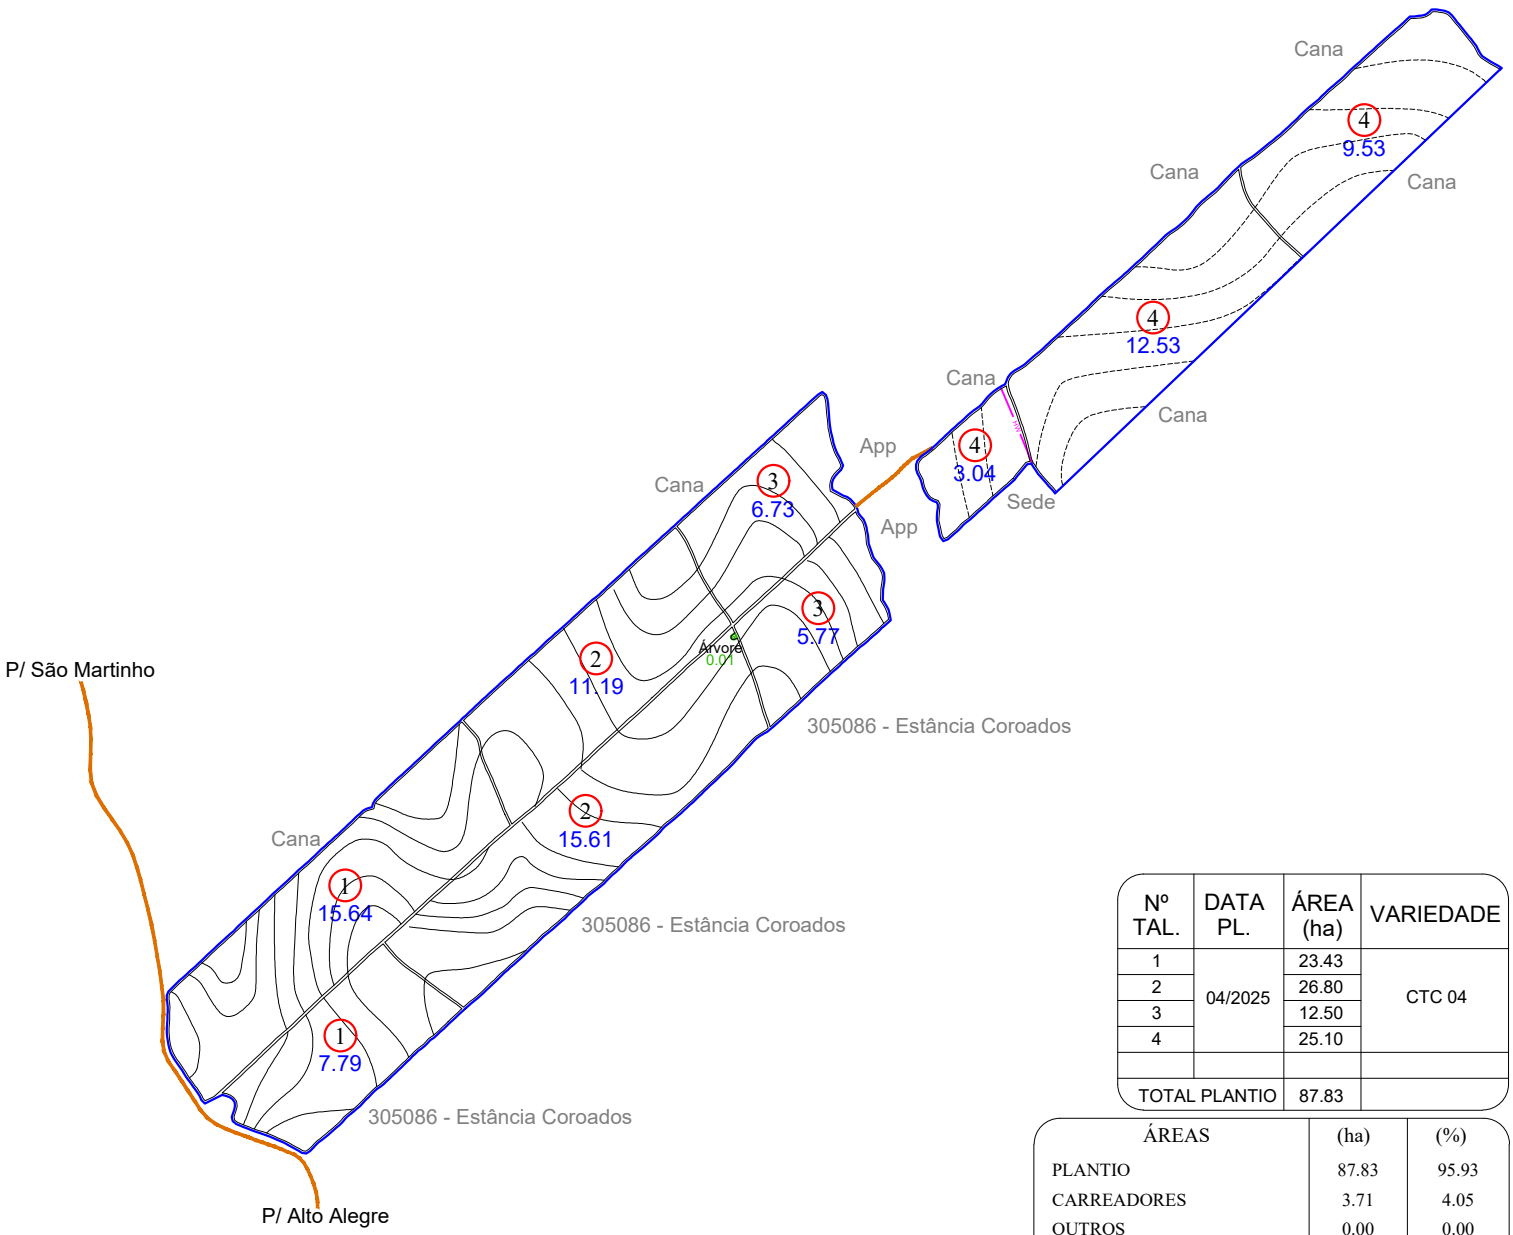

Nº TAL.	DATA PL.	ÁREA (ha)	VARIEDADE
1	04/2025	23.43	CTC 04
2		26.80	
3		12.50	
4		25.10	
TOTAL PLANTIO		87.83	

ÁREAS	(ha)	(%)
PLANTIO	87.83	95.93
CARREADORES	3.71	4.05
OUTROS	0.00	0.00
SUB TOTAL AGRICULTÁVEL	91.54	99.99
AP.P.	0.00	0.00
ÁRVORES	0.01	0.01
OUTROS	0.00	0.00
SUB TOTAL NÃO AGRICULT.	0.01	0.01
ÁREA TOTAL	91.55	100.00

C. NÍVEL: 10151.82 m/l 2.33 ha 2.55 %


ESCALA: 1: 14.500

LEGENDA

- FAZENDA
- TALHÃO
- REDE ELÉTRICA
- VAZIO
- TERRAÇO BASE LARGA
- TERRAÇO EMBUTIDO
- (P.O.A) PATIO DE OPERAÇÃO
- CARREGADO

ESPAÇAMENTO: 1.50 x 1.50
TIRO MÉDIO ESTIMADO: 211.46 m
D.V: 5.11 %

CROQUI DE ACESSO

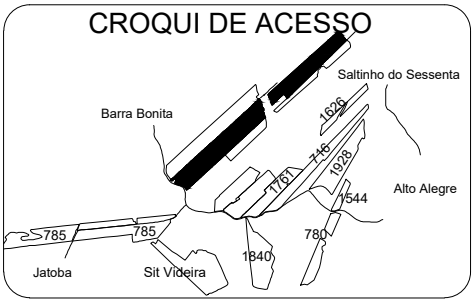

SÍTIO MOLINA

PROPRIETÁRIO: CESAR HENRIQUE ESPERANCIN CRUZ
COMPRADOR: CLEALCO
MUNICÍPIO: LUIZIÂNIA - SP

DISTÂNCIAS (km):
UNID. I - Asfalto: 24.80 Terra.: 8.00
UNID.I I - Asfalto: 37.90 Terra.: 8.00

COORDENADAS: E(X): 582694.80 N(Y): 7614845.80
LAT: -21°34'2.5377" LONG: -50°12'4.5885"

CLEALCO - AÇÚCAR E ALCOOL S/A - DEPARTAMENTO DE GEOTECNOLOGIA

LEVANTAMENTO VIA:
- SATÉLITE
- GPS / VANT
- GOOGLE

UNIDADE: I
PARTE: A/A
FUNDO AGRÍCOLA: 306458

M:\01-Mapa de safra\Mapas Atualizados\Terceiro\306458 - Sítio Molina (Cesar Henrique Esperancin Cruz)\306458 - Sítio Molina (Cesar Henrique Esperancin Cruz).dwg

Bruno Gamboa 09/03/26