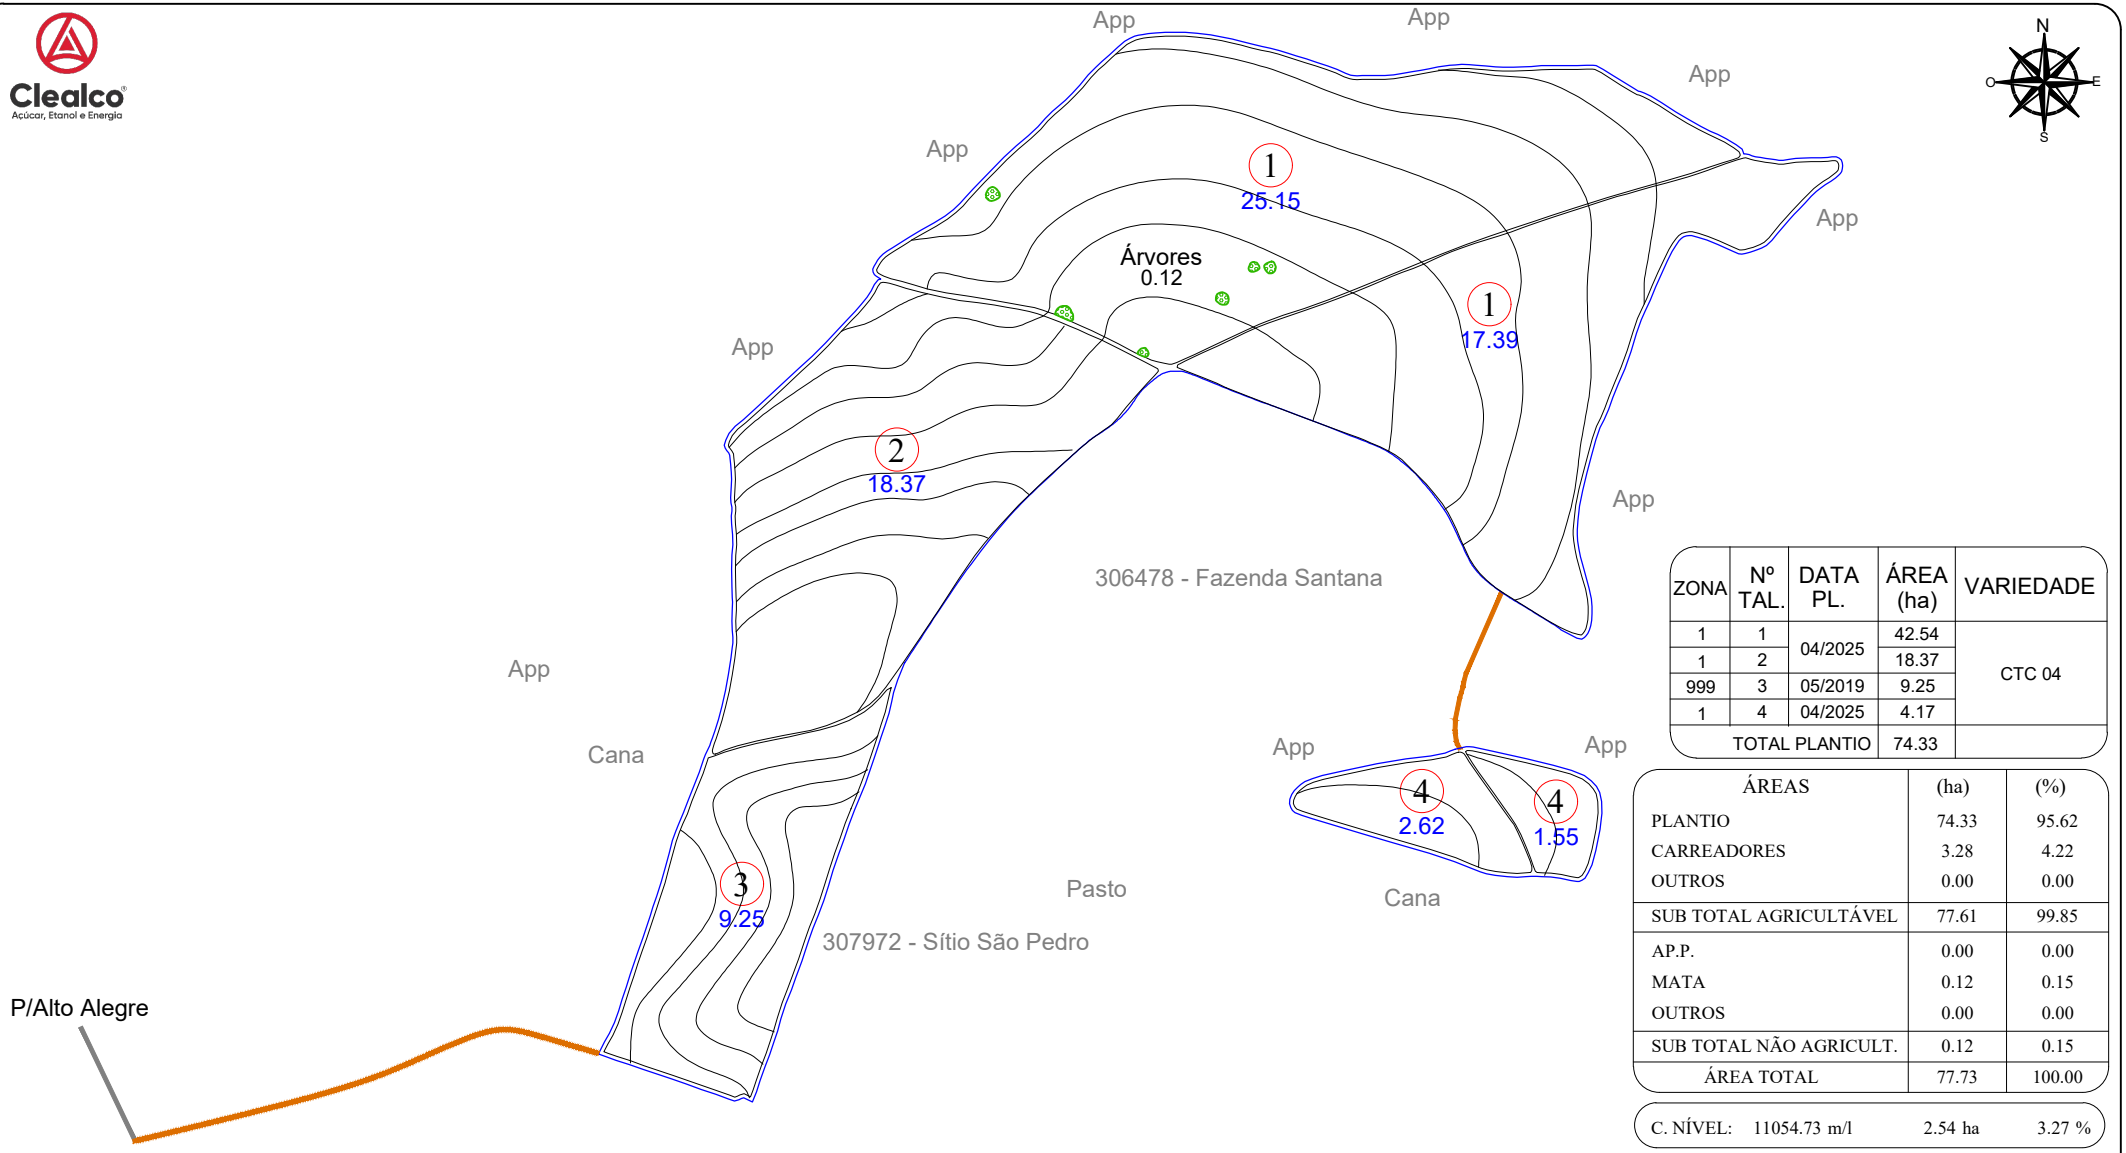


ZONA	Nº TAL.	DATA PL.	ÁREA (ha)	VARIEDADE
1	1	04/2025	42.54	CTC 04
1	2		18.37	
999	3	05/2019	9.25	
1	4	04/2025	4.17	
TOTAL PLANTIO			74.33	

ÁREAS	(ha)	(%)
PLANTIO	74.33	95.62
CARREADORES	3.28	4.22
OUTROS	0.00	0.00
SUB TOTAL AGRICULTÁVEL	77.61	99.85
AP.P.	0.00	0.00
MATA	0.12	0.15
OUTROS	0.00	0.00
SUB TOTAL NÃO AGRICULT.	0.12	0.15
ÁREA TOTAL	77.73	100.00

C. NÍVEL: 11054.73 m/l 2.54 ha 3.27 %


ESCALA: 1: 0.000

LEGENDA

- FAZENDA
- TALHÃO
- REDE ELÉTRICA
- TERRAÇO BASE LARGA
- TERRAÇO EMBUTIDO

ESPAÇAMENTO: 1.50 x 1.50
TIRO MÉDIO ESTIMADO: 274.97 m
D.V: 0.00 %

CROQUI DE ACESSO

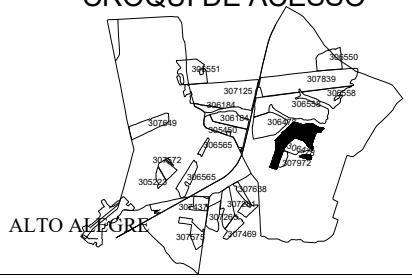

FAZENDA SANTANA

PROPRIETÁRIO: ROSIMARA R. V. DE ANDRADE
COMPRADOR: CLEALCO
MUNICÍPIO: ALTO ALEGRE - SP

DISTÂNCIAS (km):
UNID. I - Asfalto: 51.60 Terra.: 1.70
UNID.I I - Asfalto: 46.50 Terra.: 1.70

COORDENADAS: E(X): 591499.44 N(Y): 7615297.20
LAT: -21°33'46.3115" LONG: -50°6'58.5546"
CLEALCO - AÇÚCAR E ALCOOL S/A - DEPARTAMENTO DE GEOTECNOLOGIA

LEVANTAMENTO VIA:
SATÉLITE
GPS / VANT
GOOGLE

UNIDADE: II
PARTE: A/A
FUNDO AGRÍCOLA: 306477

M:\01-Mapa de safra\Mapas Atualizados\Terceiro\306477 - Fazenda Santana (Rosimara R. V. de Andrade)\306477 - Fazenda Santana (Rosimara R. V. de Andrade).dwg

Bruno Gamboa 12/12/25