ZONA D.V.	Nº TAL.	DATA PL.	ÁREA (ha)	VARIEDADE
999	1	04/2019	34.09	CTC 04
TOTAL PLANTIO			34.09	--------

ÁREAS	(ha)	(%)
PLANTIO	34.09	93.69
CARREADORES	2.15	5.90
OUTROS	0.00	0.00
SUB TOTAL AGRICULTÁVEL	36.24	99.59
AP.P.	0.00	0.00
ÁRVORES	0.15	0.41
OUTROS	0.00	0.00
SUB TOTAL NÃO AGRICULT.	0.15	0.41
ÁREA TOTAL	36.39	100.00

C. NÍVEL:	4030.12 m/l	0.93 ha	2.55 %

LEGENDA

FAZENDA	CONFRONTANTE
TALHÃO	REDE ELÉTRICA
CURVA DE NÍVEL	TRAJETO VAZIO
CARREADOR	TRAJETO CARREGADO

PLANTIO MANUAL - ESPAÇAMENTO: 1.50 X 1.50
TIRO MÉDIO ESTIMADO: 000.00 m

Clealco®
Açúcar, Etanol e Energia

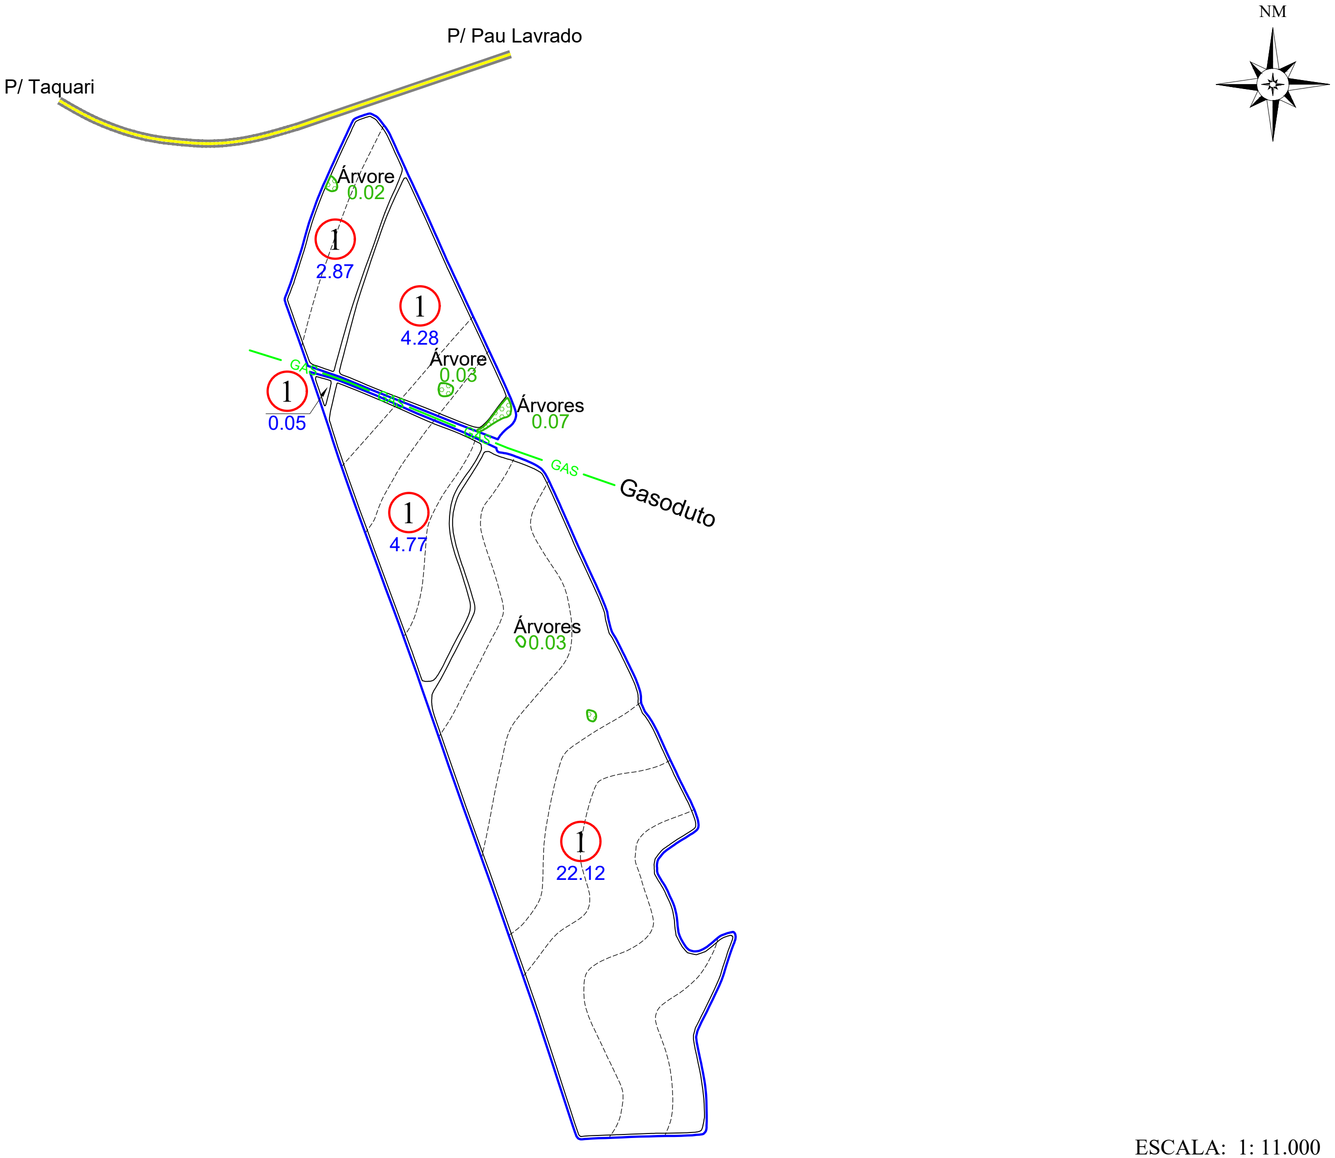

ESCALA: 1: 11.000

CROQUI DE ACESSO

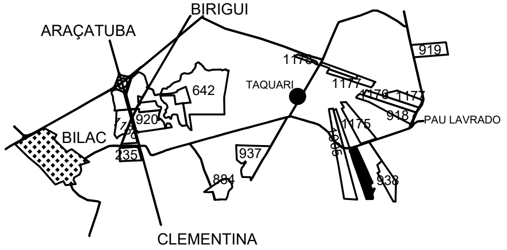

SÍTIO PALMEIRAS

PROPRIETÁRIO:	JORGE LUIZ ZAGO	DISTÂNCIAS (km):			
		UNID. I - Asfalto:	30.50	Terra.:	0.10
COMPRADOR:	CLEALCO S/A	UNID.I I - Asfalto:	85.50	Terra.:	0.10
MUNICÍPIO:	BIRIGUI	UNID. III -Asfalto:	40.00	Terra.:	0.10

COORDENADAS:	E(X):	562794.05	N(Y):	7633303.54
	LAT:	-21°24'5.1240"	LONG:	-50°23'39.0161"

CLEALCO - AÇÚCAR E ALCOOL S/A - DEPARTAMENTO DE TOPOGRAFIA

UNIDADE:
I

PARTE:
A/A

FUNDO AGRÍCOLA:
306489

M:\01-Mapa de safra\Mapas Atualizados\Terceiro\306489 - Sítio Palmeiras (Jorge Luiz Zago)\306489 - Sítio Palmeiras (Jorge Luiz Zago).dwg

Fernanda Bezerra 17/05/24