
Clealco
Açúcar, Etanol e Energia

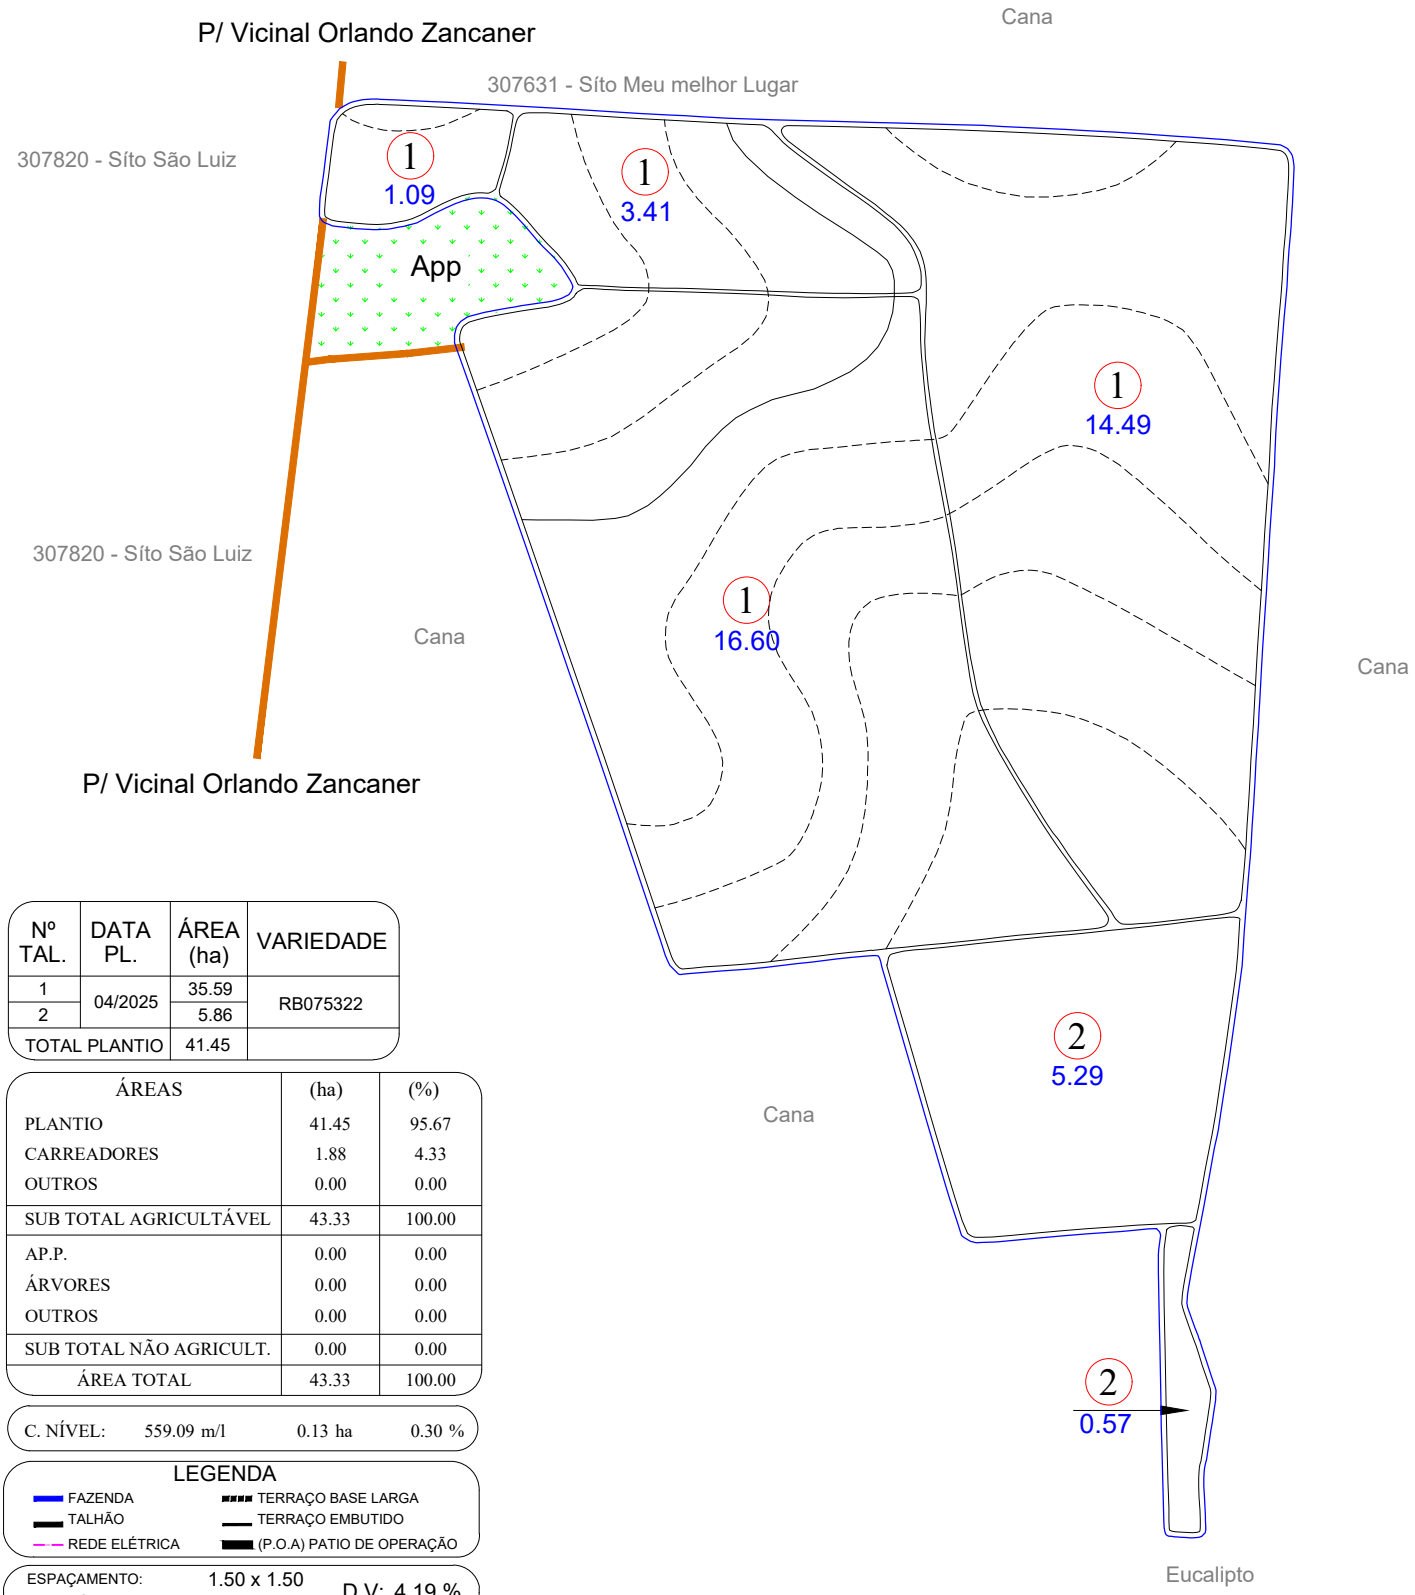

Nº TAL.	DATA PL.	ÁREA (ha)	VARIEDADE
1	04/2025	35.59	RB075322
2		5.86	
TOTAL PLANTIO		41.45	

ÁREAS	(ha)	(%)
PLANTIO	41.45	95.67
CARREADORES	1.88	4.33
OUTROS	0.00	0.00
SUB TOTAL AGRICULTÁVEL	43.33	100.00
AP.P.	0.00	0.00
ÁRVORES	0.00	0.00
OUTROS	0.00	0.00
SUB TOTAL NÃO AGRICULT.	0.00	0.00
ÁREA TOTAL	43.33	100.00

C. NÍVEL: 559.09 m/l 0.13 ha 0.30 %


LEGENDA

- FAZENDA
- TALHÃO
- REDE ELÉTRICA
- TERRAÇO BASE LARGA
- TERRAÇO EMBUTIDO
- (P.O.A) PATIO DE OPERAÇÃO

ESPAÇAMENTO: 1.50 x 1.50
TIRO MÉDIO ESTIMADO: 220.46 m
D.V: 4.19 %

ESCALA: 1: 6.000

CROQUI DE ACESSO

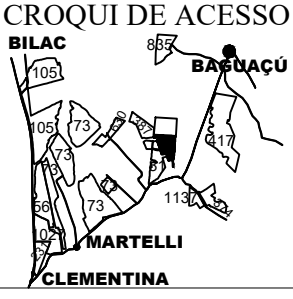

SÍTIO SÃO BENTO

PROPRIETÁRIO: JORGE LUIZ ZAGO
COMPRADOR: CLEALCO
MUNICÍPIO: COROADOS - SP

DISTÂNCIAS (km):
UNID. I - Asfalto: 17.90 Terra.: 1.10
UNID.I I - Asfalto: 68.50 Terra.: 1.10

COORDENADAS: E(X): 563607.13 N(Y): 7624367.13
LAT: -21°28'55.6759" LONG: -50°23'9.5615"

CLEALCO - AÇÚCAR E ALCOOL S/A - DEPARTAMENTO DE GEOTECNOLOGIA

LEVANTAMENTO VIA:
SATÉLITE
GPS / VANT
GOOGLE

UNIDADE: I
PARTE: A/A
FUNDO AGRÍCOLA: 306490

M:\01-Mapa de safra\Mapas Atualizados\Terceiro\306490 - Sítio São Bento (Jorge Luiz Zago)\306490 - Sítio São Bento (Jorge Luiz Zago).dwg

Fabiano Castro 28/01/2026