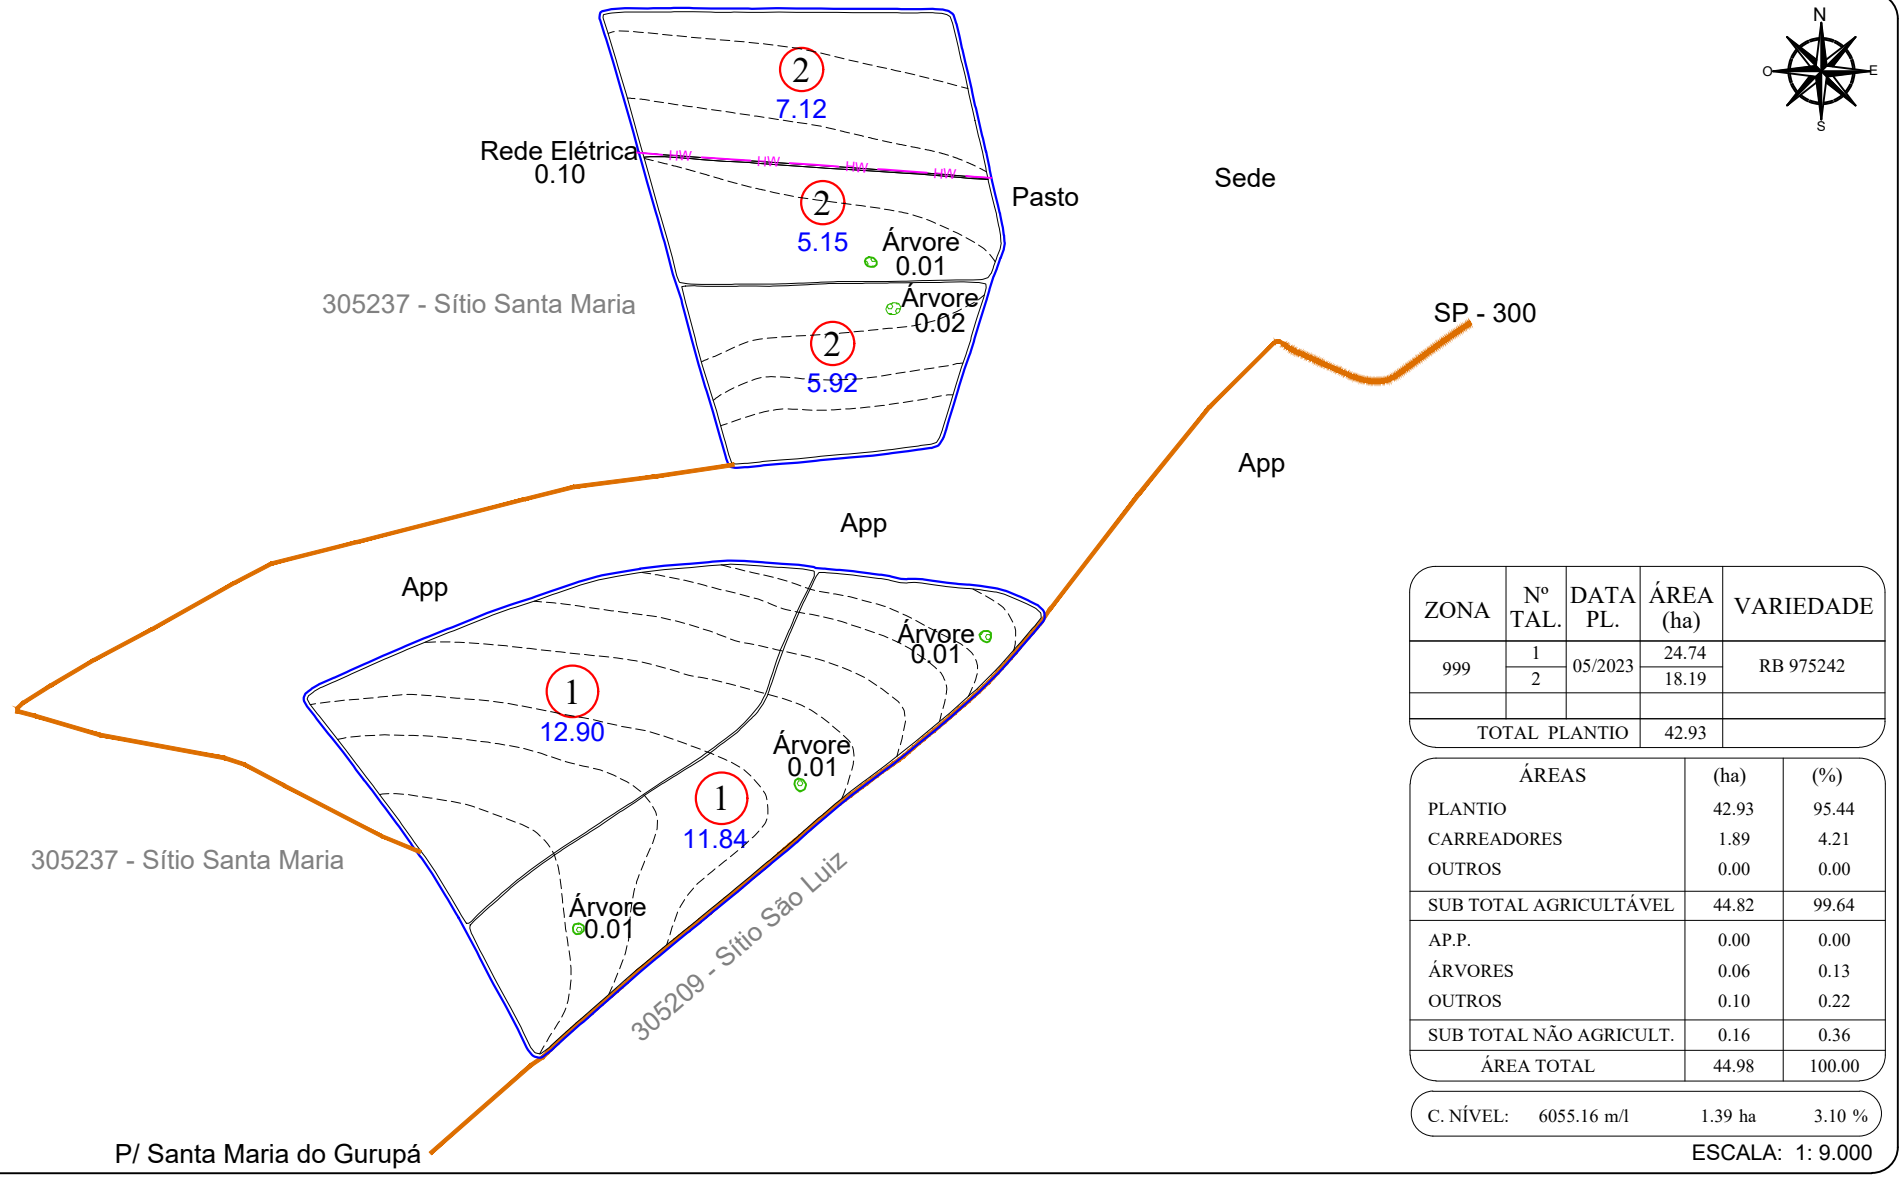


ZONA	Nº TAL.	DATA PL.	ÁREA (ha)	VARIEDADE
999	1	05/2023	24.74	RB 975242
	2		18.19	
TOTAL PLANTIO			42.93	

ÁREAS	(ha)	(%)
PLANTIO	42.93	95.44
CARREADORES	1.89	4.21
OUTROS	0.00	0.00
SUB TOTAL AGRICULTÁVEL	44.82	99.64
AP.P.	0.00	0.00
ÁRVORES	0.06	0.13
OUTROS	0.10	0.22
SUB TOTAL NÃO AGRICULT.	0.16	0.36
ÁREA TOTAL	44.98	100.00

C. NÍVEL: 6055.16 m/l 1.39 ha 3.10 %


ESCALA: 1: 9.000

LEGENDA

- FAZENDA
- TALHÃO
- REDE ELÉTRICA
- TERRAÇO BASE LARGA
- TERRAÇO EMBUTIDO

ESPAÇAMENTO: 1.50 x 1.50
TIRO MÉDIO ESTIMADO: 293.38 m
D.V: 6.85 %

CROQUI DE ACESSO

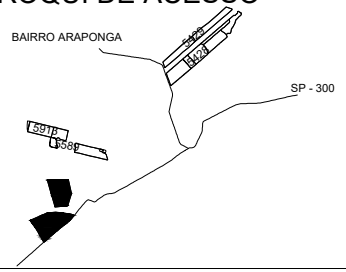

SÍTIO SÃO PEDRO

PROPRIETÁRIO: JOSÉ CARLOS D. GILBERTO
COMPRADOR: CLEALCO
MUNICÍPIO: AVANHANDAVA - SP

DISTÂNCIAS (km):
UNID. I - Asfalto: 49.20 Terra.: 17.00
UNID.I I - Asfalto: 49.00 Terra.: 17.00

COORDENADAS: E(X): 598484.23 N(Y): 7610807.36
LAT: -21°36'10.9912" LONG: -50°2'54.7635"

CLEALCO - AÇÚCAR E ALCOOL S/A - DEPARTAMENTO DE GEOTECNOLOGIA

LEVANTAMENTO VIA:
SATÉLITE
GPS / VANT
GOOGLE

UNIDADE: II
PARTE: A/A
FUNDO AGRÍCOLA: 306512

M:\01-Mapa de safra\Mapas Atualizados\Terceiro\306512 - Sítio São Pedro (José Carlos Donisete Gilberto\306512 - Sítio São Pedro (José Carlos Donisete Gilberto.dwg

Bruno Gamboa 24/07/25