
Clealco
Açúcar, Etanol e Energia

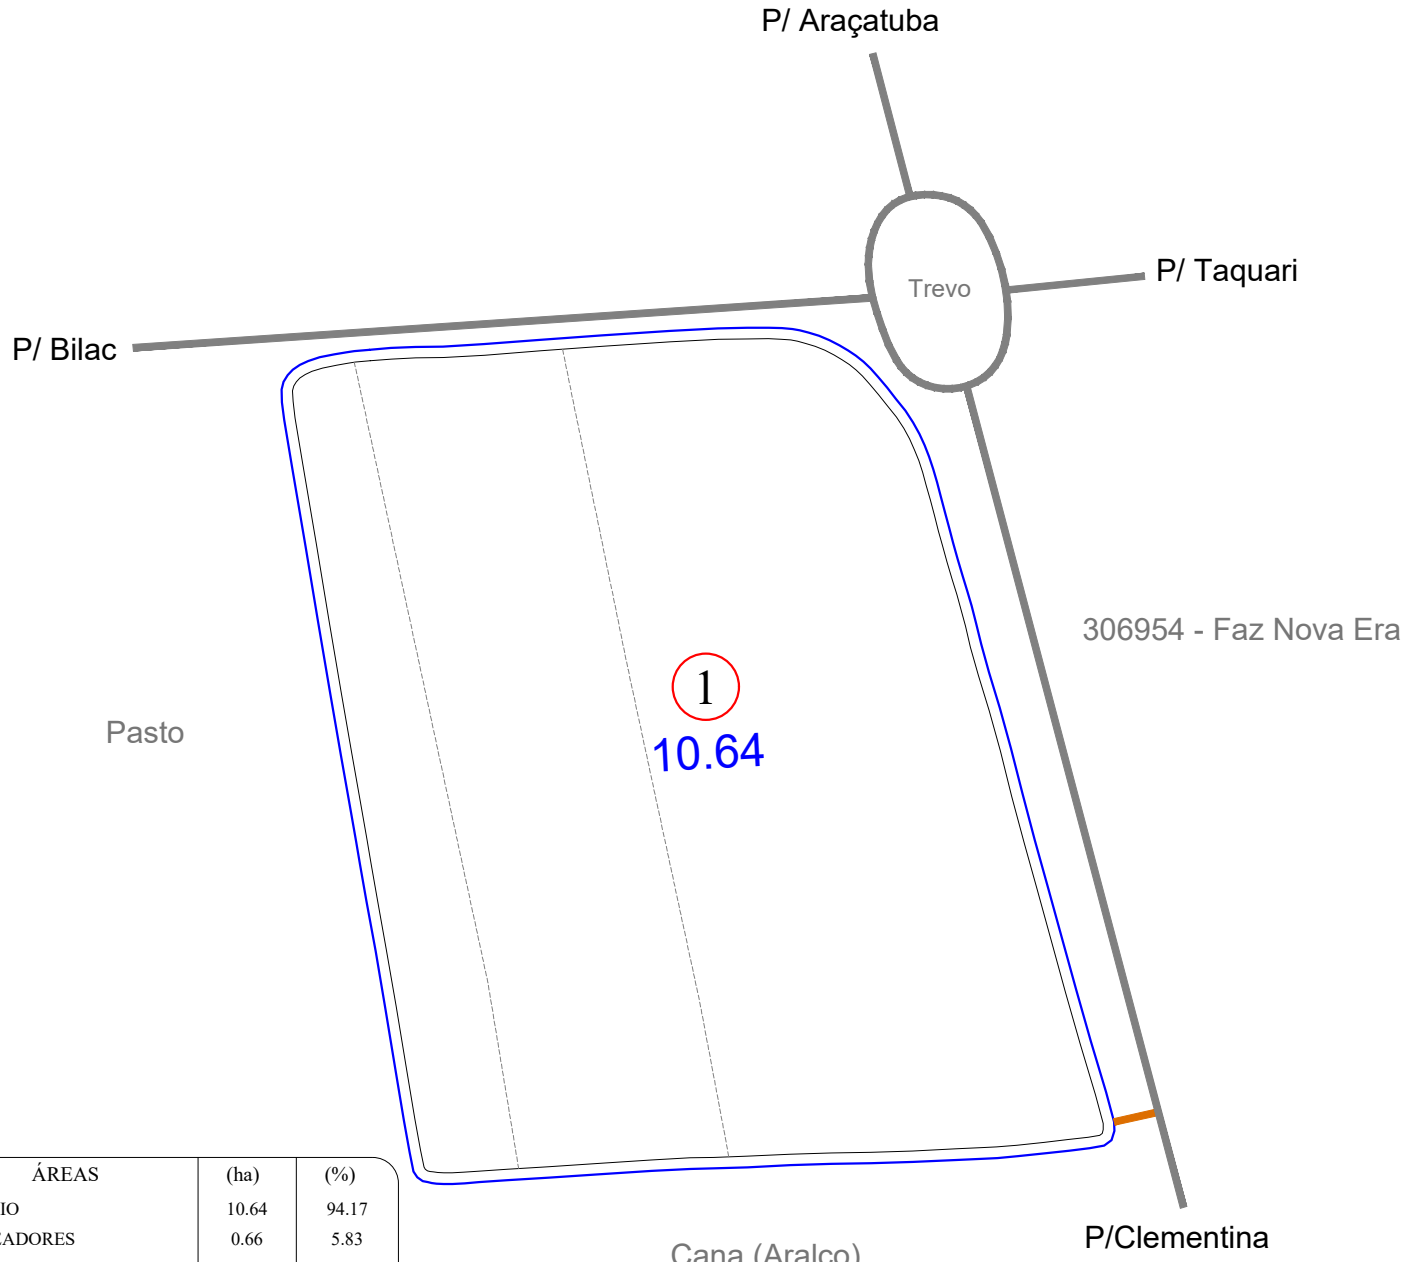

ÁREAS	(ha)	(%)
PLANTIO	10.64	94.17
CARREADORES	0.66	5.83
OUTROS	0.00	0.00
SUB TOTAL AGRICULTÁVEL	11.30	100.00
AP.P.	0.00	0.00
ÁRVORES	0.00	0.00
OUTROS	0.00	0.00
SUB TOTAL NÃO AGRICULT.	0.00	0.00
ÁREA TOTAL	11.30	100.00

C. NÍVEL: 0.00 m/l 0.00 ha 0.00 %

LEGENDA


- FAZENDA
- TALHÃO
- REDE ELÉTRICA
- TERRAÇO BASE LARGA
- TERRAÇO EMBUTIDO
- (P.O.A) PATIO DE OPERAÇÃO

ESPAÇAMENTO: 1.50 x 1.50
TIRO MÉDIO ESTIMADO: 348.68 m
D.V: 1.43 %

Nº TAL.	DATA PL.	ÁREA (ha)	VARIEDADE
1	04/2024	10.64	RB86 7515
TOTAL PLANTIO		10.64	

ESCALA: 1: 3.500

CROQUI DE ACESSO

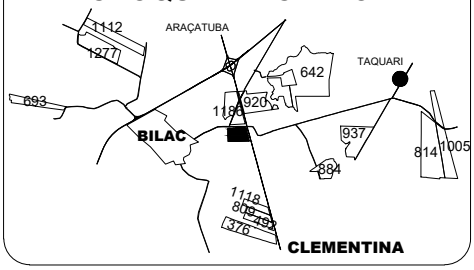

SÍTIO PESSOA

PROPRIETÁRIO: PAULO BENTO BOGO
COMPRADOR: CLEALCO
MUNICÍPIO: BILAC - SP

DISTÂNCIAS (km):
UNID. I - Asfalto: 22.70 Terra.: 0.10
UNID.I I - Asfalto: 79.00 Terra.: 0.10

COORDENADAS: E(X): 556593.90 N(Y): 7633331.10
LAT: -21°24'4.9673" LONG: -50°27'14.3575"

CLEALCO - AÇÚCAR E ALCOOL S/A - DEPARTAMENTO DE GEOTECNOLOGIA

LEVANTAMENTO VIA:
- SATÉLITE
- GPS / VANT
- GOOGLE

UNIDADE: I
PARTE: A/A
FUNDO AGRÍCOLA: 306513

M:\01-Mapa de safra\Mapas Atualizados\Terceiro\306513 - Sítio Pessoa (Paulo Bento Bogo)\306513 - Sítio Pessoa (Paulo Bento Bogo).dwg

Peterson Santos 25/03/25