ZONA DV	CLA	Nº TAL.	DATA PL.	ÁREA (ha)	VAR.
999 5.35 %	SR	1	05/2020	43.54	RB 975201
TOTAL PLANTIO				43.54	--------


ÁREAS	(ha)	(%)
PLANTIO	43.54	95.07
CARREADORES	2.26	4.93
OUTROS	0.00	0.00
SUB TOTAL AGRICULTÁVEL	45.80	---------
VÁRZEA	0.00	0.00
MATA	0.02	0.04
OUTROS	0.18	0.39
SUB TOTAL NÃO AGRICULT.	0.20	0.43
ÁREA TOTAL	46.00	---------

C. NÍVEL: 7215.10 m/l 1.66 ha 3.81 %


LEGENDA

- FAZENDA
- TALHÃO
- CURVA DE NÍVEL
- CARREADOR
- CONFRONTANTE
- REDE ELÉTRICA
- TRAJETO VAZIO
- TRAJETO CARREGADO

PLANTIO MANUAL - ESPAÇAMENTO: 1.50 X 1.50

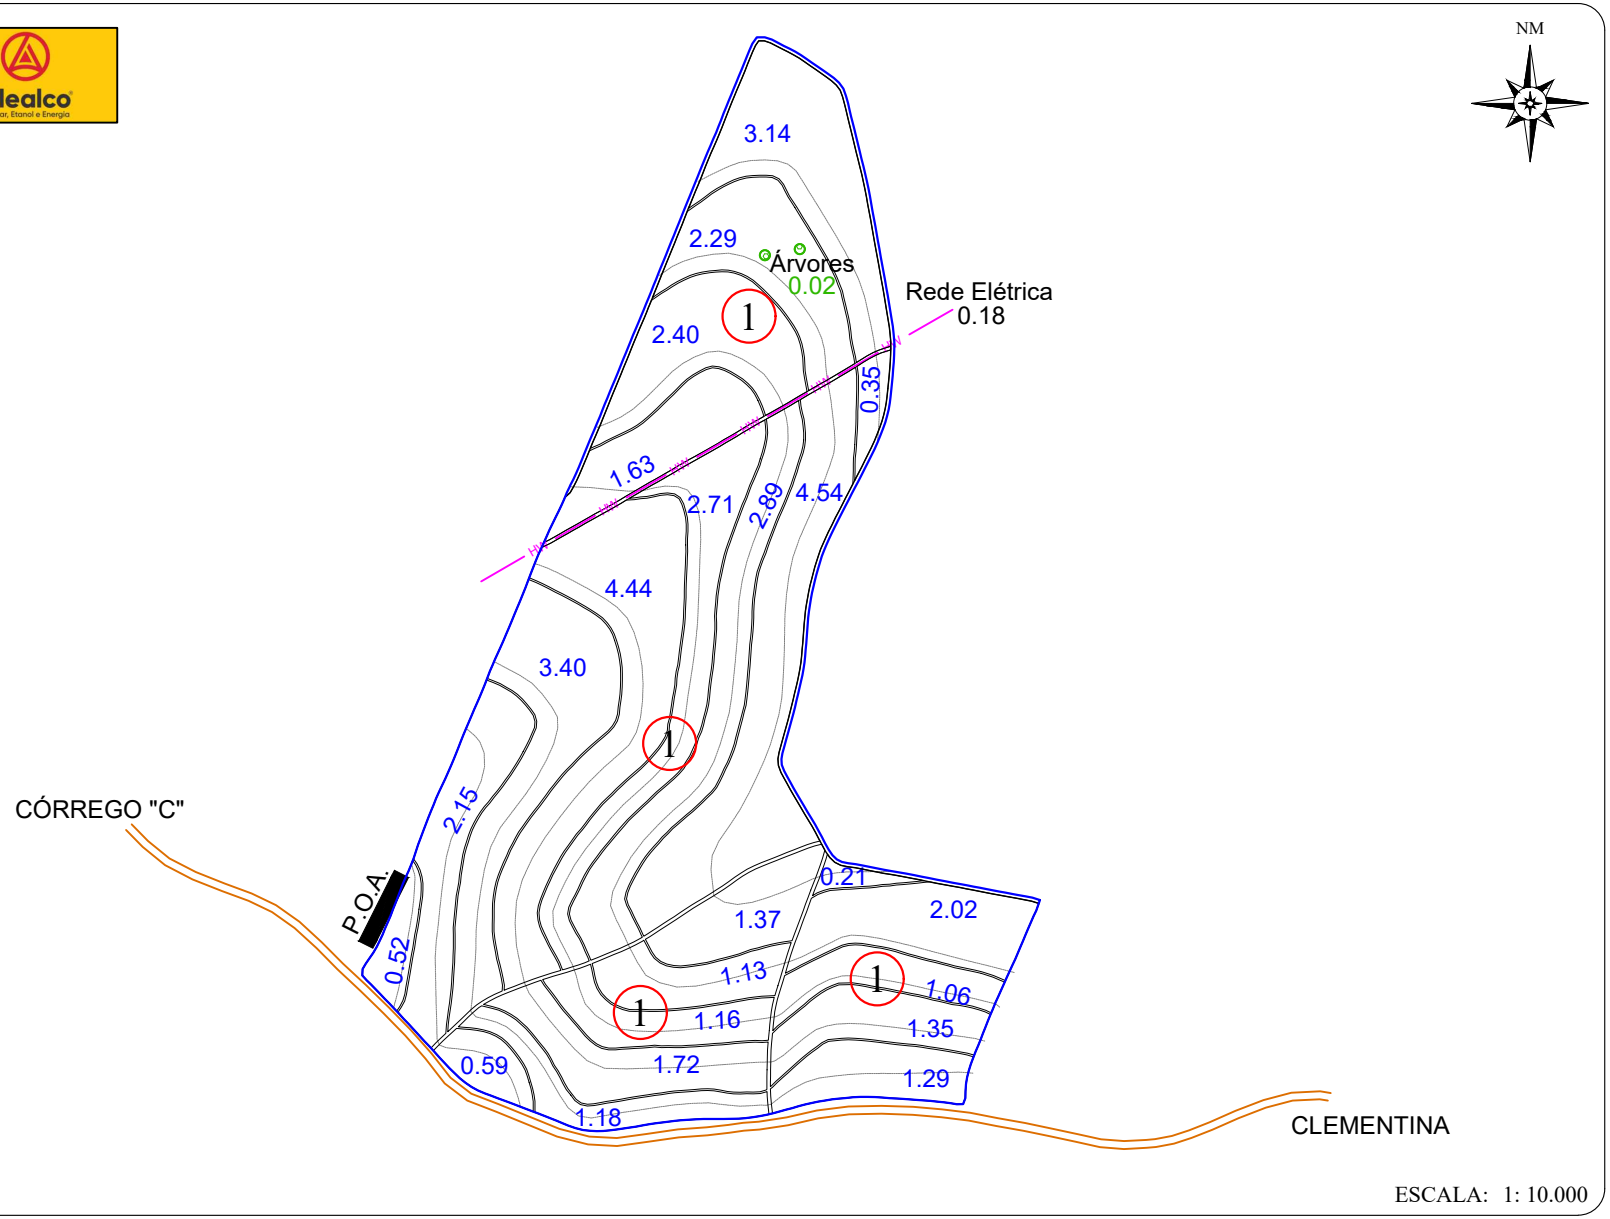

CROQUI DE ACESSO

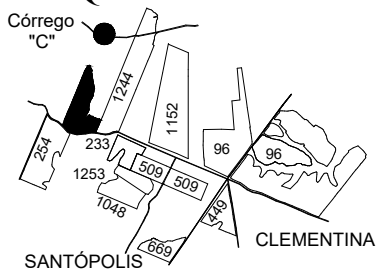

SÍTIO SÃO JOÃO II

PROPRIETÁRIO: FERNANDO COSTA GARRUTTI
COMPRADOR: CLEALCO S/A
MUNICÍPIO: CLEMENTINA

DISTÂNCIAS (km):
UNID. I - Asfalto: 5.50 Terra.: 3.70
UNID.I I - Asfalto: 51.80 Terra.: 3.70
UNID. III -Asfalto: 48.00 Terra.: 3.70

COORDENADAS: E(X): 552217.3165 N(Y): 7612865.7484
LAT: 21° 35' 11,08231" LONG: 50° 29' 44,06918"

CLEALCO - AÇÚCAR E ALCOOL S/A - DEPARTAMENTO DE TOPOGRAFIA

UNIDADE: I
PARTE: A/A
FUNDO AGRÍCOLA: 306523