

Clealco
Açúcar, Etanol e Energia

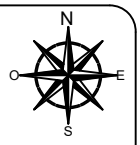

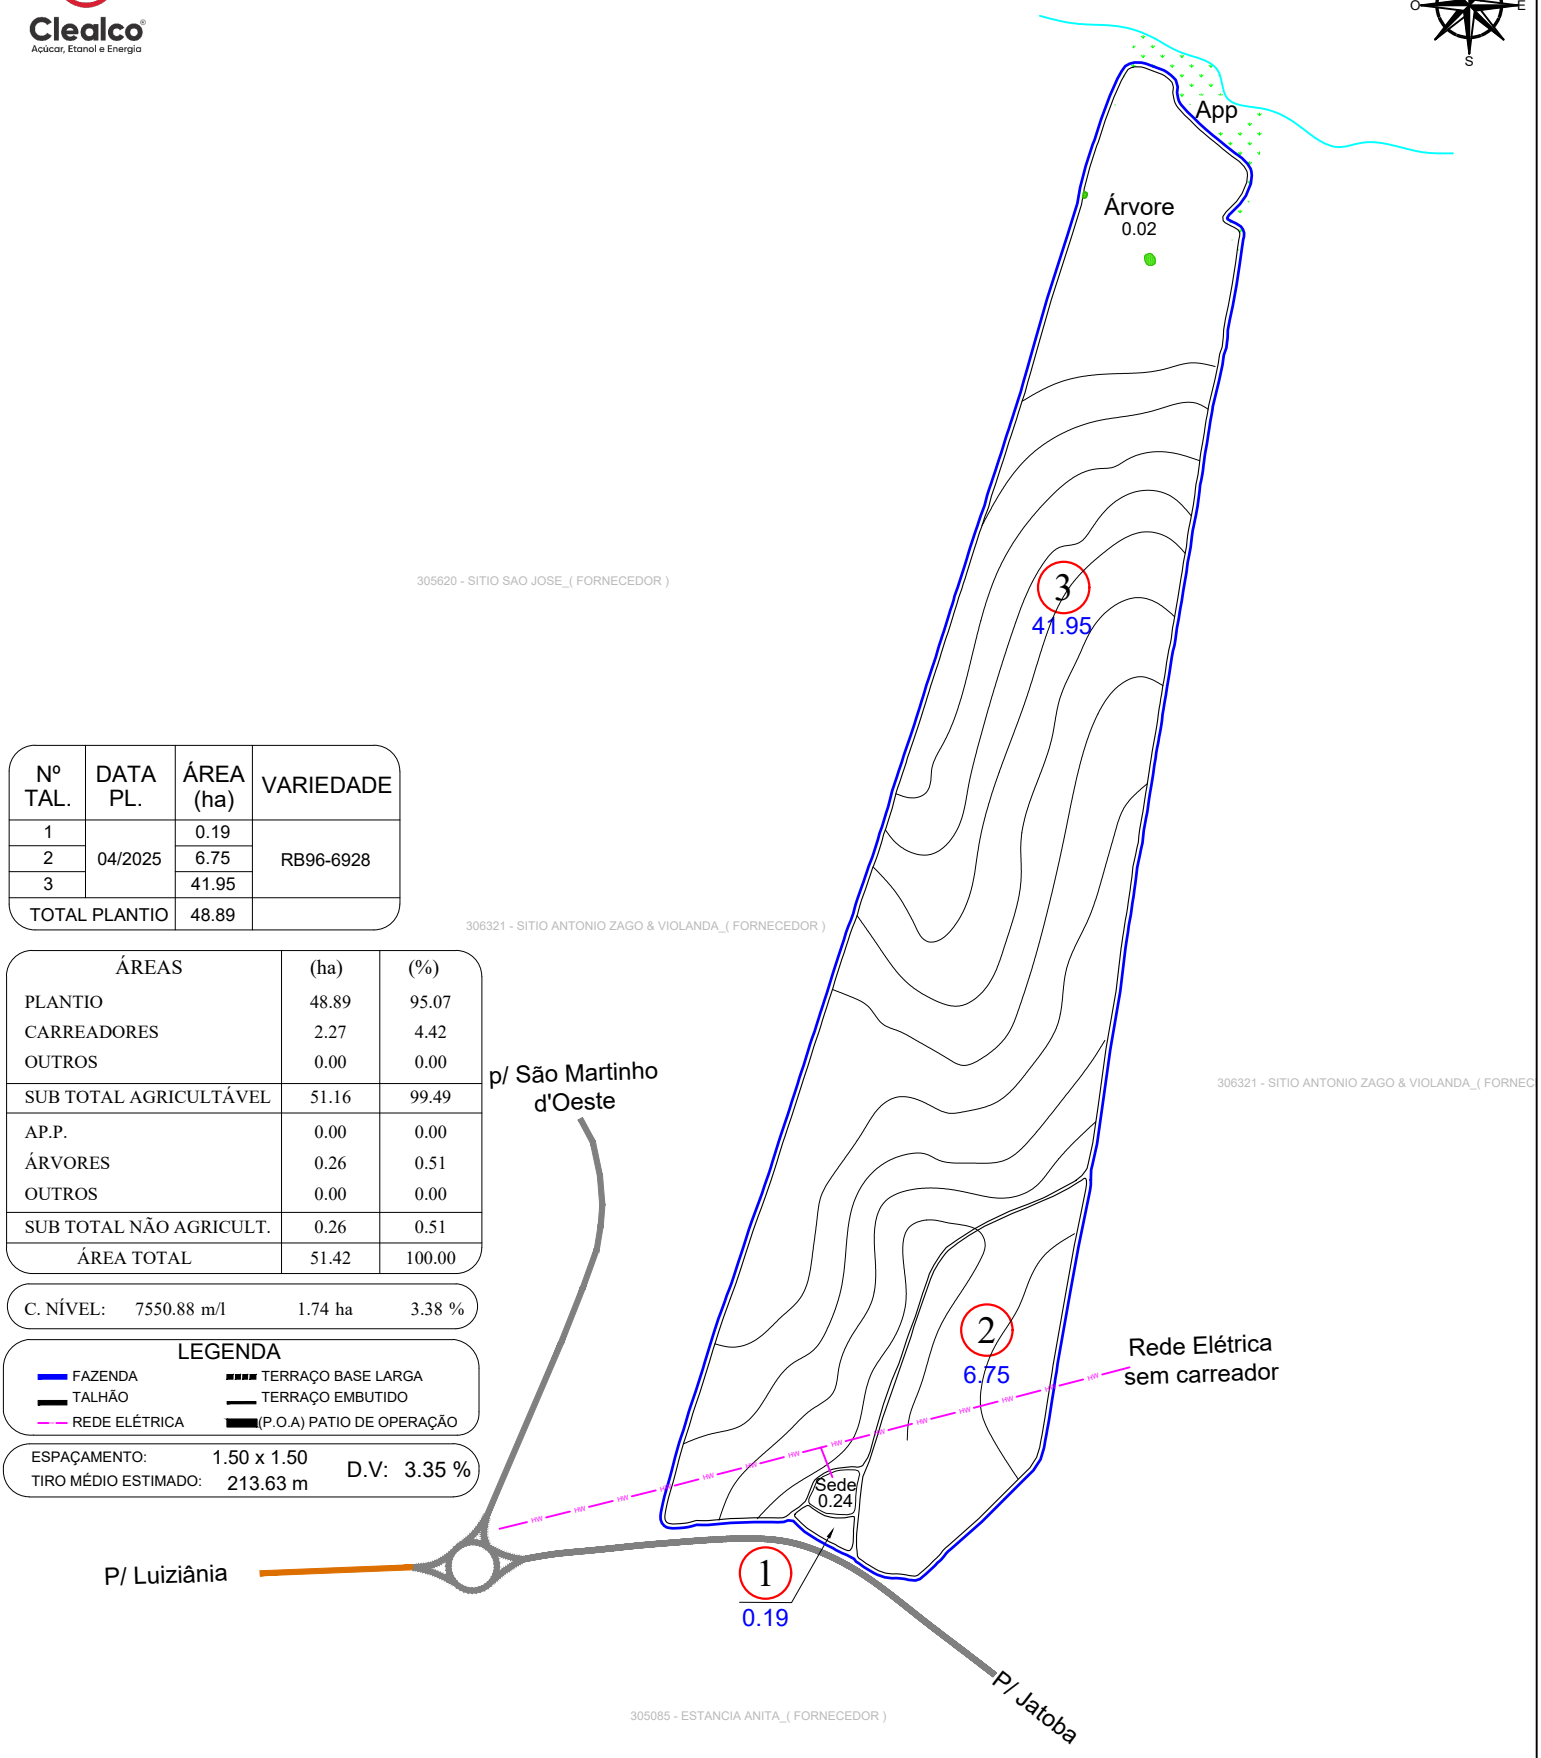

Nº TAL.	DATA PL.	ÁREA (ha)	VARIEDADE
1	04/2025	0.19	RB96-6928
2		6.75	
3		41.95	
TOTAL PLANTIO		48.89	

ÁREAS	(ha)	(%)
PLANTIO	48.89	95.07
CARREADORES	2.27	4.42
OUTROS	0.00	0.00
SUB TOTAL AGRICULTÁVEL	51.16	99.49
AP.P.	0.00	0.00
ÁRVORES	0.26	0.51
OUTROS	0.00	0.00
SUB TOTAL NÃO AGRICULT.	0.26	0.51
ÁREA TOTAL	51.42	100.00

C. NÍVEL: 7550.88 m/l 1.74 ha 3.38 %


LEGENDA

- FAZENDA
- TALHÃO
- REDE ELÉTRICA
- TERRAÇO BASE LARGA
- TERRAÇO EMBUTIDO
- (P.O.A) PATIO DE OPERAÇÃO

ESPAÇAMENTO: 1.50 x 1.50
TIRO MÉDIO ESTIMADO: 213.63 m
D.V: 3.35 %

ESCALA: 1: 9.000

CROQUI DE ACESSO

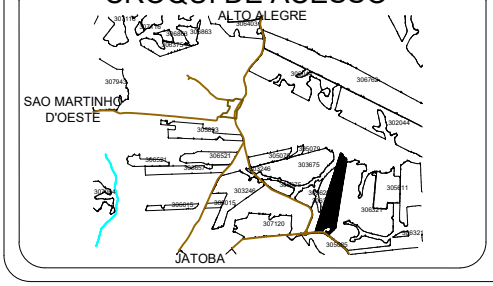

SÍTIO SÃO MARTINHO

PROPRIETÁRIO: WALDEMIR A. CAPUTO
COMPRADOR: CLEALCO
MUNICÍPIO: ALTO ALEGRE - SP

DISTÂNCIAS (km):
UNID. I - Asfalto: 45.50 Terra.: 1.00
UNID.I I - Asfalto: 34.50 Terra.: 1.00

COORDENADAS: E(X): 577266.55 N(Y): 7612110.74
LAT: -21°35'32.3659" LONG: -50°15'12.8680"

CLEALCO - AÇÚCAR E ALCOOL S/A - DEPARTAMENTO DE GEOTECNOLOGIA

LEVANTAMENTO VIA:
- SATÉLITE
- GPS / VANT
- GOOGLE

UNIDADE: I
PARTE: A/A
FUNDO AGRÍCOLA: 306539

M:\01-Mapa de safra\Mapas Atualizados\Spot\306539 - Sitio Sao Martinho (Waldemir Aparicio Caputo)\306539 - Sitio Sao Martinho (Waldemir Aparicio Caputo).dwg

Benati 12/09/2025