ZONA D.V.	Nº TAL.	DATA PL.	ÁREA (ha)	VARIEDADE
999	1	05/2023	13.94	RB 975242
6.03 %	2		20.98	
TOTAL PLANTIO			34.92	--------

ÁREAS	(ha)	(%)
PLANTIO	34.92	97.02
CARREADORES	1.05	2.92
OUTROS	0.00	0.00
SUB TOTAL AGRICULTÁVEL	35.97	99.94
AP.P.	0.00	0.00
ÁRVORES	0.02	0.06
OUTROS	0.00	0.00
SUB TOTAL NÃO AGRICULT.	0.02	0.06
ÁREA TOTAL	35.99	100.00

C. NÍVEL:	4487.65 m/l	1.03 ha	2.87 %

LEGENDA

▬ FAZENDA	▬ CONFRONTANTE
▬ TALHÃO	– – REDE ELÉTRICA
▪▪▪ CURVA DE NÍVEL	—▷ TRAJETO VAZIO
— CARREADOR	—► TRAJETO CARREGADO

PLANTIO MANUAL - ESPAÇAMENTO: 1.50 X 1.50
TIRO MÉDIO ESTIMADO: 332.70 m

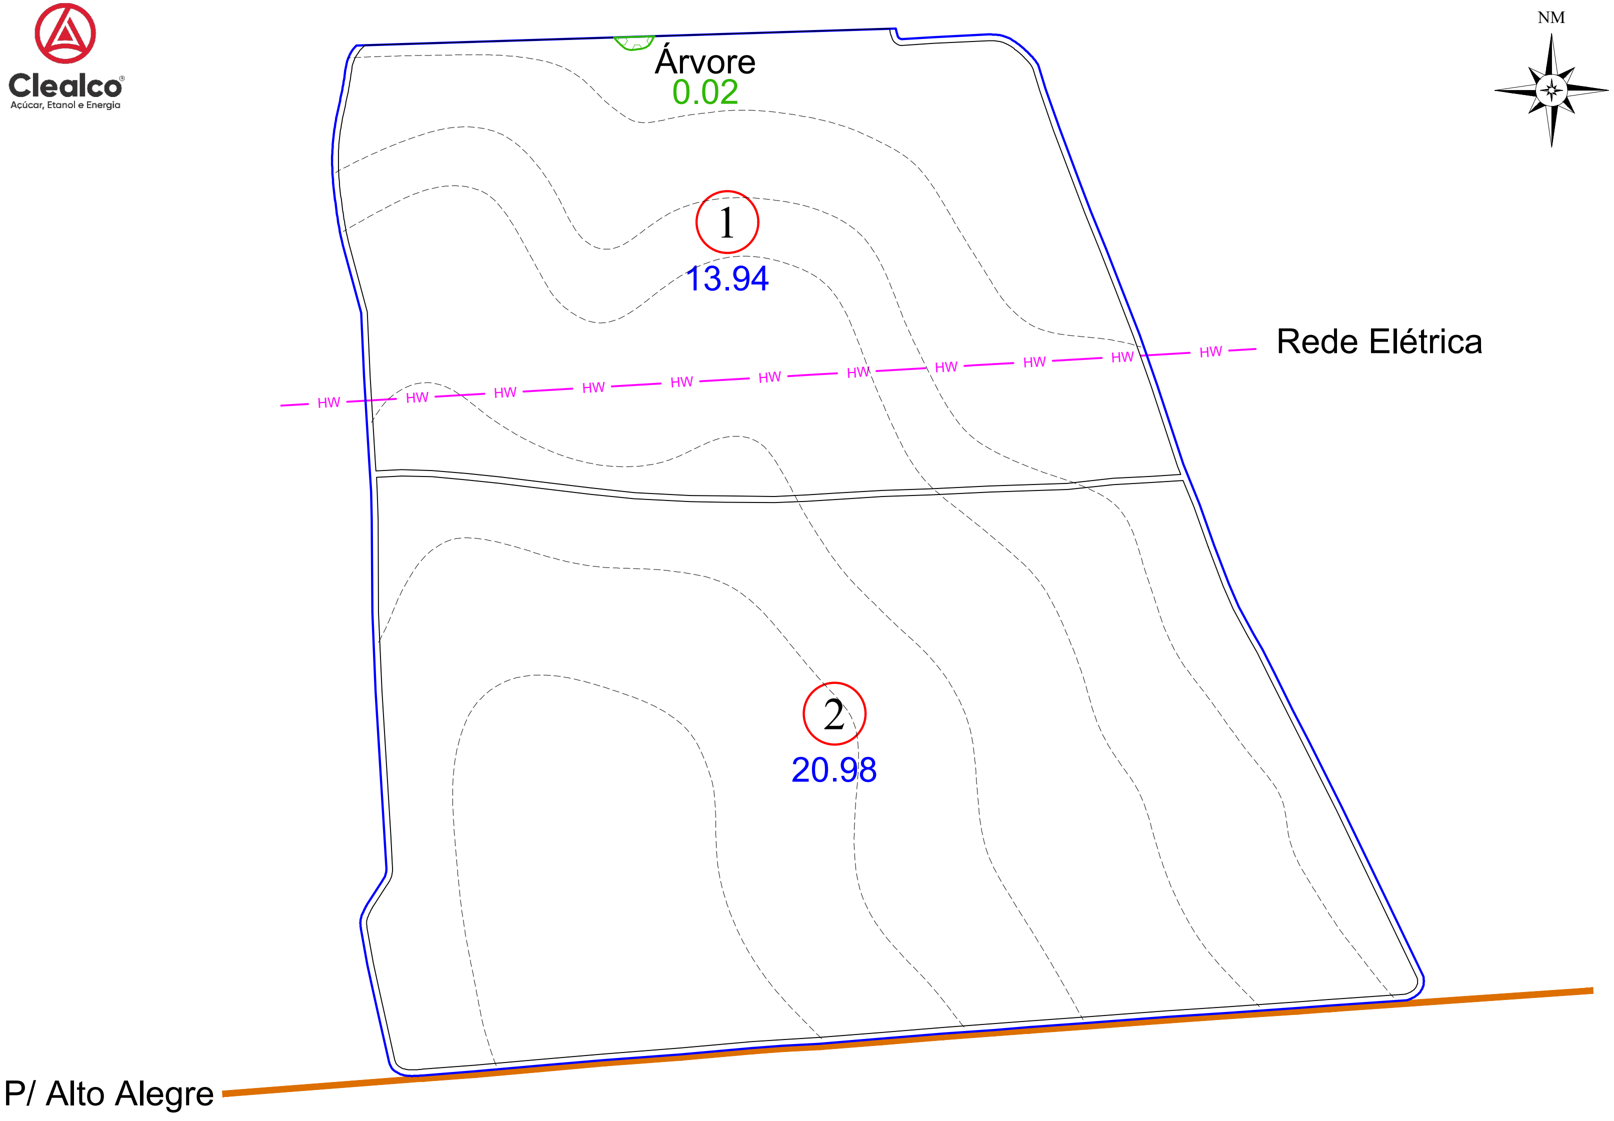
Clealco
Açúcar, Etanol e Energia
NM
Árvore
0.02
1
13.94
Rede Elétrica
HW
2
20.98
P/ Alto Alegre

ESCALA: 1: 5.000

CROQUI DE ACESSO

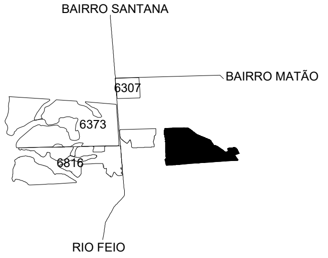
BAIRRO SANTANA
BAIRRO MATÃO
6307
6373
6816
RIO FEIO

FAZENDA SÃO JOÃO

PROPRIETÁRIO: WALDEMIR APARICIO CAPUTO
COMPRADOR: CLEALCO S/A
MUNICÍPIO: ALTO ALEGRE

DISTÂNCIAS (km):

	Asfalto:		Terra.:	
UNID. I -	Asfalto:	48.30	Terra.:	4.50
UNID.I I -	Asfalto:	48.20	Terra.:	4.50
UNID. III -	Asfalto:	13.50	Terra.:	4.50

COORDENADAS: E(X): 591822.05 N(Y): 7607761.22
LAT: -21°37'51.3377" LONG: -50°6'45.8447"

CLEALCO - AÇÚCAR E ALCOOL S/A - DEPARTAMENTO DE TOPOGRAFIA

UNIDADE:
II

PARTE:
A/A

FUNDO AGRÍCOLA:
306545

M:\03-Projetos (Sistematização, Pré, Pós e outros)\Terceiro\2023\Joao\Pós Plantio\306545 - Fazenda Sao Joao (Waldemir Aparicio Caputo) - Pós Plantio 2023.dwg

Bruno Gamboa 20/10/23