D.V.	Nº TAL.	DATA PL.	ÁREA (ha)	VARIEDADE
4.94%	1	04/2024	20.36	CV 7870
	2		21.49	
TOTAL PLANTIO			41.85	

ÁREAS	(ha)	(%)
PLANTIO	41.85	96.81
CARREADORES	1.38	3.19
OUTROS	0.00	0.00
SUB TOTAL AGRICULTÁVEL	43.23	100.00
AP.P.	0.00	0.00
ÁRVORES	0.00	0.00
OUTROS	0.00	0.00
SUB TOTAL NÃO AGRICULT.	0.00	0.00
ÁREA TOTAL	43.23	100.00


C. NÍVEL: 8095.24 m/l 1.86 ha 4.31 %

LEGENDA

- FAZENDA
- TALHÃO
- REDE ELÉTRICA
- TERRAÇO BASE LARGA
- TERRAÇO EMBUTIDO


ESPAÇAMENTO: 1.50 x 1.50

TIRO MÉDIO ESTIMADO: 222.97 m

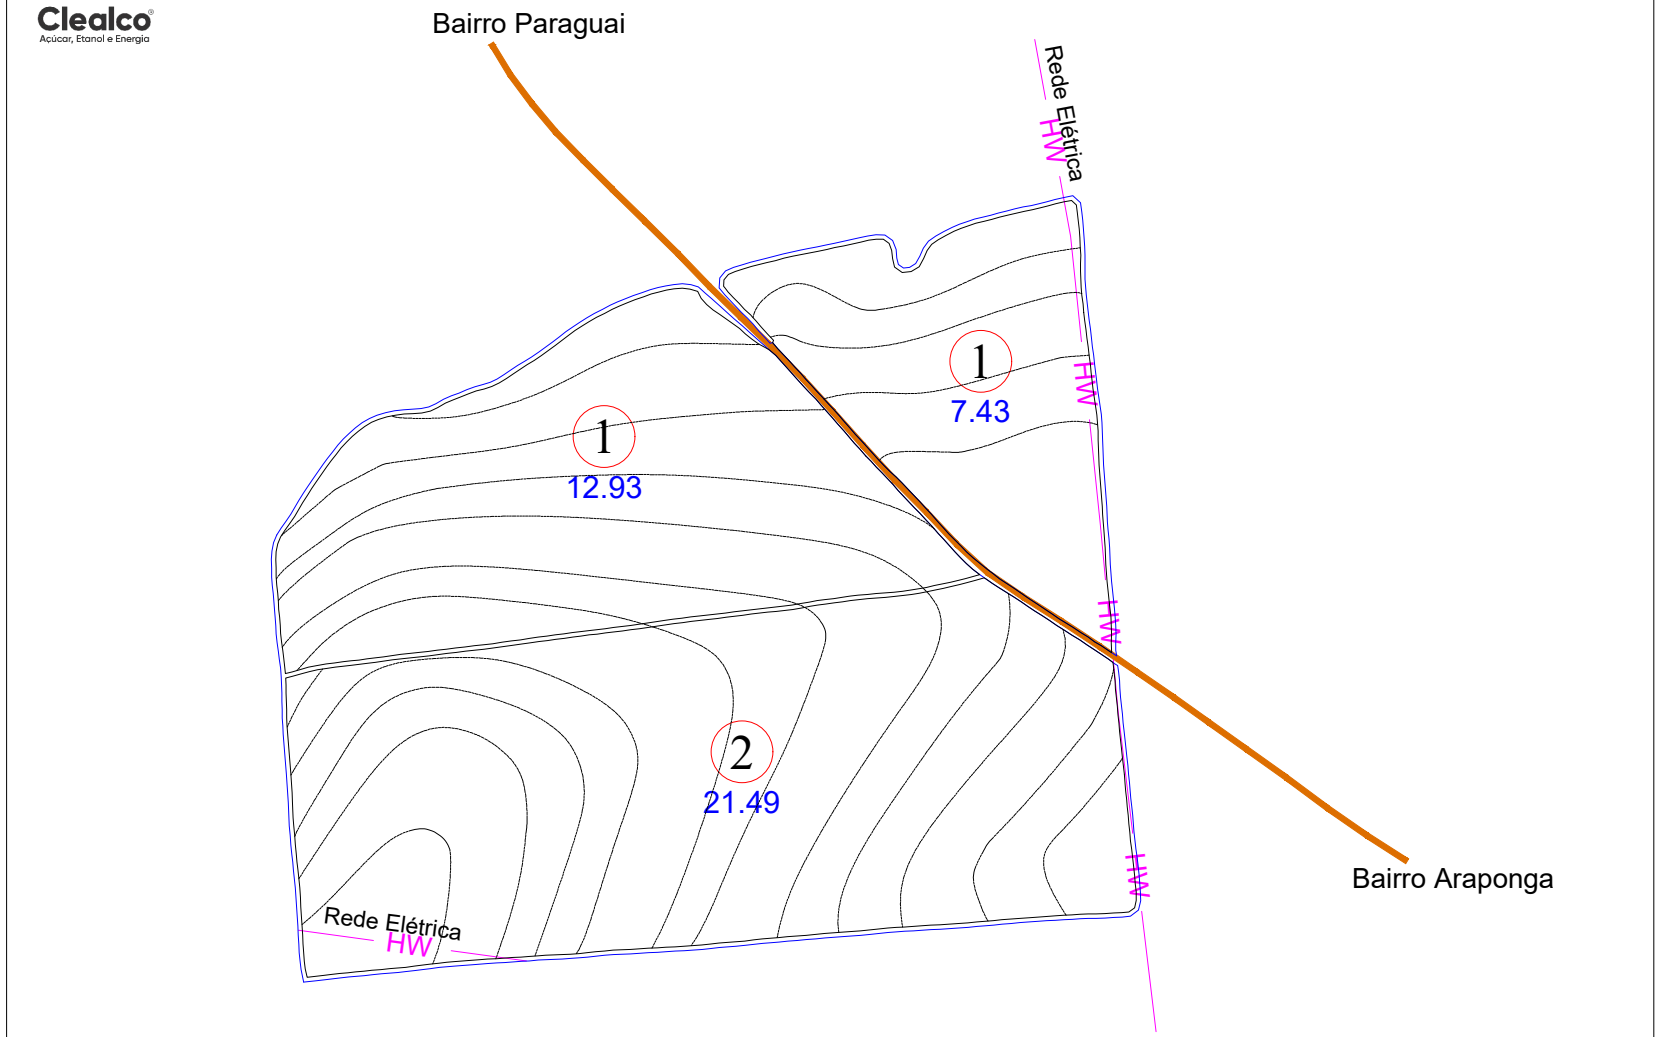

ESCALA: 1: 7.000

CROQUI DE ACESSO

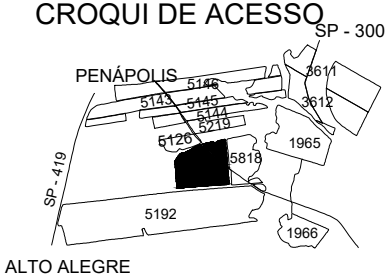

SÍTIO SÃO JOÃO

PROPRIETÁRIO: RAFAEL PONTIN E OUTRO

COMPRADOR: CLEALCO S/A

MUNICÍPIO: PENÁPOLIS

DISTÂNCIAS (km):

UNID. I - Asfalto: 43.30 Terra.: 9.40

UNID.I I - Asfalto: 54.80 Terra.: 9.40

UNID. III -Asfalto: 8.00 Terra.: 1.00

COORDENADAS: E(X): 592913.80 N(Y): 7617848.38

LAT: -21°32'23.0788" LONG: -50°6'9.8919"

CLEALCO - AÇÚCAR E ALCOOL S/A - DEPARTAMENTO DE GEOTECNOLOGIA

UNIDADE: II

PARTE: A/A

FUNDO AGRÍCOLA: 306550

M:\01-Mapa de safra\Mapas Atualizados\Terceiro\306550 - Sítio São João (José Luis Pontin e Familia)\306550 - Sítio São João (José Luis Pontin e Familia).dwg

Bruno Gamboa 03/02/25