ZONA D.V.	Nº TAL.	DATA PL.	ÁREA (ha)	VAR.
999 4.84%	1	01/2019	42.45	CTC 04
	2		31.08	
TOTAL PLANTIO			73.53	--------


ÁREAS	(ha)	(%)
PLANTIO	73.53	95.37
CARREADORES	3.57	4.63
OUTROS	0.00	0.00
SUB TOTAL AGRICULTÁVEL	77.10	100.00
AP.P.	0.00	0.00
ÁRVORES	0.00	0.00
OUTROS	0.00	0.00
SUB TOTAL NÃO AGRICULT.	0.00	0.00
ÁREA TOTAL	77.10	100.00

C. NÍVEL: 11816.63 m/l 2.72 ha 3.53 %

LEGENDA


- FAZENDA
- TALHÃO
- CURVA DE NÍVEL
- CARREADOR
- CONFRONTANTE
- REDE ELÉTRICA
- TRAJETO VAZIO
- TRAJETO CARREGADO

PLANTIO MANUAL - ESPAÇAMENTO: 1.50 X 1.50
TIRO MÉDIO ESTIMADO: 196.29m

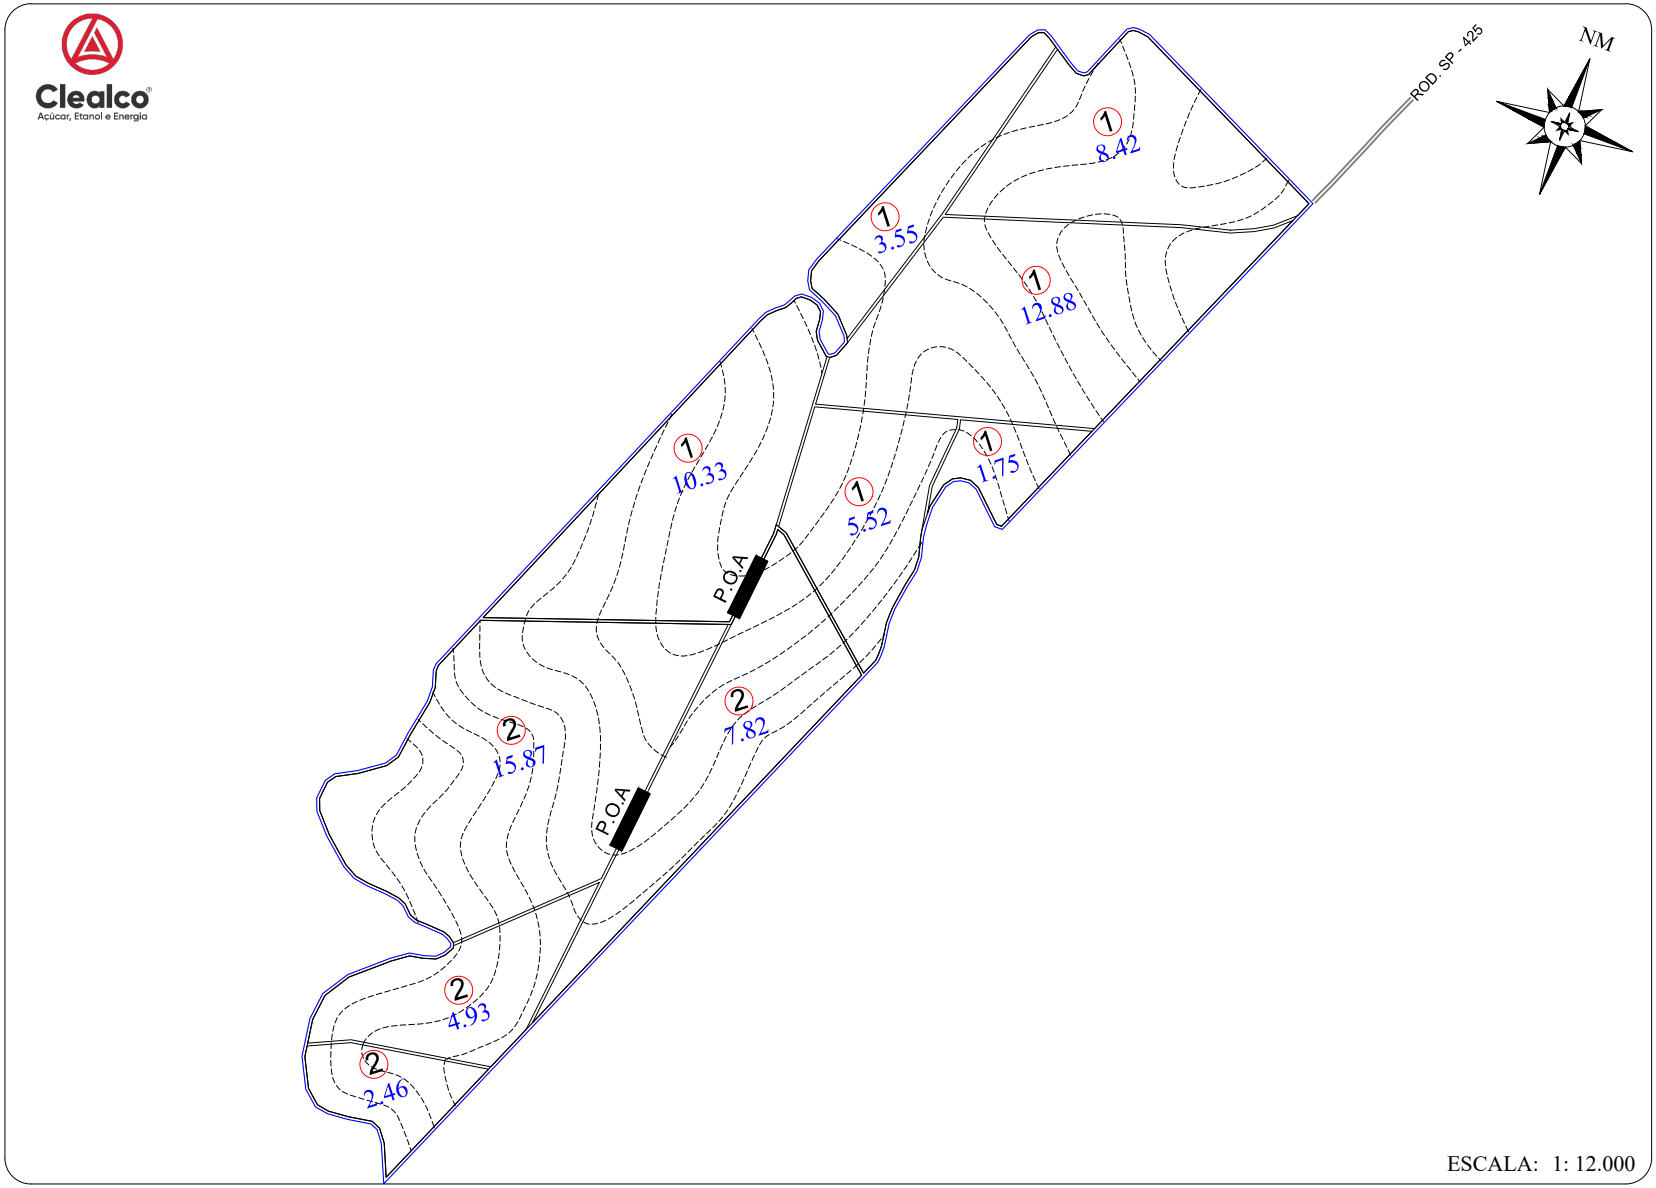

ESCALA: 1: 12.000

CROQUI DE ACESSO

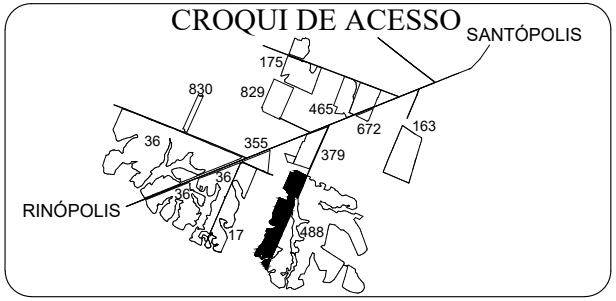

FAZENDA CARAVELA

PROPRIETÁRIO: VILMAR JOSÉ GASTALDI
COMPRADOR: CLEALCO S/A
MUNICÍPIO: SANTÓPOLIS DO AGUAPEI

DISTÂNCIAS (km):
UNID. I - Asfalto: 17.00 Terra.: 3.50
UNID.I I - Asfalto: 51.50 Terra.: 3.50
UNID. III -Asfalto: 58.00 Terra.: 3.50

COORDENADAS: E(X): 546713 N(Y): 7602690
LAT: 21º 40' 42,32726" LONG: 50º 32' 54,46337"

CLEALCO - AÇÚCAR E ALCOOL S/A - DEPARTAMENTO DE TOPOGRAFIA

UNIDADE: I
PARTE: A/A
FUNDO AGRÍCOLA: 306616

M:\01-Mapa de safra\Mapas Atualizados\Terceiro\306616 - Fazenda Caravela (Vilmar José Gastaldi)\306616 - Fazenda Caravela (Vilmar José Gastaldi).dwg

Peterson Santos 09/02/23