
Clealco
Açúcar, Etanol e Energia

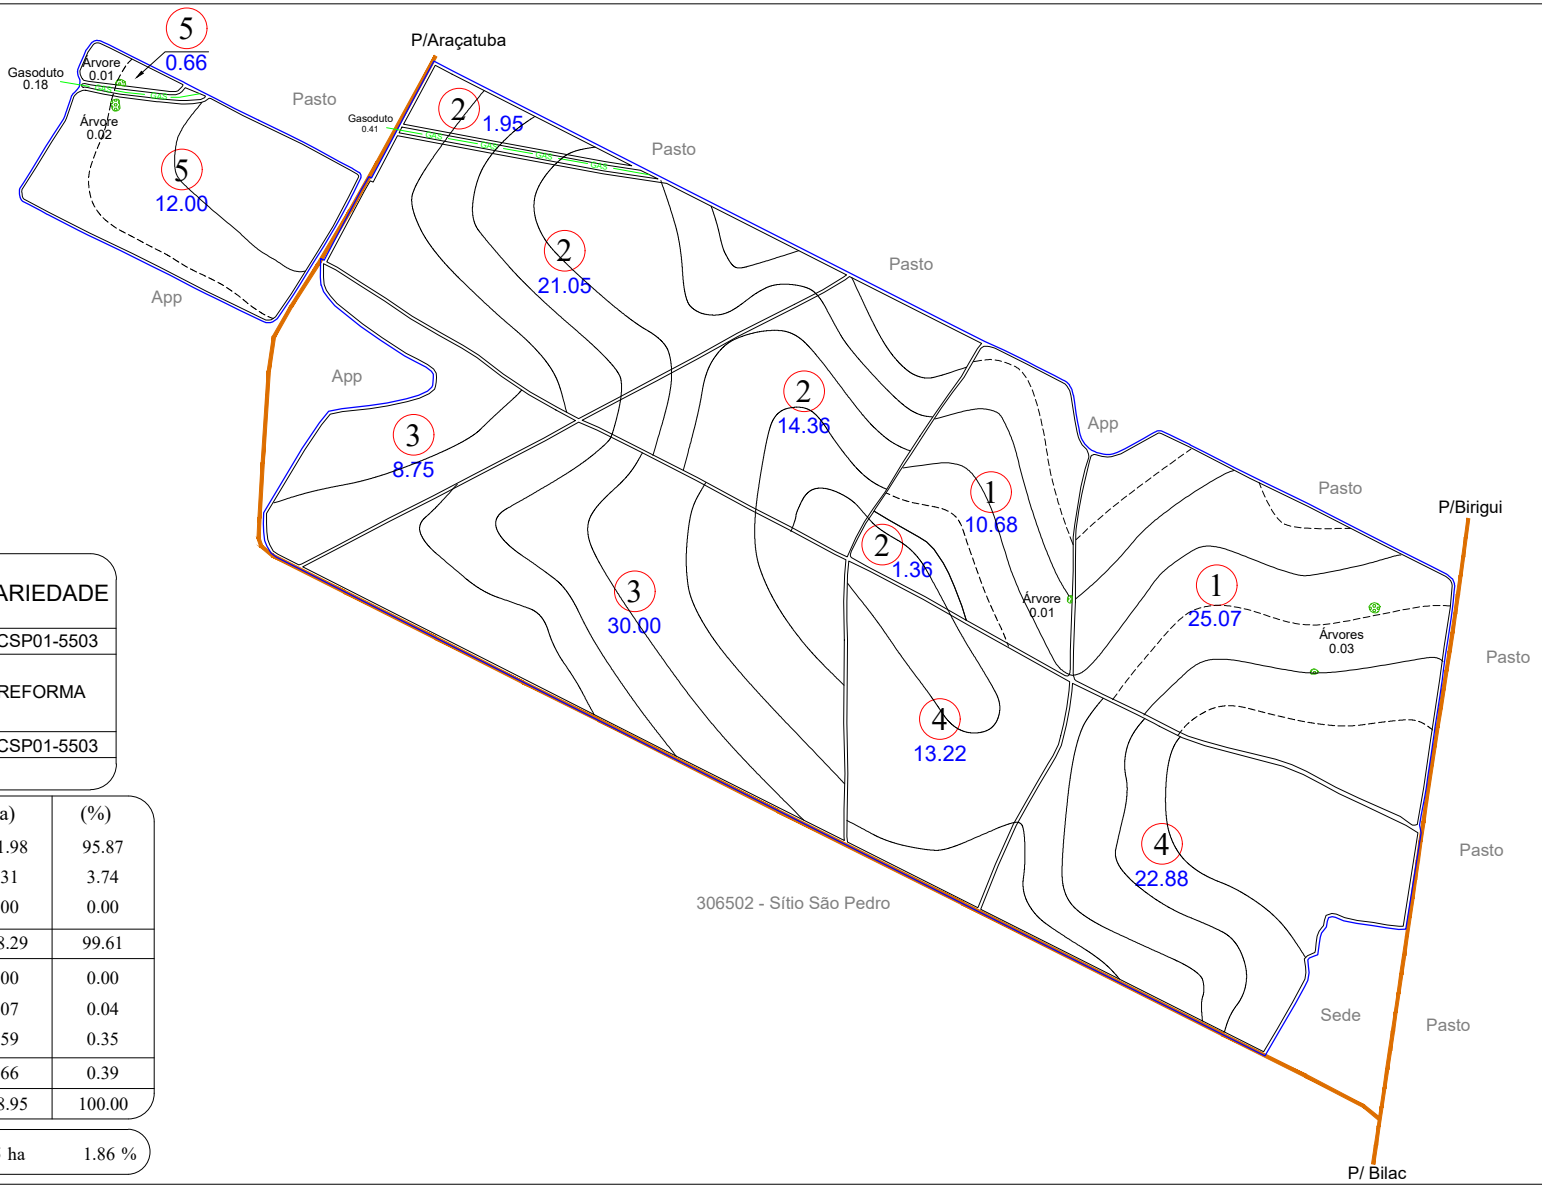

ZONA	Nº TAL.	DATA PL.	ÁREA (ha)	VARIEDADE
1	1	04/2026	35.75	IACSP01-5503
999	2	2027	38.72	REFORMA
	3		38.75	
	4		36.10	
1	5	04/2026	12.66	IACSP01-5503
TOTAL PLANTIO			161.98	

ÁREAS	(ha)	(%)
PLANTIO	161.98	95.87
CARREADORES	6.31	3.74
OUTROS	0.00	0.00
SUB TOTAL AGRICULTÁVEL	168.29	99.61
AP.P.	0.00	0.00
ÁRVORES	0.07	0.04
OUTROS	0.59	0.35
SUB TOTAL NÃO AGRICULT.	0.66	0.39
ÁREA TOTAL	168.95	100.00

C. NÍVEL: 13675.42 m/l 3.15 ha 1.86 %


ESCALA: 1: 12.500

LEGENDA

- FAZENDA
- TALHÃO
- REDE ELÉTRICA
- TERRAÇO BASE LARGA
- TERRAÇO EMBUTIDO

ESPAÇAMENTO: 1.50 x 1.50
TIRO MÉDIO ESTIMADO: 275.83 m
D.V: 4.25 %

CROQUI DE ACESSO

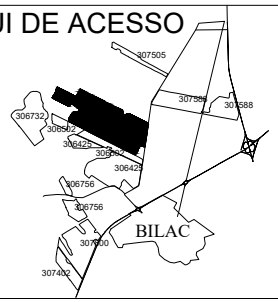

SÍTIO TUPINIQUINS

PROPRIETÁRIO: JORGE LUIZ ZAGO
COMPRADOR: CLEALCO
MUNICÍPIO: BILAC- SP

DISTÂNCIAS (km):
UNID. I - Asfalto: 25.50 Terra.: 2.50
UNID.I I - Asfalto: 80.00 Terra.: 3.00

COORDENADAS: E(X): 552787.30 N(Y): 7635908.31
LAT: -21°22'41.5584" LONG: -50°29'26.8560"
CLEALCO - AÇÚCAR E ALCOOL S/A - DEPARTAMENTO DE GEOTECNOLOGIA

LEVANTAMENTO VIA:
SATÉLITE
GPS / VANT
GOOGLE

UNIDADE: I
PARTE: A/A
FUNDO AGRÍCOLA: 306642

M:\01-Mapa de safra\Mapas Atualizados\Terceiro\306642 - Sítio Tupiniquins (Jorge Luiz Zago)\306642 - Sítio Tupiniquins (Jorge Luiz Zago).dwg

Bruno Gamboa 05/10/26