ZONA DV	CLA	Nº TAL.	DATA PL.	ÁREA (ha)	VAR.
999 5.11 %		1	05/2020	24.03	CTC 04
		2		17.60	
TOTAL PLANTIO				41.63	--------

ÁREAS	(ha)	(%)
PLANTIO	41.63	00.00
CARREADORES	1.47	0.00
OUTROS	0.00	0.00
SUB TOTAL AGRICULTÁVEL	43.10	--------
VÁRZEA	0.00	0.00
MATA	0.02	0.00
OUTROS	0.00	0.00
SUB TOTAL NÃO AGRICULT.	0.02	0.00
ÁREA TOTAL	43.12	--------


C. NÍVEL: 0.00 m/l 0.00 ha 0.00 %

LEGENDA


- FAZENDA
- TALHÃO
- CURVA DE NÍVEL
- CARREADOR
- CONFRONTANTE
- REDE ELÉTRICA
- TRAJETO VAZIO
- TRAJETO CARREGADO

PLANTIO MANUAL - ESPAÇAMENTO: 1.50 X 1.50
TIRO MÉDIO ESTIMADO: 230.10 m

Clealco
Açúcar, Etanol e Energia

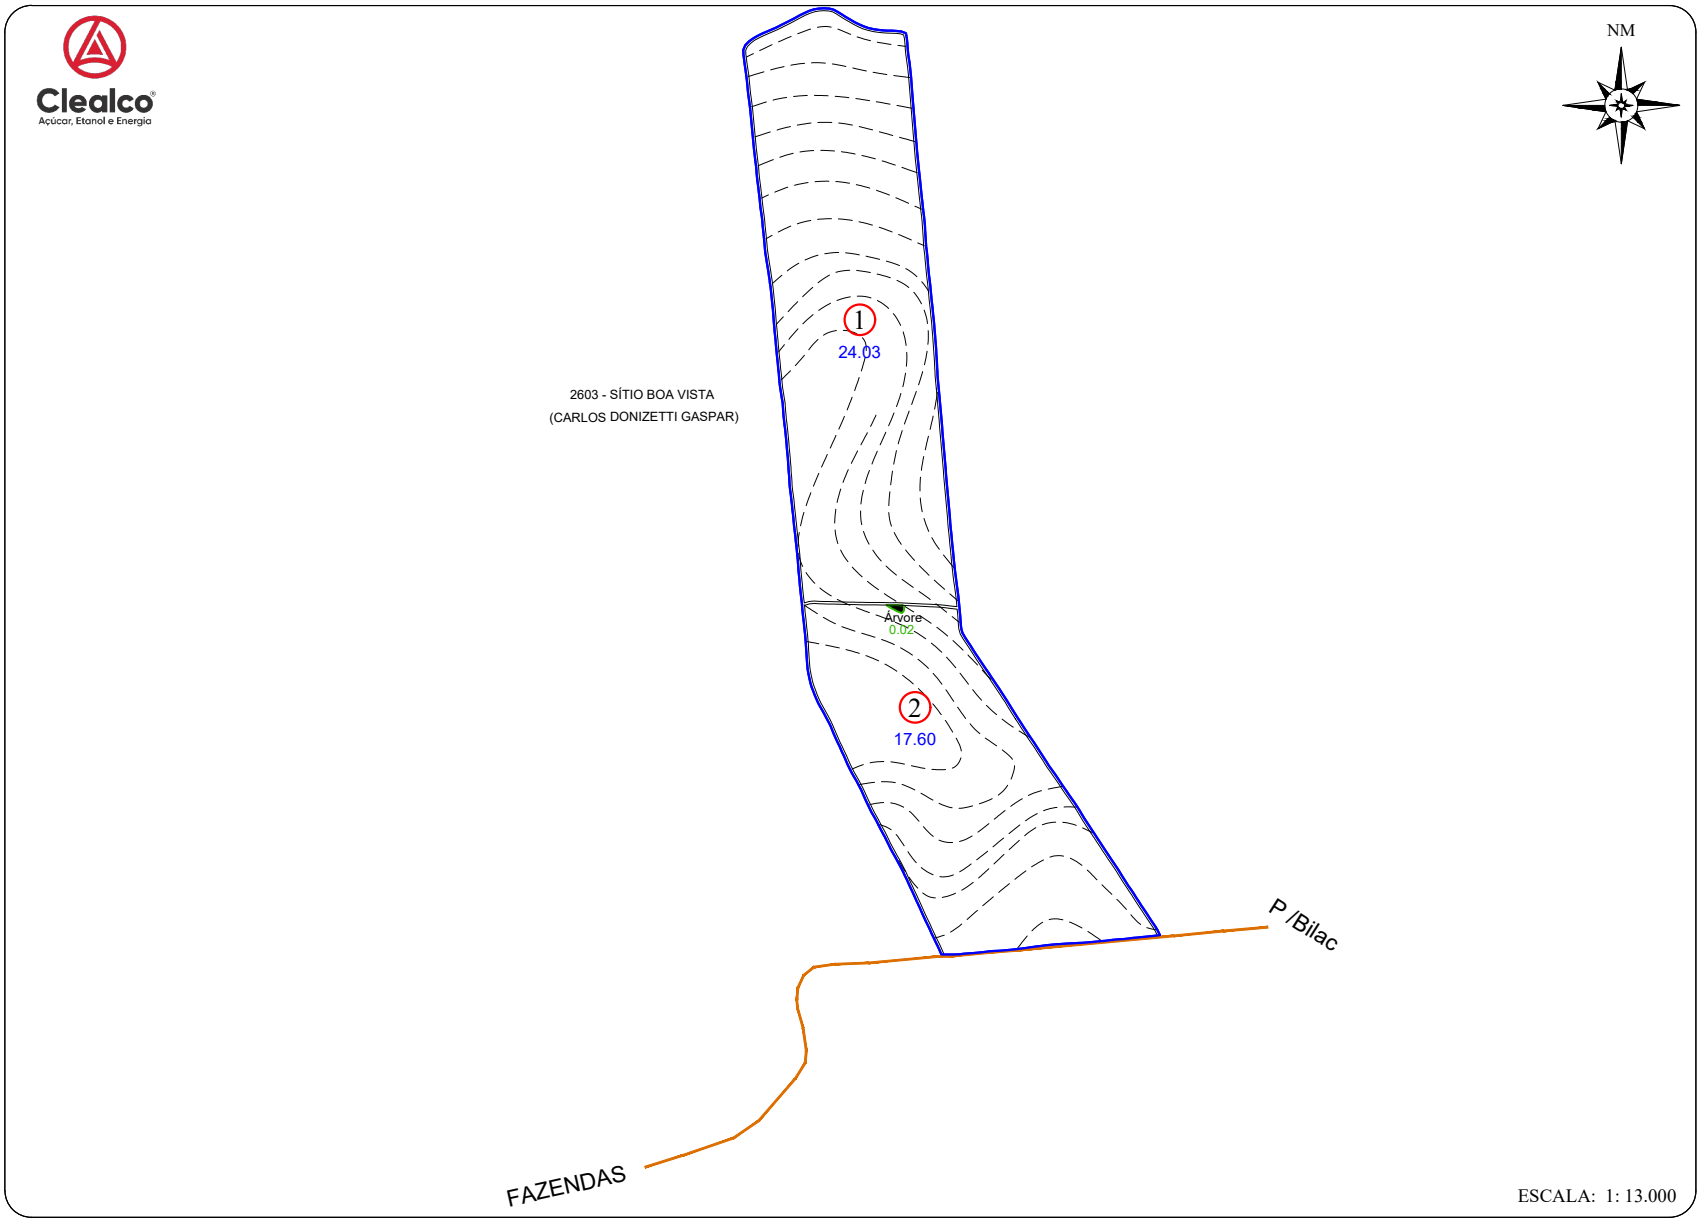

CROQUI DE ACESSO

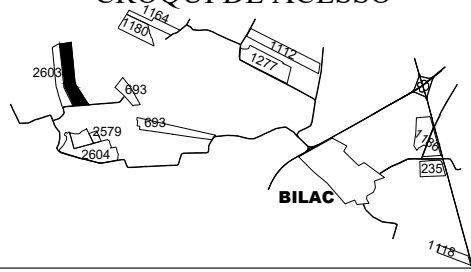

SÍTIO SÃO ROQUE

PROPRIETÁRIO: ANTONIO ROBERTO GENARI
COMPRADOR: CLEALCO S/A
MUNICÍPIO: BILAC

DISTÂNCIAS (km):
UNID. I - Asfalto: 26.00 Terra.: 6.00
UNID.I I - Asfalto: 81.50 Terra.: 6.00
UNID. III -Asfalto: 68.00 Terra.: 6.00

COORDENADAS: E(X): 547712.7417 N(Y): 7635835.089
LAT: -21°22'44.4490" LONG: -50°32'23.0680"

CLEALCO - AÇÚCAR E ALCOOL S/A - DEPARTAMENTO DE TOPOGRAFIA

UNIDADE: I
PARTE: A/A
FUNDO AGRÍCOLA: 306731