
Clealco
Açúcar, Etanol e Energia

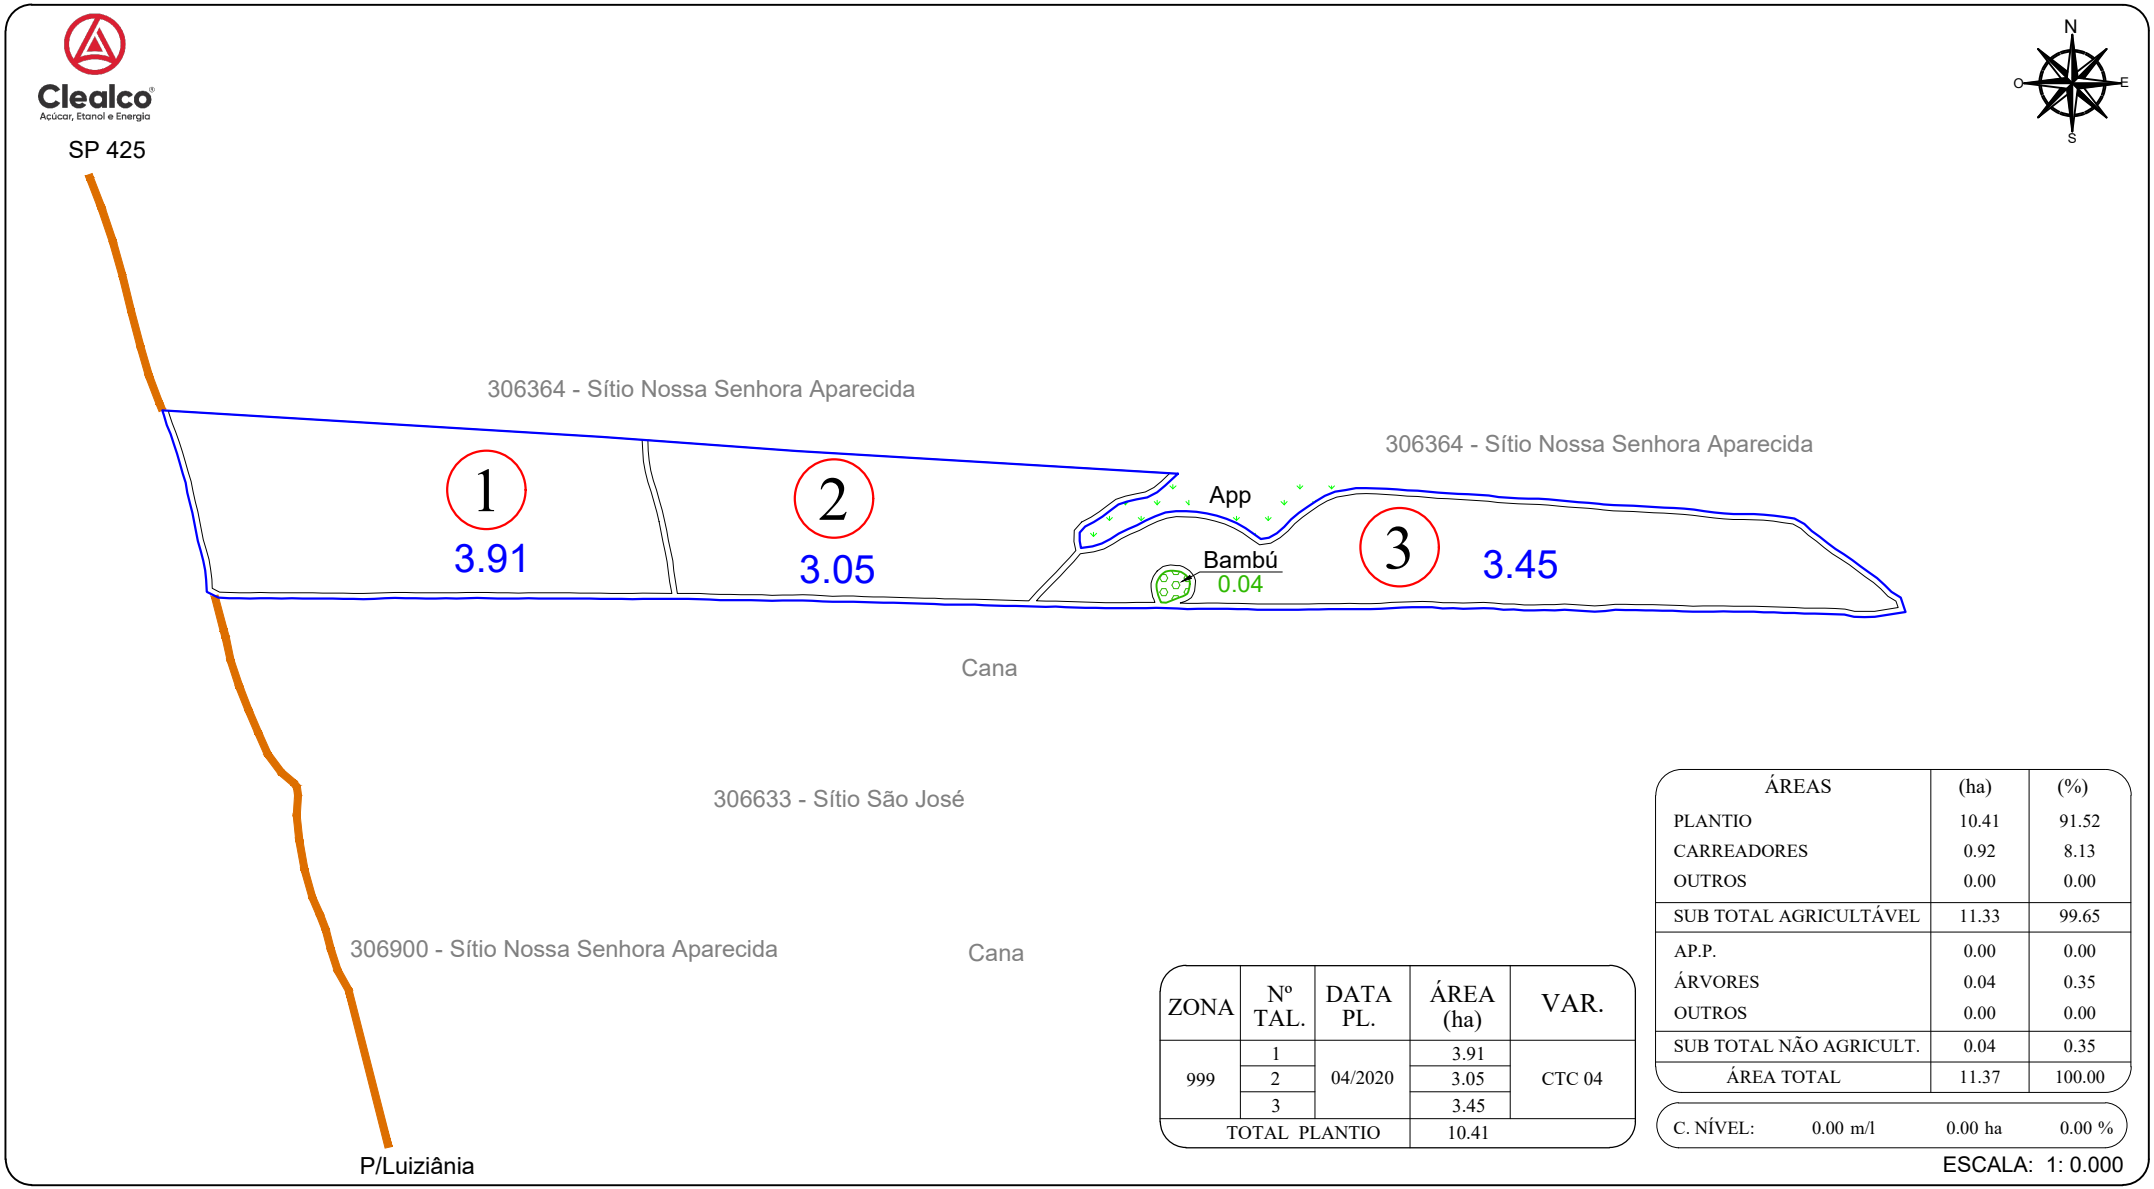

ZONA	Nº TAL.	DATA PL.	ÁREA (ha)	VAR.
999	1	04/2020	3.91	CTC 04
	2		3.05	
	3		3.45	
TOTAL PLANTIO			10.41	

ÁREAS	(ha)	(%)
PLANTIO	10.41	91.52
CARREADORES	0.92	8.13
OUTROS	0.00	0.00
SUB TOTAL AGRICULTÁVEL	11.33	99.65
AP.P.	0.00	0.00
ÁRVORES	0.04	0.35
OUTROS	0.00	0.00
SUB TOTAL NÃO AGRICULT.	0.04	0.35
ÁREA TOTAL	11.37	100.00

C. NÍVEL: 0.00 m/l 0.00 ha 0.00 %


ESCALA: 1: 0.000

LEGENDA

- FAZENDA
- TALHÃO
- REDE ELÉTRICA
- TERRAÇO BASE LARGA
- TERRAÇO EMBUTIDO

ESPAÇAMENTO: 1.50 x 1.50
TIRO MÉDIO ESTIMADO: 000.00 m
D.V: 0.00 %

CROQUI DE ACESSO

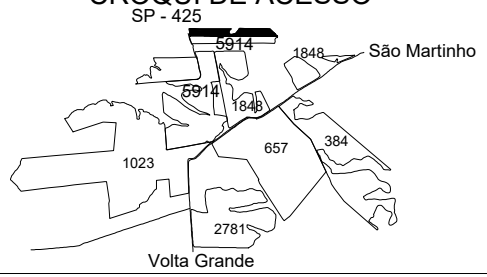

SÍTIO SÃO JUDAS TADEU

PROPRIETÁRIO: JULIANA A. C. TENORIO
COMPRADOR: CLEALCO
MUNICÍPIO: BRAÚNA - SP

DISTÂNCIAS (km):
UNID. I - Asfalto: 20.60 Terra.: 8.90
UNID.I I - Asfalto: 24.00 Terra.: 9.00

COORDENADAS: E(X): 570109.52 N(Y): 7614179.91
LAT: -21°34'26.1328" LONG: -50°19'22.0700"

CLEALCO - AÇÚCAR E ALCOOL S/A - DEPARTAMENTO DE GEOTECNOLOGIA

LEVANTAMENTO VIA:
SATÉLITE
GPS / VANT
GOOGLE

UNIDADE: I
PARTE: A/A
FUNDO AGRÍCOLA: 306750

M:\01-Mapa de safra\Mapas Atualizados\Terceiro\306750 - Sitio São Judas Tadeu (Juliana Ap. Crivelari Tenorio)\306750 - Sitio São Judas Tadeu (Juliana Ap. Crivelari Tenorio).dwg

Bruno Gamboa 24/07/25