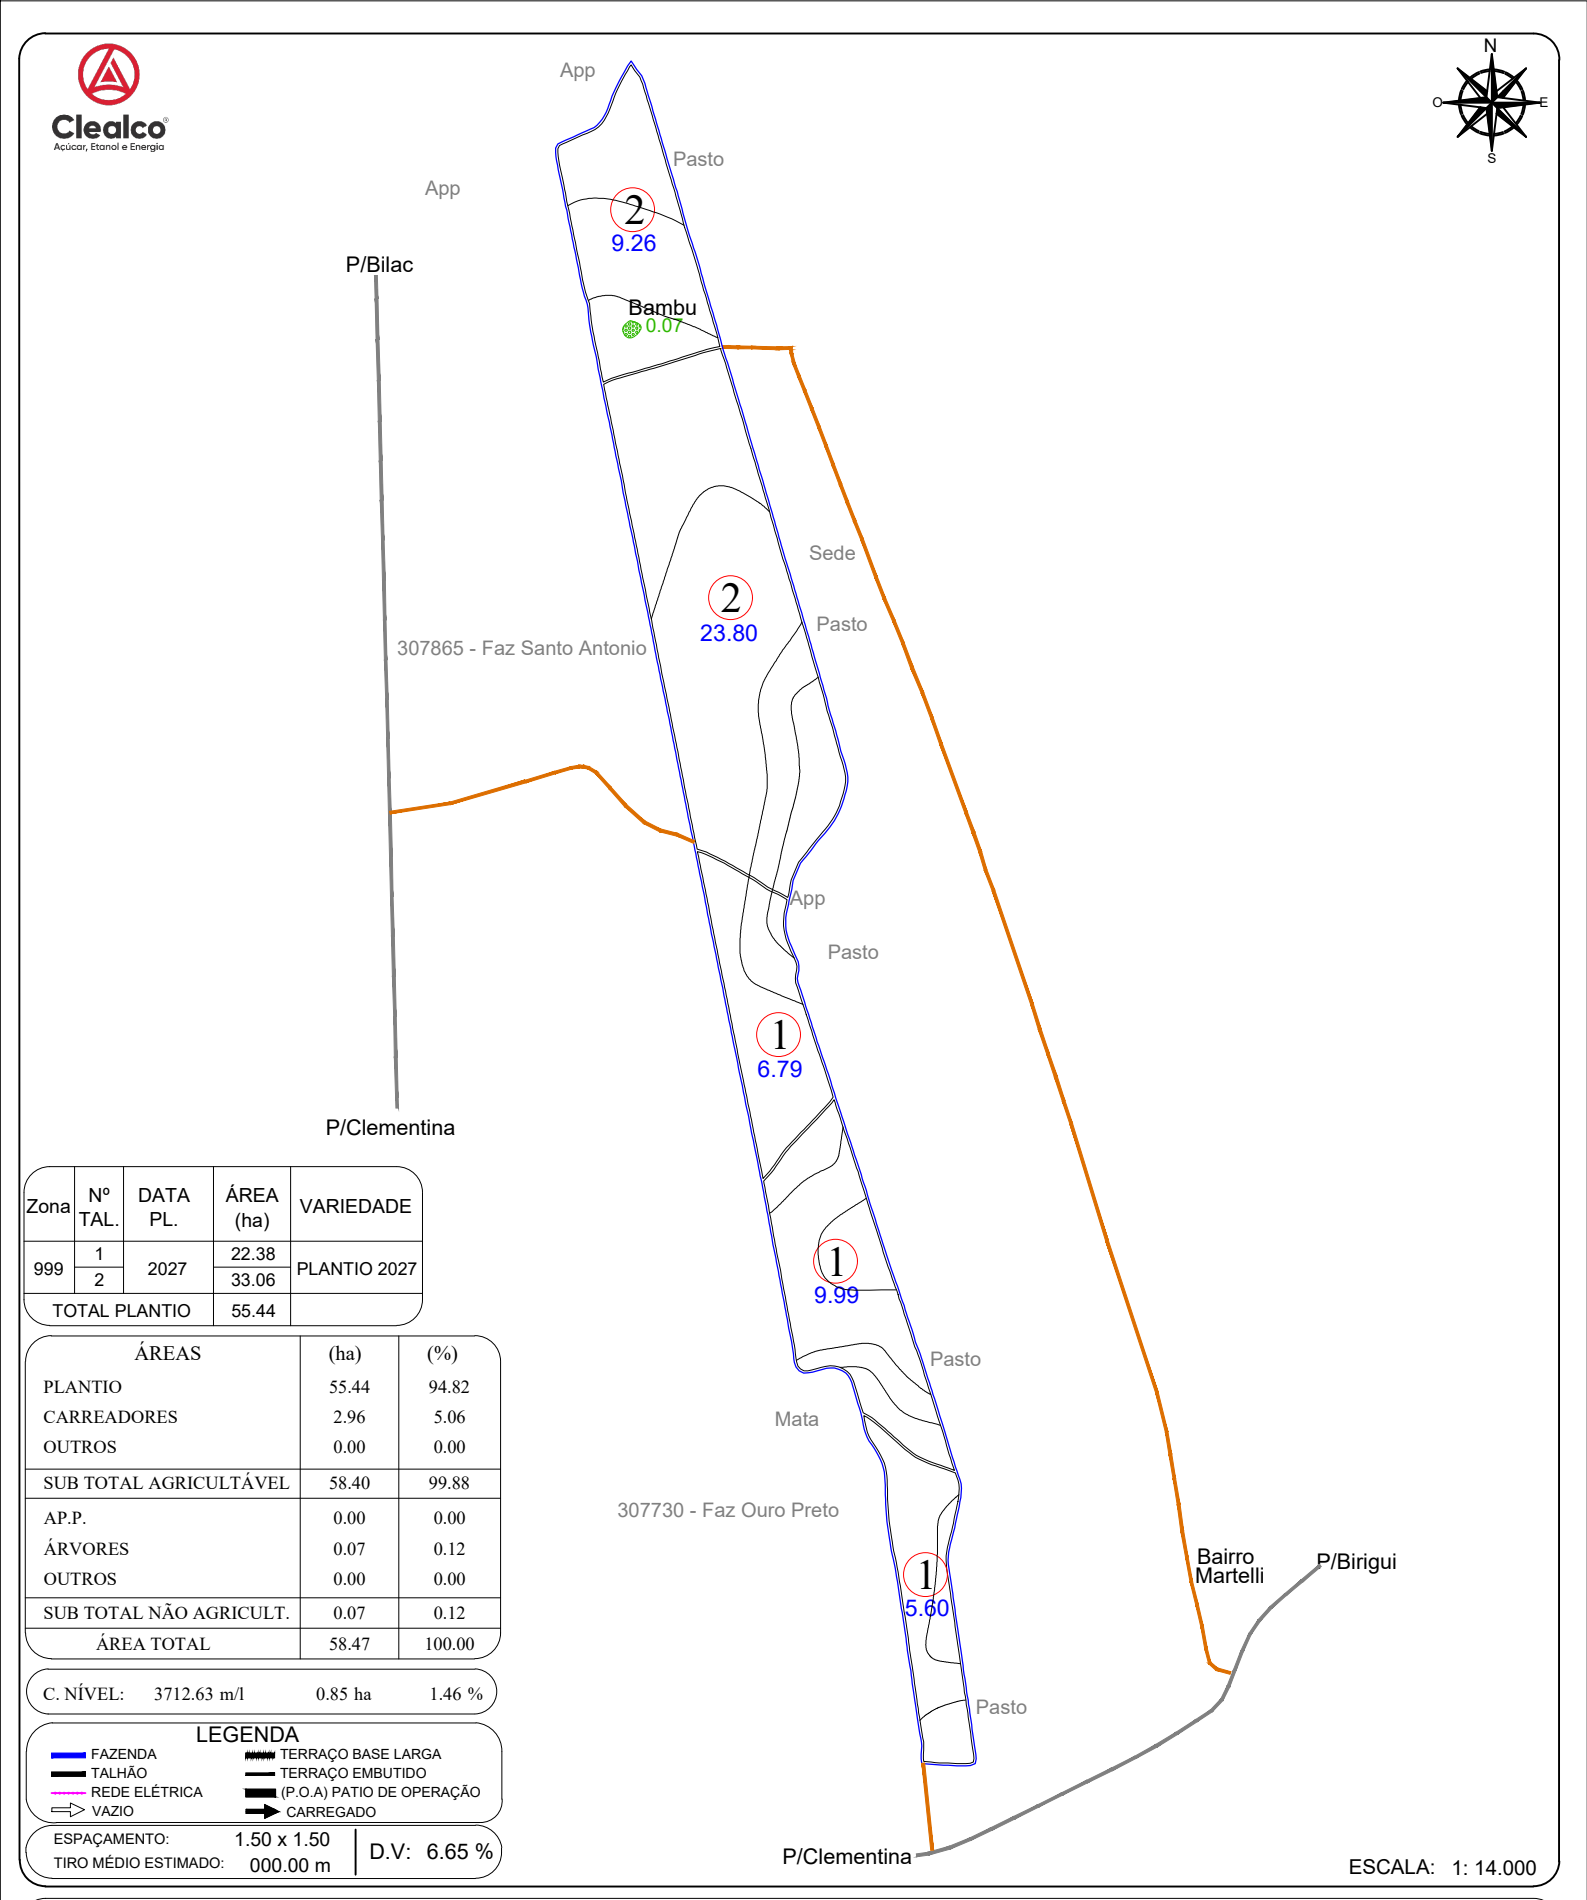


Zona	Nº TAL.	DATA PL.	ÁREA (ha)	VARIEDADE
999	1	2027	22.38	PLANTIO 2027
	2		33.06	
TOTAL PLANTIO			55.44	

ÁREAS	(ha)	(%)
PLANTIO	55.44	94.82
CARREADORES	2.96	5.06
OUTROS	0.00	0.00
SUB TOTAL AGRICULTÁVEL	58.40	99.88
AP.P.	0.00	0.00
ÁRVORES	0.07	0.12
OUTROS	0.00	0.00
SUB TOTAL NÃO AGRICULT.	0.07	0.12
ÁREA TOTAL	58.47	100.00

C. NÍVEL:	3712.63 m/l	0.85 ha	1.46 %


LEGENDA

- FAZENDA
- TALHÃO
- REDE ELÉTRICA
- VAZIO
- TERRAÇO BASE LARGA
- TERRAÇO EMBUTIDO
- (P.O.A) PATIO DE OPERAÇÃO
- CARREGADO

ESPAÇAMENTO: 1.50 x 1.50
TIRO MÉDIO ESTIMADO: 000.00 m
D.V: 6.65 %

ESCALA: 1: 14.000

CROQUI DE ACESSO

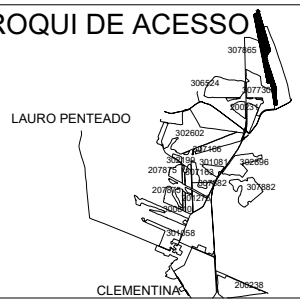

FAZENDA SANTA RITA

PROPRIETÁRIO: JORGE LUIZ ZAGO
COMPRADOR: CLEALCO
MUNICÍPIO: CLEMENTINA - SP

DISTÂNCIAS (km):
UNID. I - Asfalto: 8.80 Terra.: 2.90
UNID.I I - Asfalto: 41.30 Terra.: 16.6

COORDENADAS: E(X): 559729.18 N(Y): 7622644.38
LAT: -21°29'52.1882" LONG: -50°25'24.0995"

CLEALCO - AÇÚCAR E ALCOOL S/A - DEPARTAMENTO DE GEOTECNOLOGIA

LEVANTAMENTO VIA:
- SATÉLITE
- GPS / VANT
- GOOGLE

UNIDADE: I
PARTE: A/B
FUNDO AGRÍCOLA: 306753

M:\01-Mapa de safra\Mapas Atualizados\Terceiro\306753 - Fazenda Santa Rita (Jorge Luiz Zago)\306753 A - Fazenda Santa Rita (Jorge Luiz Zago).dwg

Bruno Gamboa 08/10/26