
Clealco
Açúcar, Etanol e Energia

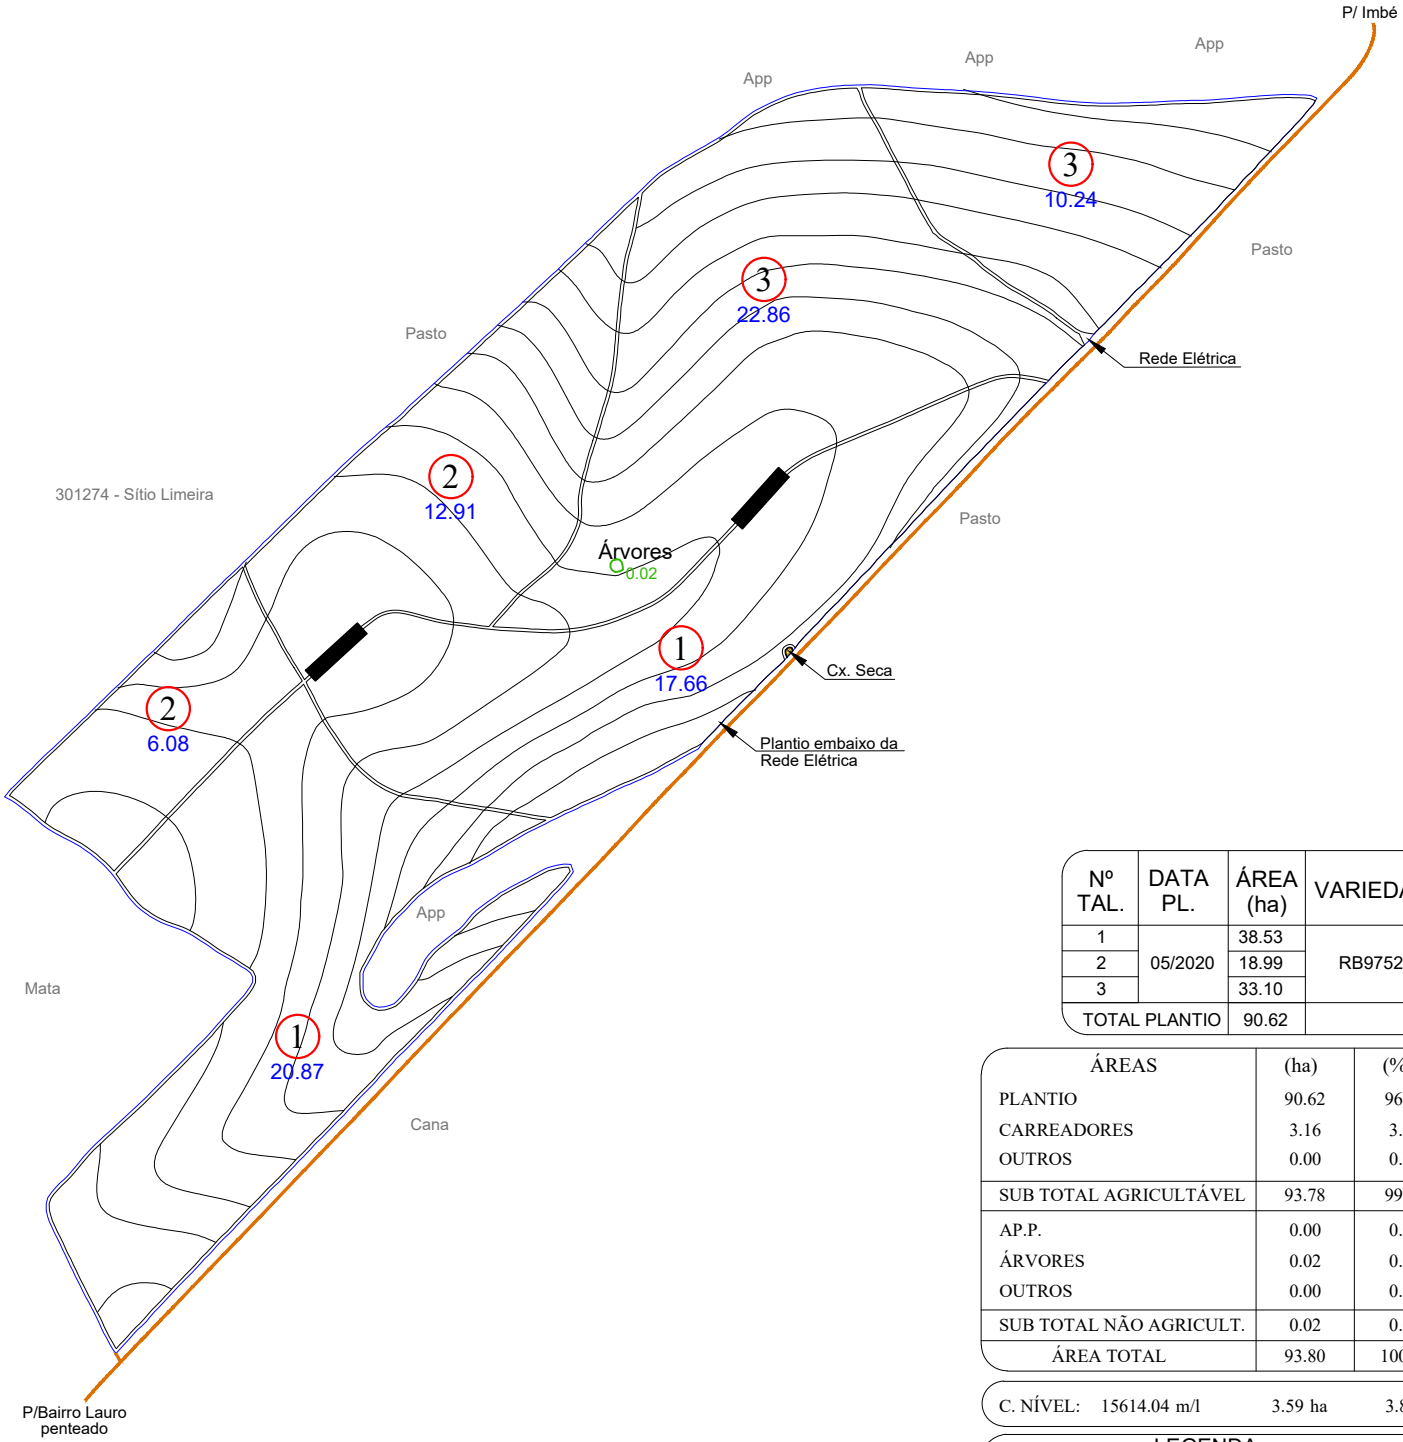

Nº TAL.	DATA PL.	ÁREA (ha)	VARIEDADE
1	05/2020	38.53	RB975201
2		18.99	
3		33.10	
TOTAL PLANTIO		90.62	

ÁREAS	(ha)	(%)
PLANTIO	90.62	96.61
CARREADORES	3.16	3.37
OUTROS	0.00	0.00
SUB TOTAL AGRICULTÁVEL	93.78	99.98
AP.P.	0.00	0.00
ÁRVORES	0.02	0.02
OUTROS	0.00	0.00
SUB TOTAL NÃO AGRICULT.	0.02	0.02
ÁREA TOTAL	93.80	100.00

C. NÍVEL: 15614.04 m/l 3.59 ha 3.83 %


LEGENDA

- FAZENDA
- TALHÃO
- REDE ELÉTRICA
- TERRAÇO BASE LARGA
- TERRAÇO EMBUTIDO
- (P.O.A) PATIO DE OPERAÇÃO

ESPAÇAMENTO: 1.50 x 1.50
TIRO MÉDIO ESTIMADO: 276.00 m
D.V: 5.26 %

ESCALA: 1: 10.000

CROQUI DE ACESSO

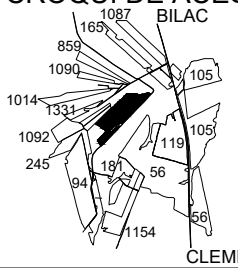

SÍTIO SANTO ANTONIO

PROPRIETÁRIO: ZEIDA BRUSCHETA
COMPRADOR: CLEALCO
MUNICÍPIO: BILAC - SP

DISTÂNCIAS (km):
UNID. I - Asfalto: 22.00 Terra.: 2.50
UNID.I I - Asfalto: 62.00 Terra.: 2.50

COORDENADAS: E(X): 556611.72 N(Y): 7625554.82
LAT: -21°28'17.8903" LONG: -50°27'12.7970"

CLEALCO - AÇÚCAR E ALCOOL S/A - DEPARTAMENTO DE GEOTECNOLOGIA

LEVANTAMENTO VIA:
SATÉLITE
GPS / VANT
GOOGLE

UNIDADE: I
PARTE: A/A
FUNDO AGRÍCOLA: 306754

M:\01-Mapa de safra\Mapas Atualizados\Terceiro\306754 - Sitio Santo Antonio (Jorge Luiz Zago)\306754 - Sitio Santo Antonio (Zelda Bruscheta).dwg

Peterson Santos 30/01/25