ZONA D.V.	Nº TAL.	DATA PL.	ÁREA (ha)	VARIEDADE
999 4.87 %	1	05/2024	18.00	RB 975201
	2		5.45	
	3		27.27	
	4		16.22	
	5		7.84	
	6	04/2019	1.27	CTC 04
	7	04/2020	0.56	
	8		1.10	
	9	05/2024	31.58	RB 975201
	10		41.57	
	11		36.84	
TOTAL PLANTIO			187.70	--------

ÁREAS	(ha)	(%)
PLANTIO	187.70	94.70
CARREADORES	8.00	4.04
OUTROS	0.26	0.13
SUB TOTAL AGRICULTÁVEL	195.96	98.86
AP.P.	2.19	1.10
ÁRVORES	0.02	0.01
OUTROS	0.04	0.02
SUB TOTAL NÃO AGRICULT.	2.25	1.14
ÁREA TOTAL	198.21	100.00

C. NÍVEL: 23647.42 m/l 5.44 ha 2.74 %


LEGENDA

- FAZENDA
- TALHÃO
- CURVA DE NÍVEL
- CARREADOR
- CONFRONTANTE
- REDE ELÉTRICA
- TRAJETO VAZIO
- TRAJETO CARREGADO

PLANTIO MANUAL - ESPAÇAMENTO: 1.50 X 1.50
TIRO MÉDIO ESTIMADO: 279.03 m


Clealco
Açúcar, Etanol e Energia

NM

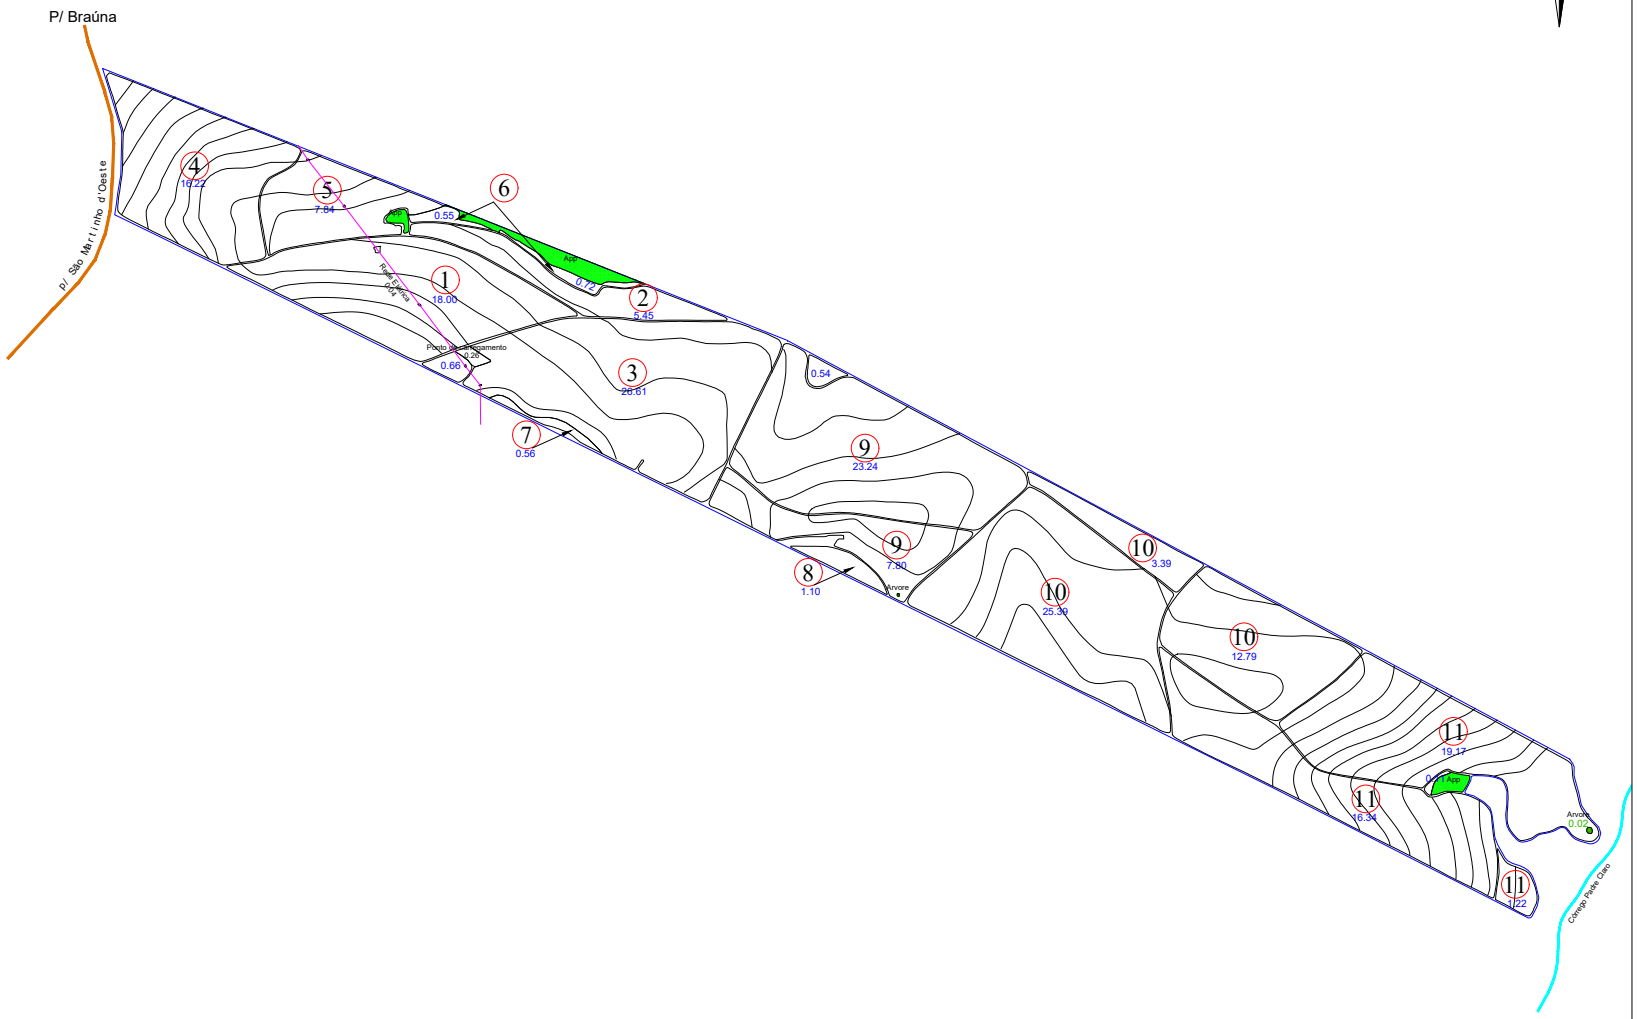

ESCALA: 1: 20.000

CROQUI DE ACESSO

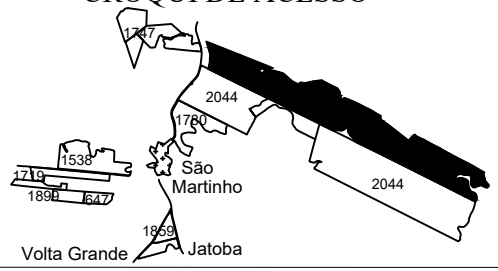

FAZENDA SANTA CLARA

PROPRIETÁRIO: ESPOLIO DE TARCILIO TRISOGLIO
COMPRADOR: CLEALCO S/A
MUNICÍPIO: ALTO ALEGRE

DISTÂNCIAS (km):

UNID. I - Asfalto:	51.00	Terra.:	4.00
UNID.I I - Asfalto:	39.00	Terra.:	4.00
UNID. III -Asfalto:	3.30	Terra.:	23.40

COORDENADAS: E(X): 577785.00 N(Y): 7614520.11
LAT: -21°34'13.9242" LONG: -50°14'55.2429"

CLEALCO - AÇÚCAR E ALCOOL S/A - DEPARTAMENTO DE TOPOGRAFIA

UNIDADE: I

PARTE: A/A

FUNDO AGRÍCOLA: 306762

M:\01-Mapa de safra\Mapas Atualizados\Terceiro\306762 - Fazenda Santa Clara (Espolio de Tarcilio Trisoglio)\306762 - Fazenda Santa Clara (Espolio de Tarcilio Trisoglio).dwg

Benati 03/10/2024