
Clealco
Açúcar, Etanol e Energia

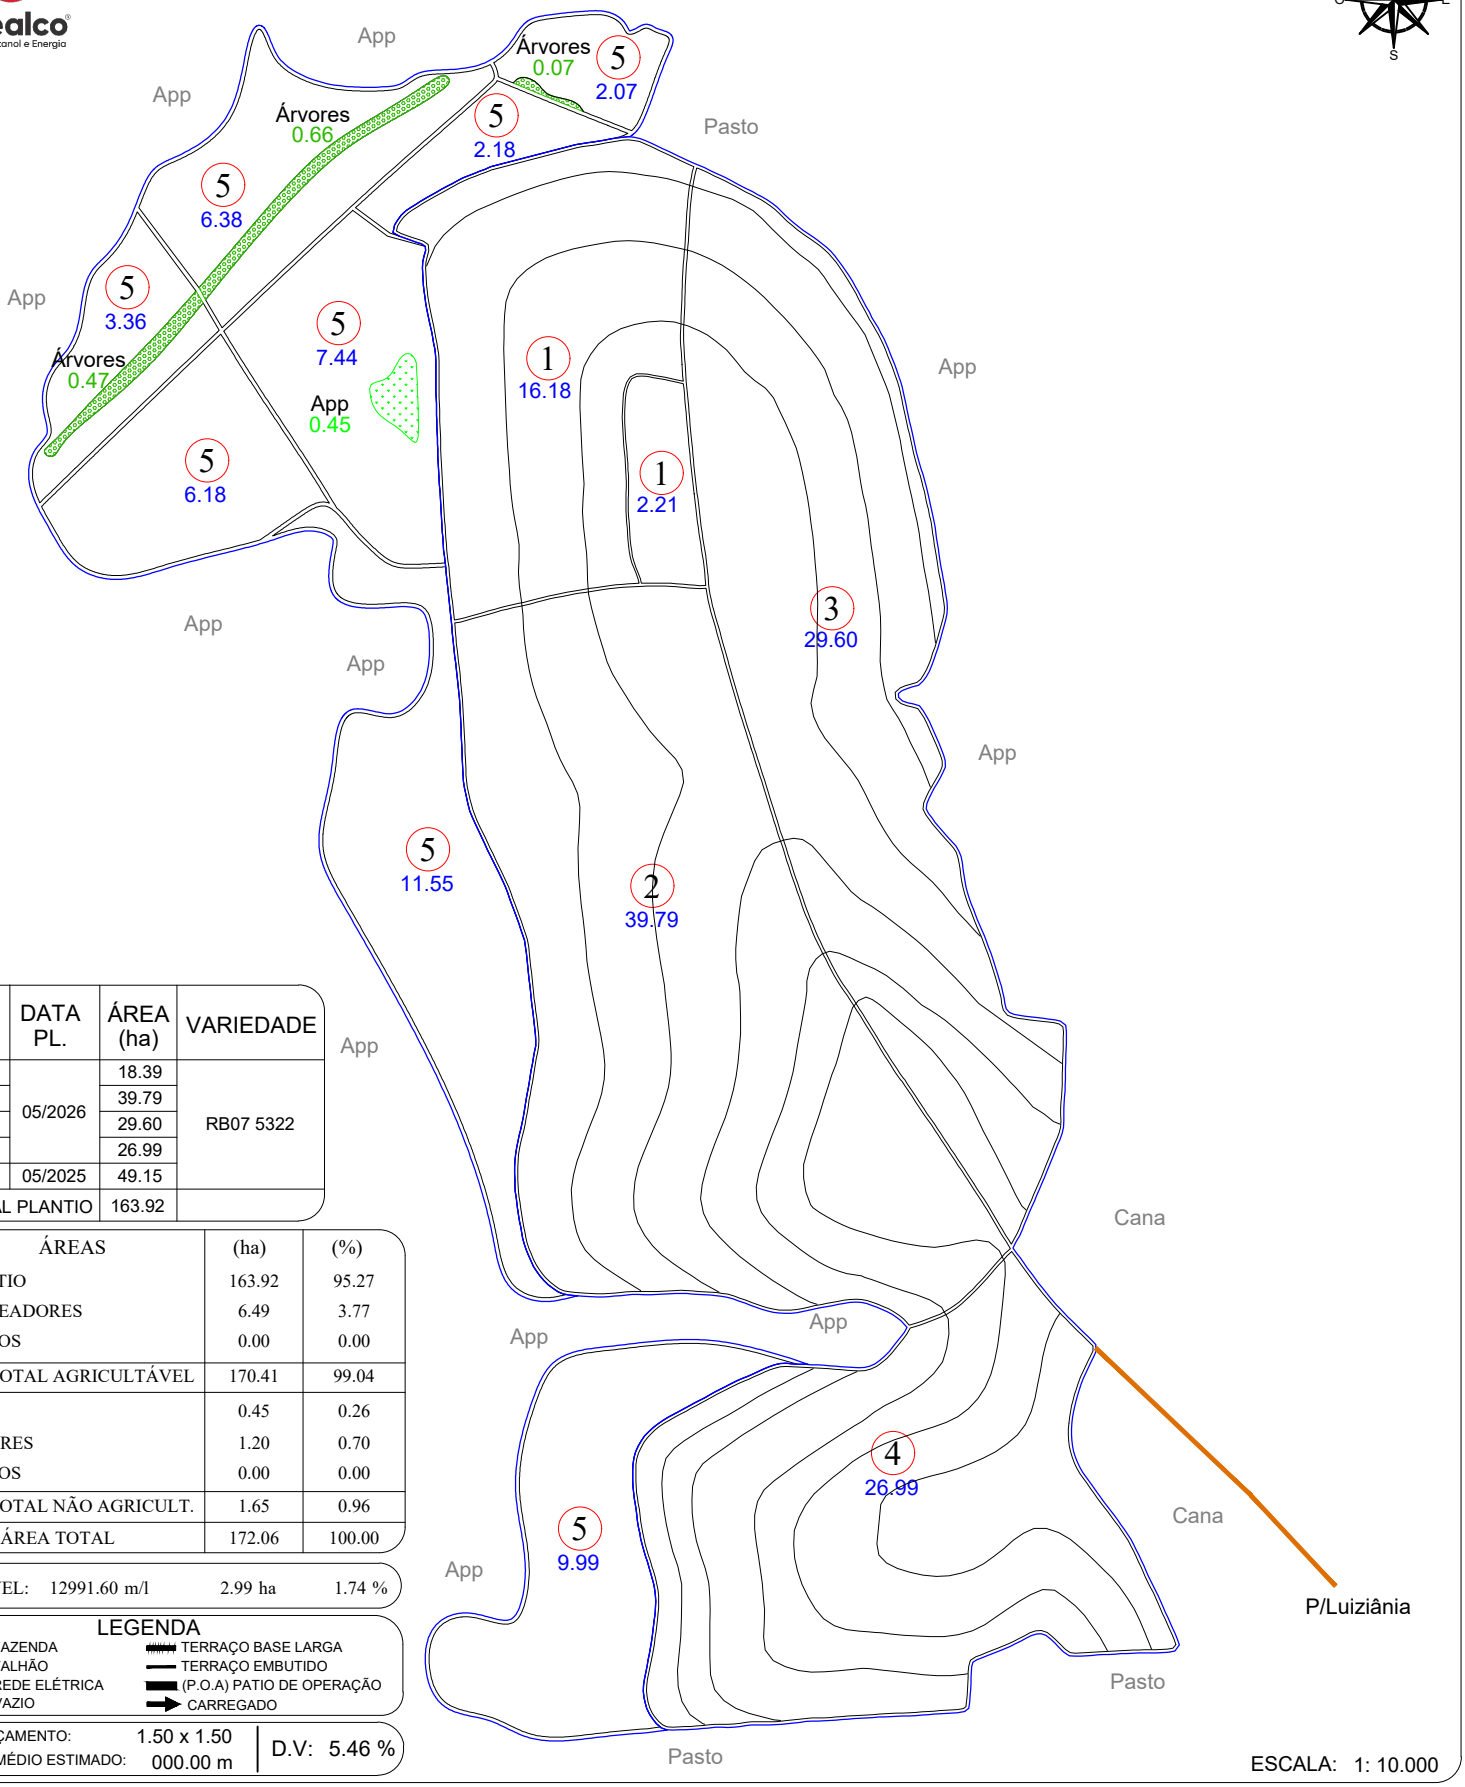

Nº TAL.	DATA PL.	ÁREA (ha)	VARIEDADE
1	05/2026	18.39	RB07 5322
2		39.79	
3		29.60	
4		26.99	
5	05/2025	49.15	
TOTAL PLANTIO		163.92	

ÁREAS	(ha)	(%)
PLANTIO	163.92	95.27
CARREADORES	6.49	3.77
OUTROS	0.00	0.00
SUB TOTAL AGRICULTÁVEL	170.41	99.04
AP.P.	0.45	0.26
ÁRVORES	1.20	0.70
OUTROS	0.00	0.00
SUB TOTAL NÃO AGRICULT.	1.65	0.96
ÁREA TOTAL	172.06	100.00

C. NÍVEL: 12991.60 m/l 2.99 ha 1.74 %


LEGENDA

- FAZENDA
- TALHÃO
- REDE ELÉTRICA
- VAZIO
- TERRAÇO BASE LARGA
- TERRAÇO EMBUTIDO
- (P.O.A) PATIO DE OPERAÇÃO
- CARREGADO

ESPAÇAMENTO: 1.50 x 1.50
TIRO MÉDIO ESTIMADO: 000.00 m
D.V: 5.46 %

ESCALA: 1: 10.000

CROQUI DE ACESSO

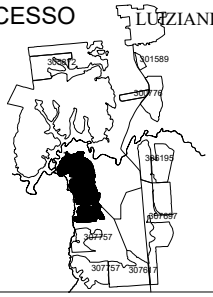

FAZENDA SANTA CLARA II

PROPRIETÁRIO: WILLIAN ÁVILLA
COMPRADOR: CLEALCO
MUNICÍPIO: ARCO IRIS - SP

DISTÂNCIAS (km):
UNID. I - Asfalto: 32.50 Terra.: 8.50
UNID.I I - Asfalto: 16.50 Terra.: 14.50

COORDENADAS: E(X): 567800.92 N(Y): 7597551.20
LAT: -21°43'27.2809" LONG: -50°20'39.9024"

CLEALCO - AÇÚCAR E ALCOOL S/A - DEPARTAMENTO DE GEOTECNOLOGIA

LEVANTAMENTO VIA:
- SATÉLITE
- GPS / VANT
- GOOGLE

UNIDADE: II
PARTE: A/A
FUNDO AGRÍCOLA: 306770

M:\01-Mapa de safra\Mapas Atualizados\Terceiro\306770 - Fazenda Santa Clara II (Willian Avilla)\306770 - Fazenda Santa Clara II (Willian Avilla) - Expans&o.dwg

Bruno Gamboa 13/07/26