ZONA DV	Nº TAL.	DATA PL.	ÁREA (ha)	VARIEDADE
999	1	07/2023	15.06	RB 975201
4.90%	2	05/2022	19.61	CTC 04
TOTAL PLANTIO			34.67	--------

ÁREAS	(ha)	(%)
PLANTIO	34.67	94.17
CARREADORES	1.97	5.34
OUTROS	0.00	0.00
SUB TOTAL AGRICULTÁVEL	36.64	99.51
AP.P.	0.00	0.00
ÁRVORES	0.18	0.49
OUTROS	0.00	0.00
SUB TOTAL NÃO AGRICULT.	0.18	0.49
ÁREA TOTAL	36.82	100.00

C. NÍVEL:	0.00 m/l	0.00 ha	0.00 %

LEGENDA

FAZENDA	CONFRONTANTE
TALHÃO	REDE ELÉTRICA
CURVA DE NÍVEL	TRAJETO VAZIO
CARREADOR	TRAJETO CARREGADO

PLANTIO MANUAL - ESPAÇAMENTO: 1.50 X 1.50
TIRO MÉDIO ESTIMADO: 189.76 m

Clealco
Açúcar, Etanol e Energia

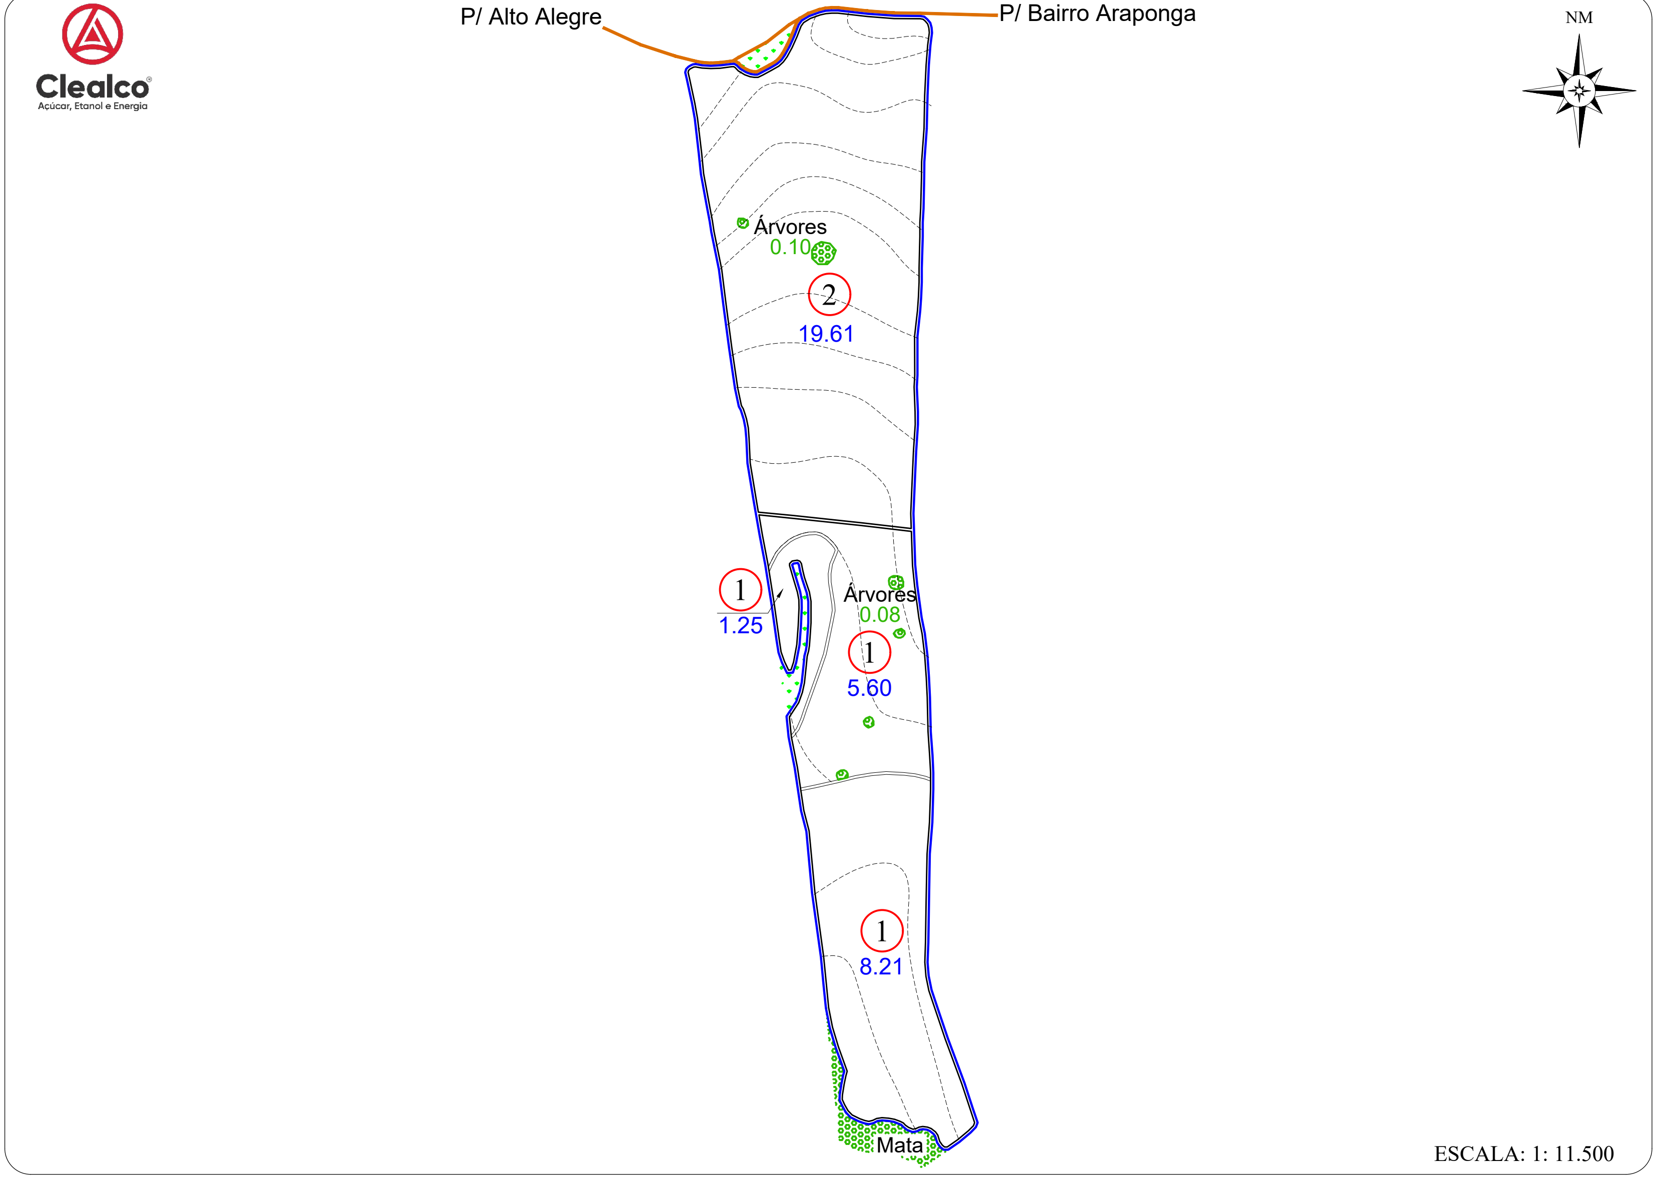

ESCALA: 1: 11.500

CROQUI DE ACESSO

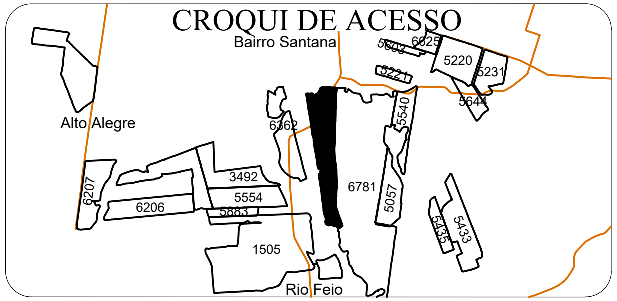

SÍTIO MATÃO

PROPRIETÁRIO:	RENAN V. DE ANDRADE
COMPRADOR:	CLEALCO S/A
MUNICÍPIO:	ALTO ALEGRE

DISTÂNCIAS (km):

UNID. I -	Asfalto:	60.00	Terra.:	2.50
UNID.I I -	Asfalto:	47.70	Terra.:	2.50
UNID. III -	Asfalto:	13.00	Terra.:	2.50

COORDENADAS: E(X):	591902.30	N(Y):	7611671.90
LAT:	-21°35'44.1396"	LONG:	-50°6'43.8301"

CLEALCO - AÇÚCAR E ALCOOL S/A - DEPARTAMENTO DE TOPOGRAFIA

UNIDADE:
II

PARTE:
A/A

FUNDO AGRÍCOLA:
306782

M:\01-Mapa de safra\Mapas Atualizados\Terceiro\306782 - Sitio Matão (Renan Vilanova de Andrade e Outra)\306782 - Sitio Matão (Renan Vilanova de Andrade e Outra).dwg

Fernanda Bezerra 11/05/22