ZONA D.V.	Nº TAL.	DATA PL.	ÁREA (ha)	VARIEDADE
999 4.44 %	1	03/2022	17.17	RB 975201
	2		25.94	
	3		18.83	
	4		7.40	
	5		11.43	
TOTAL PLANTIO			80.77	--------

ÁREAS	(ha)	(%)
PLANTIO	80.77	96.44
CARREADORES	2.83	3.38
OUTROS	0.00	0.00
SUB TOTAL AGRICULTÁVEL	83.60	99.82
AP.P.	0.00	0.00
ÁRVORES	0.15	0.18
OUTROS	0.00	0.00
SUB TOTAL NÃO AGRICULT.	0.15	0.18
ÁREA TOTAL	83.75	100.00


C. NÍVEL: 0.00 m/l 0.00 ha 0.00 %

LEGENDA


- FAZENDA
- TALHÃO
- CURVA DE NÍVEL
- CARREADOR
- CONFRONTANTE
- REDE ELÉTRICA
- TRAJETO VAZIO
- TRAJETO CARREGADO

PLANTIO MANUAL - ESPAÇAMENTO: 1.50 X 1.50
TIRO MÉDIO ESTIMADO: 291.11 m

Clealco
Açúcar, Etanol e Energia

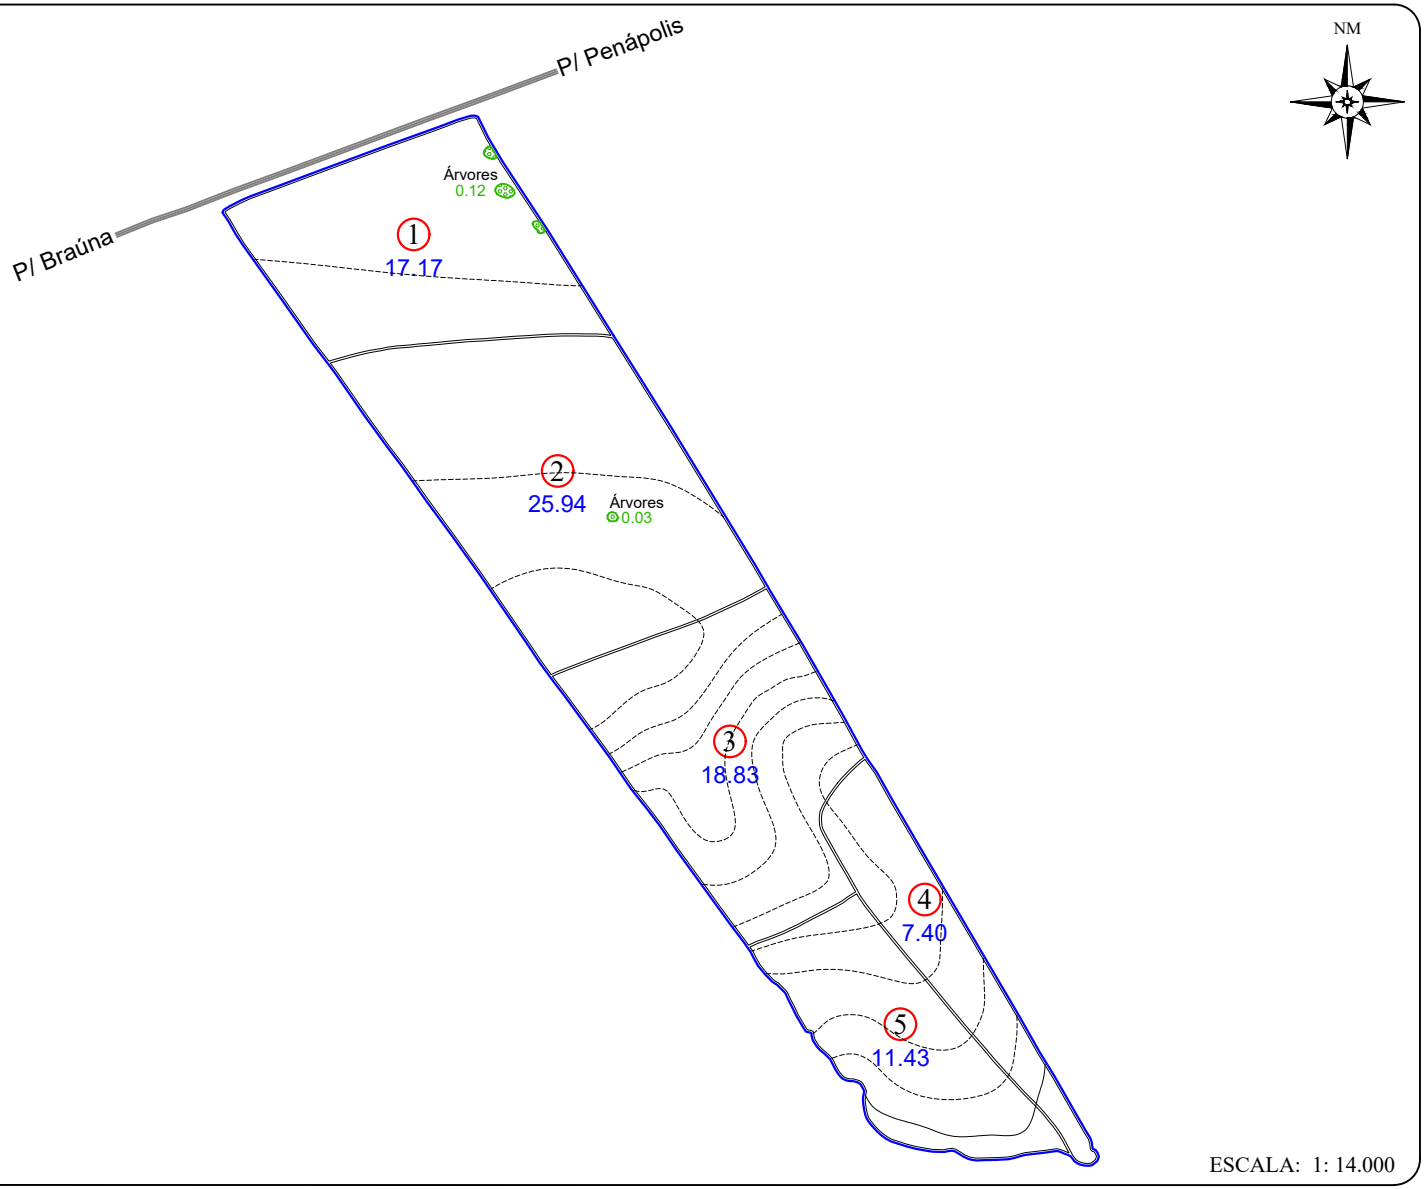

CROQUI DE ACESSO

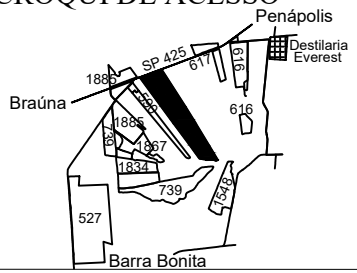

ESTANCIA MONTE BELO

PROPRIETÁRIO: JOSE MARIA TRISOGLIO
COMPRADOR: CLEALCO S/A
MUNICÍPIO: PENÁPOLIS

DISTÂNCIAS (km):
UNID. I - Asfalto: 27.00 Terra.: 1.50
UNID.I I - Asfalto: 30.00 Terra.: 7.00
UNID. III -Asfalto: 3.00 Terra.: 10.50

COORDENADAS: E(X): 581181.76 N(Y): 7622699.21
LAT: -21°29'47.3692" LONG: -50°12'58.5663"

CLEALCO - AÇÚCAR E ALCOOL S/A - DEPARTAMENTO DE TOPOGRAFIA

UNIDADE: I
PARTE: A/A
FUNDO AGRÍCOLA: 306785

M:\01-Mapa de safra\Mapas Atualizados\Terceiro\306785 - Estancia Monte Belo (Jose Maria Trisoglio)\306785 - Estancia Monte Belo (Jose Maria Trisoglio).dwg

Fernanda Bezerra 22/01/24