
307827 - Fazenda N.S. De Fátima

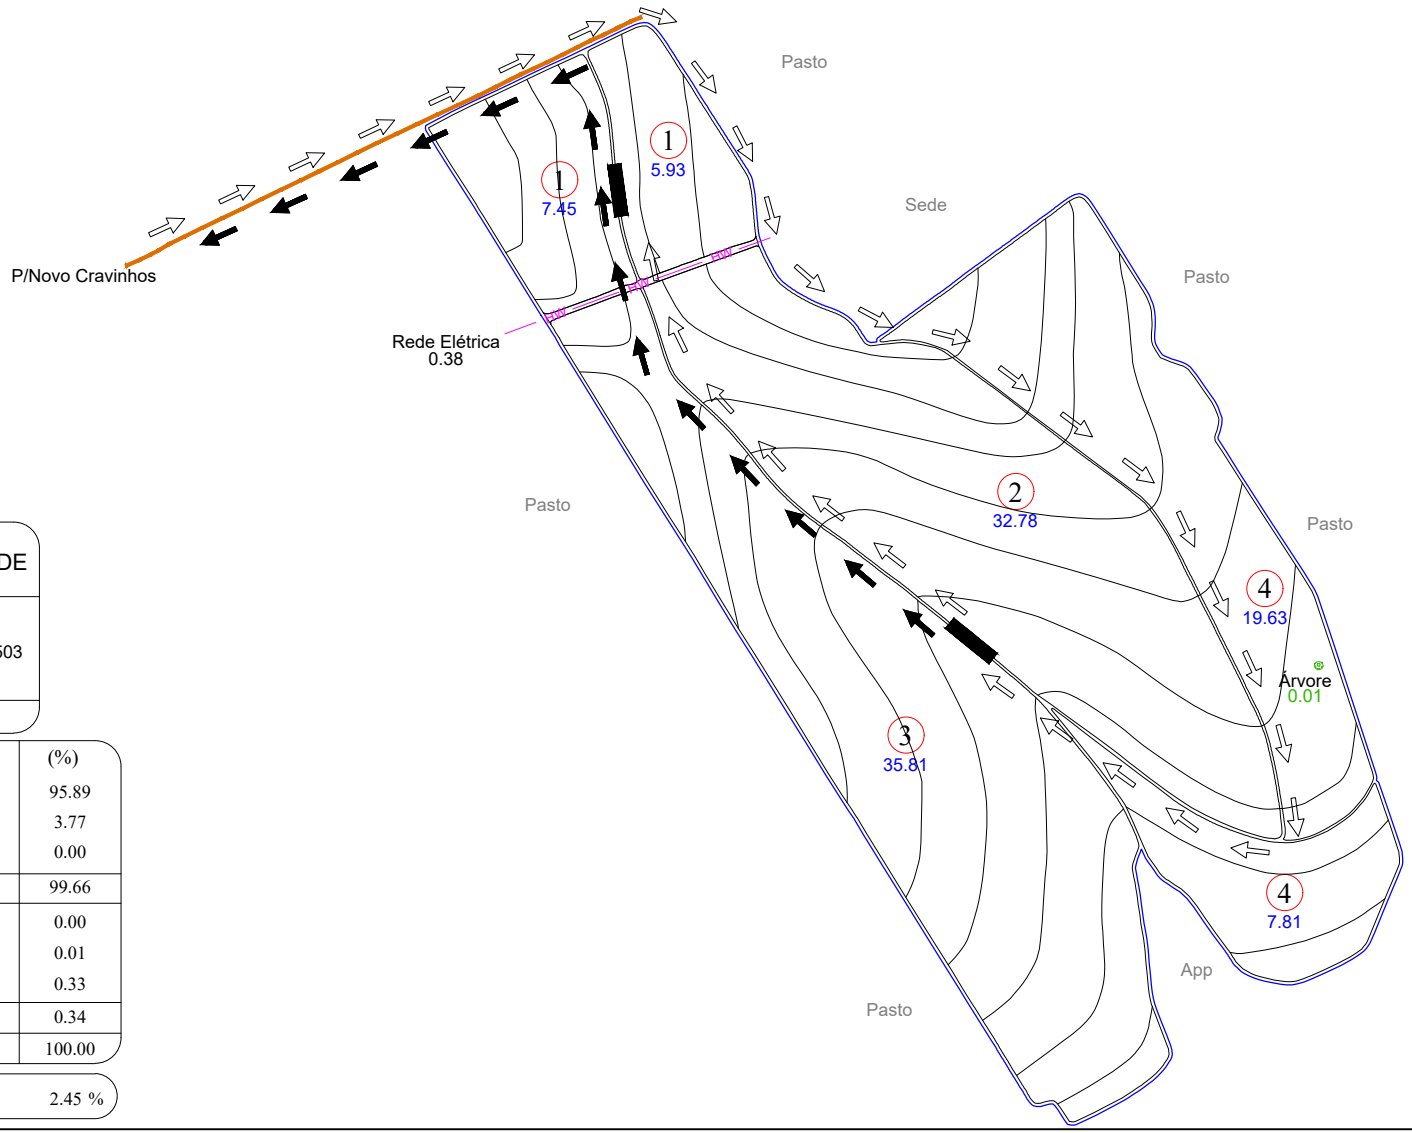

Nº TAL.	DATA PL.	ÁREA (ha)	VARIEDADE
1	06/2025	13.38	IACSP01-5503
2		32.78	
3	05/2025	35.81	
4	06/2025	27.44	
TOTAL PLANTIO		109.41	

ÁREAS	(ha)	(%)
PLANTIO	109.41	95.89
CARREADORES	4.30	3.77
OUTROS	0.00	0.00
SUB TOTAL AGRICULTÁVEL	113.71	99.66
AP.P.	0.00	0.00
ÁRVORES	0.01	0.01
OUTROS	0.38	0.33
SUB TOTAL NÃO AGRICULT.	0.39	0.34
ÁREA TOTAL	114.10	100.00


C. NÍVEL: 12156.51 m/l 2.80 ha 2.45 %

ESCALA: 1: 12.000

LEGENDA
- FAZENDA
- TALHÃO
- REDE ELÉTRICA
- TERRAÇO BASE LARGA
- TERRAÇO EMBUTIDO
- VAZIO
- CARREGADO

ESPAÇAMENTO: 1.50 x 1.50
TIRO MÉDIO ESTIMADO: 317.39 m
D.V: 5.81 %

CROQUI DE ACESSO

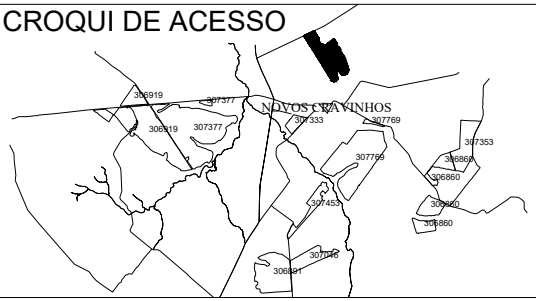

SÍTIO BOM JESUS

PROPRIETÁRIO: MARIANGELA RAMOS E OUTROS
COMPRADOR: CLEALCO
MUNICÍPIO: POMPÉIA - SP

DISTÂNCIAS (km):
UNID. I - Asfalto: 83.00 Terra.: 2.00
UNID.I I - Asfalto: 23.00 Terra.: 2.00

COORDENADAS: E(X): 592030.77 N(Y): 7570080.12
LAT: -21°58'16.7368" LONG: -50°6'31.0113"
CLEALCO - AÇÚCAR E ALCOOL S/A - DEPARTAMENTO DE GEOTECNOLOGIA

LEVANTAMENTO VIA:
SATÉLITE
GPS / VANT
GOOGLE

UNIDADE: II
PARTE: A/A
FUNDO AGRÍCOLA: 306800

M:\01-Mapa de safra\Mapas Atualizados\Terceiro\306800 - Sítio Bom Jesus (Milton Zanchettin)\306800 - Sítio Bom Jesus (Milton Zanchettin).dwg

Bruno Gamboa 19/01/26