ZONA	Nº TAL.	DATA PL.	ÁREA (ha)	VAR.
999	1	07/2021	42.91	RB867515 RB975242
	2		30.23	
	3		35.39	
	4		23.43	
TOTAL PLANTIO			131.96	--------

ÁREAS	(ha)	(%)
PLANTIO	131.96	96.28
CARREADORES	5.06	3.69
OUTROS	0.00	0.00
SUB TOTAL AGRICULTÁVEL	137.02	99.97
AP.P.	0.00	0.00
MATA	0.00	0.00
OUTROS	0.04	0.03
SUB TOTAL NÃO AGRICULT.	0.04	0.03
ÁREA TOTAL	137.06	100.00


C. NÍVEL: 16086.08 m/l 3.70 ha 2.70 %

LEGENDA


- FAZENDA
- TALHÃO
- CURVA DE NÍVEL
- CARREADOR
- CONFRONTANTE
- REDE ELÉTRICA
- TRAJETO VAZIO
- TRAJETO CARREGADO

PLANTIO MANUAL - ESPAÇAMENTO: 1.50 X 1.50
TIRO MÉDIO ESTIMADO: 307.78 m

Clealco
Açúcar, Etanol e Energia

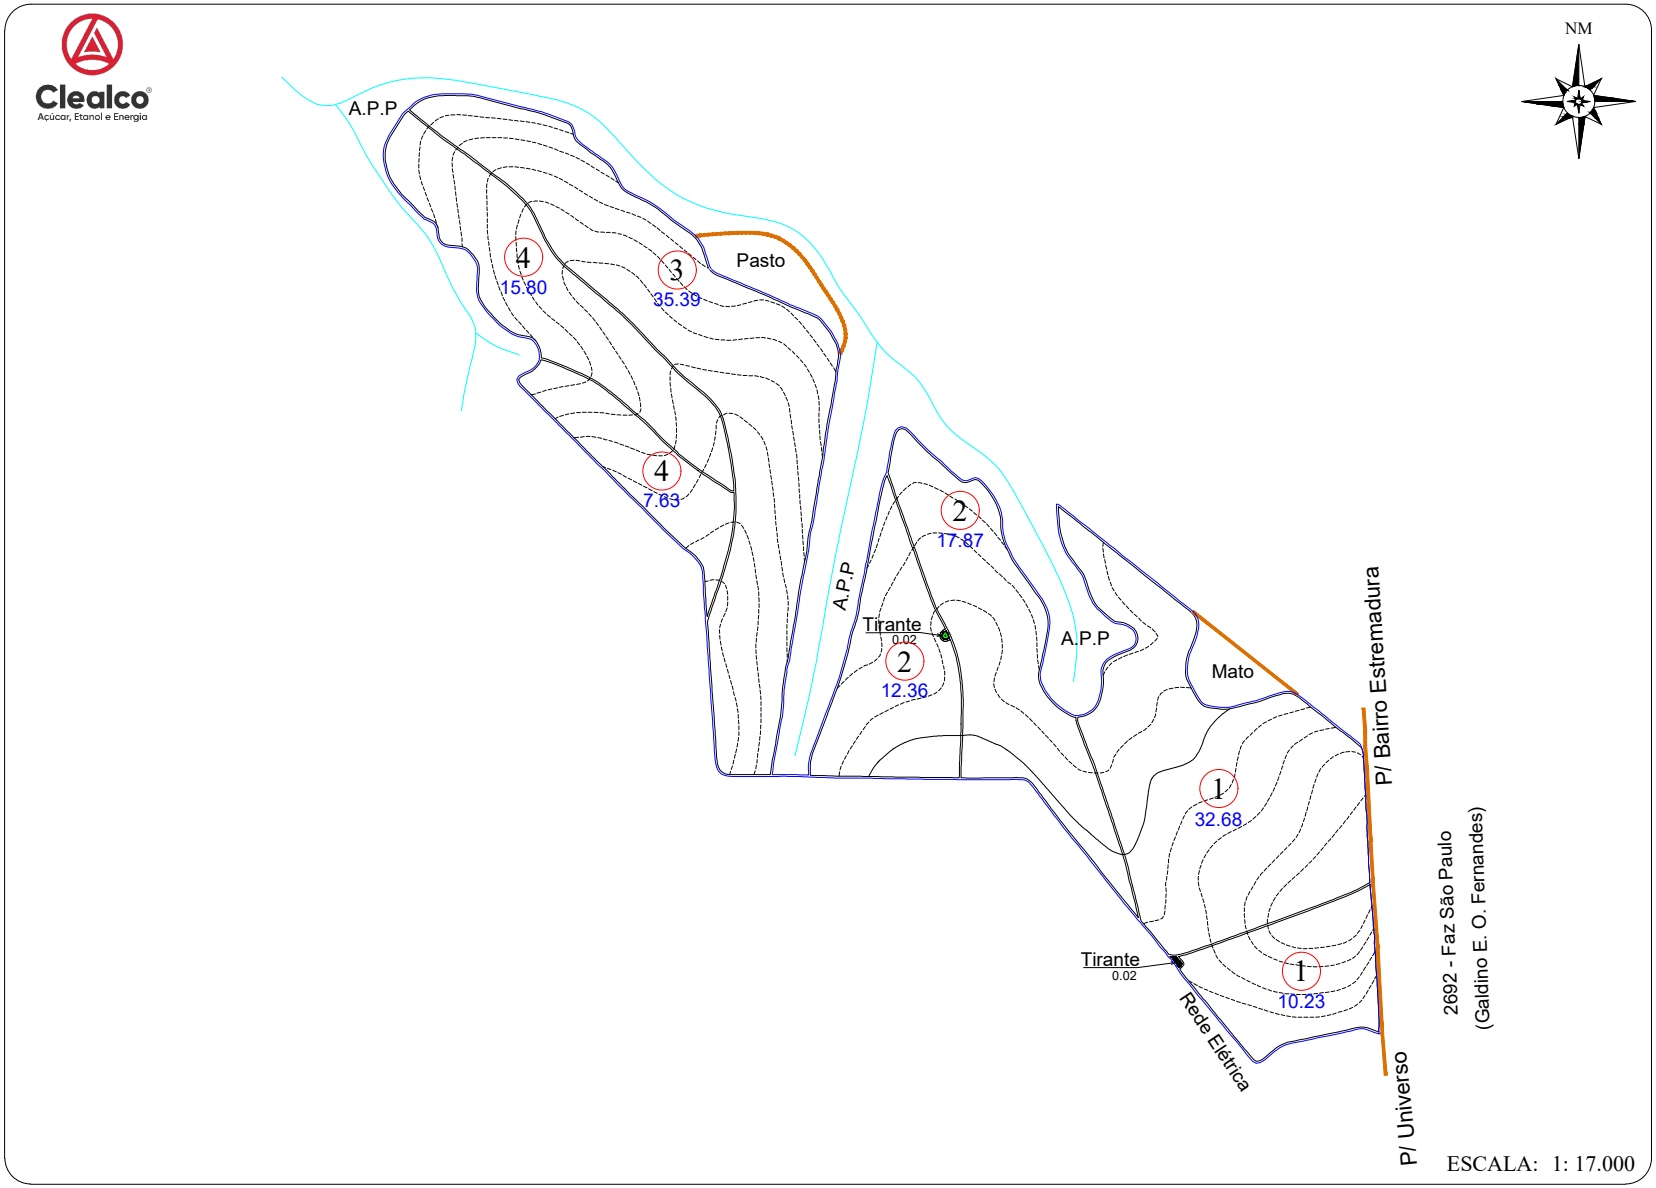

CROQUI DE ACESSO

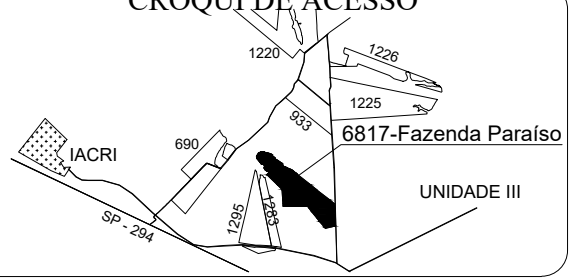

FAZENDA PARAISO

PROPRIETÁRIO: CLAUDEMIR STEFANELI
COMPRADOR: CLEALCO S/A
MUNICÍPIO: IACRI

DISTÂNCIAS (km):
UNID. I - Asfalto: 67.50 Terra.: 2.00
UNID.I I - Asfalto: 29.00 Terra.: 8.30
UNID. III -Asfalto: 92.00 Terra.: 2.00

COORDENADAS: E(X): 539.515,34 N(Y): 7.5809.14,23
LAT: 21° 52' 31,47375" LONG: 50° 37' 03,04324"

CLEALCO - AÇÚCAR E ALCOOL S/A - DEPARTAMENTO DE TOPOGRAFIA

UNIDADE: I
PARTE: A/A
FUNDO AGRÍCOLA: 306817

M:\01-Mapa de safra\Mapas Atualizados\Terceiro\306817 - Fazenda Paraíso (Claudemir Stefanelli)\306817 - Fazenda Paraíso (Claudemir Stefanelli).dwg

Bruno Gamboa 11/03/25