ZONA D.V	Nº TAL.	DATA PL.	ÁREA (ha)	VAR.
999 6.16%	1	07/2021	38.33	CTC 04
TOTAL PLANTIO			38.33	--------


ÁREAS	(ha)	(%)
PLANTIO	38.33	95.80
CARREADORES	1.68	4.20
OUTROS	0.00	0.00
SUB TOTAL AGRICULTÁVEL	40.01	100.00
AP.P.	0.00	0.00
MATA	0.00	0.00
OUTROS	0.00	0.00
SUB TOTAL NÃO AGRICULT.	0.00	0.00
ÁREA TOTAL	40.01	100.00

C. NÍVEL: 4327.75 m/l 1.00 ha 2.49 %


LEGENDA

- FAZENDA
- TALHÃO
- CURVA DE NÍVEL
- CARREADOR
- CONFRONTANTE
- REDE ELÉTRICA
- TRAJETO VAZIO
- TRAJETO CARREGADO

PLANTIO MANUAL - ESPAÇAMENTO: 1.50 X 1.50
TIRO MÉDIO ESTIMADO: 394.48 m

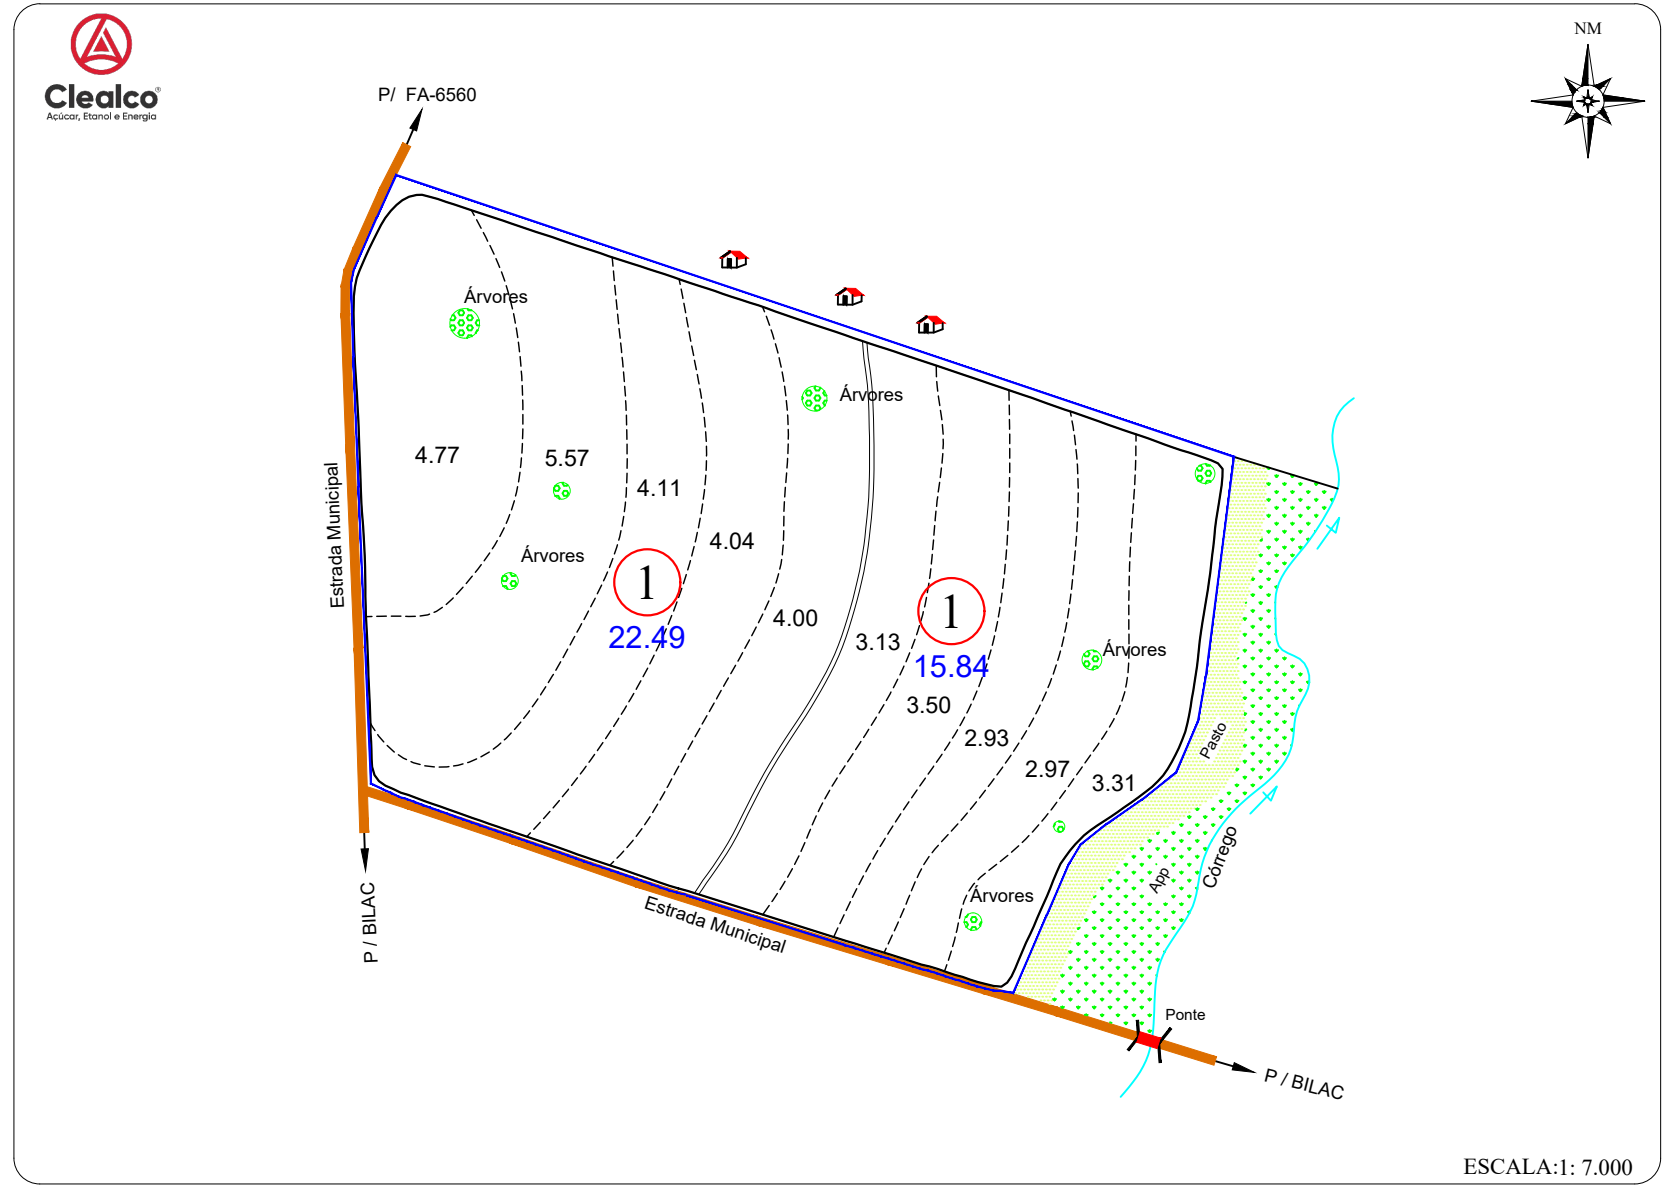

ESCALA:1: 7.000

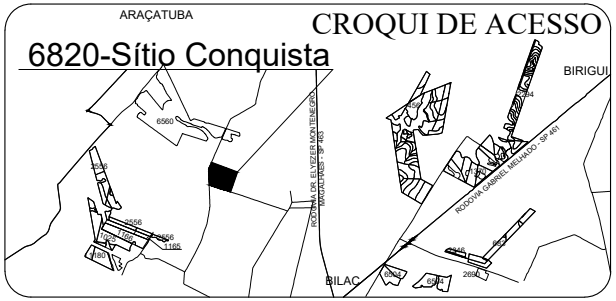

SÍTIO DA CONQUISTA

PROPRIETÁRIO: LUIS CARLOS GENARI E OUTROS
COMPRADOR: CLEALCO S/A
MUNICÍPIO: BILAC-SP

DISTÂNCIAS (km):
UNID. I - Asfalto: 24.30 Terra.: 8.30
UNID.I I - Asfalto: 80.10 Terra.: 8.30
UNID. III -Asfalto: 65.00 Terra.: 5.00

COORDENADAS: E(X): 553.113 N(Y): 7.638.914
LAT: 21°21'3.7416" LONG: 50°29'15.8596"

CLEALCO - AÇÚCAR E ALCOOL S/A - DEPARTAMENTO DE TOPOGRAFIA

UNIDADE: I
PARTE: A/A
FUNDO AGRÍCOLA: 306820