Clealco
Açúcar, Etanol e Energia

LEGENDA


- FAZENDA
- TALHÃO
- REDE ELÉTRICA
- TERRAÇO BASE LARGA
- TERRAÇO EMBUTIDO
- (P.O.A) PATIO DE OPERAÇÃO

ESPAÇAMENTO: 1.50 x 1.50
TIRO MÉDIO ESTIMADO: 000.00 m
D.V: 2.76 %

ÁREAS	(ha)	(%)
PLANTIO	1168.35	96.26
CARREADORES	41.32	3.40
OUTROS	0.00	0.00
SUB TOTAL AGRICULTÁVEL	1209.67	99.67
AP.P.	0.00	0.00
ÁRVORES	3.59	0.30
OUTROS	0.44	0.04
SUB TOTAL NÃO AGRICULT.	4.03	0.33
ÁREA TOTAL	1213.70	100.00


C. NÍVEL: 78722.94 m/l 18.11 ha 1.49 %

Nº TAL.	DATA PL.	ÁREA (ha)	VARIEDADE
1	05/2025	32.84	RB 075322
2		33.23	
3		13.08	RB 985033
4		13.56	
5		11.26	RB 075322
6		39.54	
7		30.49	
8		1.22	
9		25.01	RB 985033
10		19.54	RB 867515
11		6.63	
12	2026	46.39	REFORMA
13	04/2023	42.11	RB 867515
14		26.98	
15	2026	21.50	REFORMA
16		29.64	
17	04/2021	33.39	RB 855035
18		37.67	
19	04/2020	41.72	
20		26.77	CTC 9001
21	04/2023	51.70	RB 867515
22		43.80	RB 966928
23	04/2024	41.58	RB 975033
24		12.12	
25	04/2021	45.11	RB 975242
26		25.45	
27		27.87	RB 966928
28		47.64	
29		52.83	RB 975242
30	04/2022	33.73	
31	04/2019	42.30	
32	05/2026	52.47	DIVERSAS
33		54.63	
34		37.05	
35		33.59	
36		33.91	
TOTAL PLANTIO		1168.35	

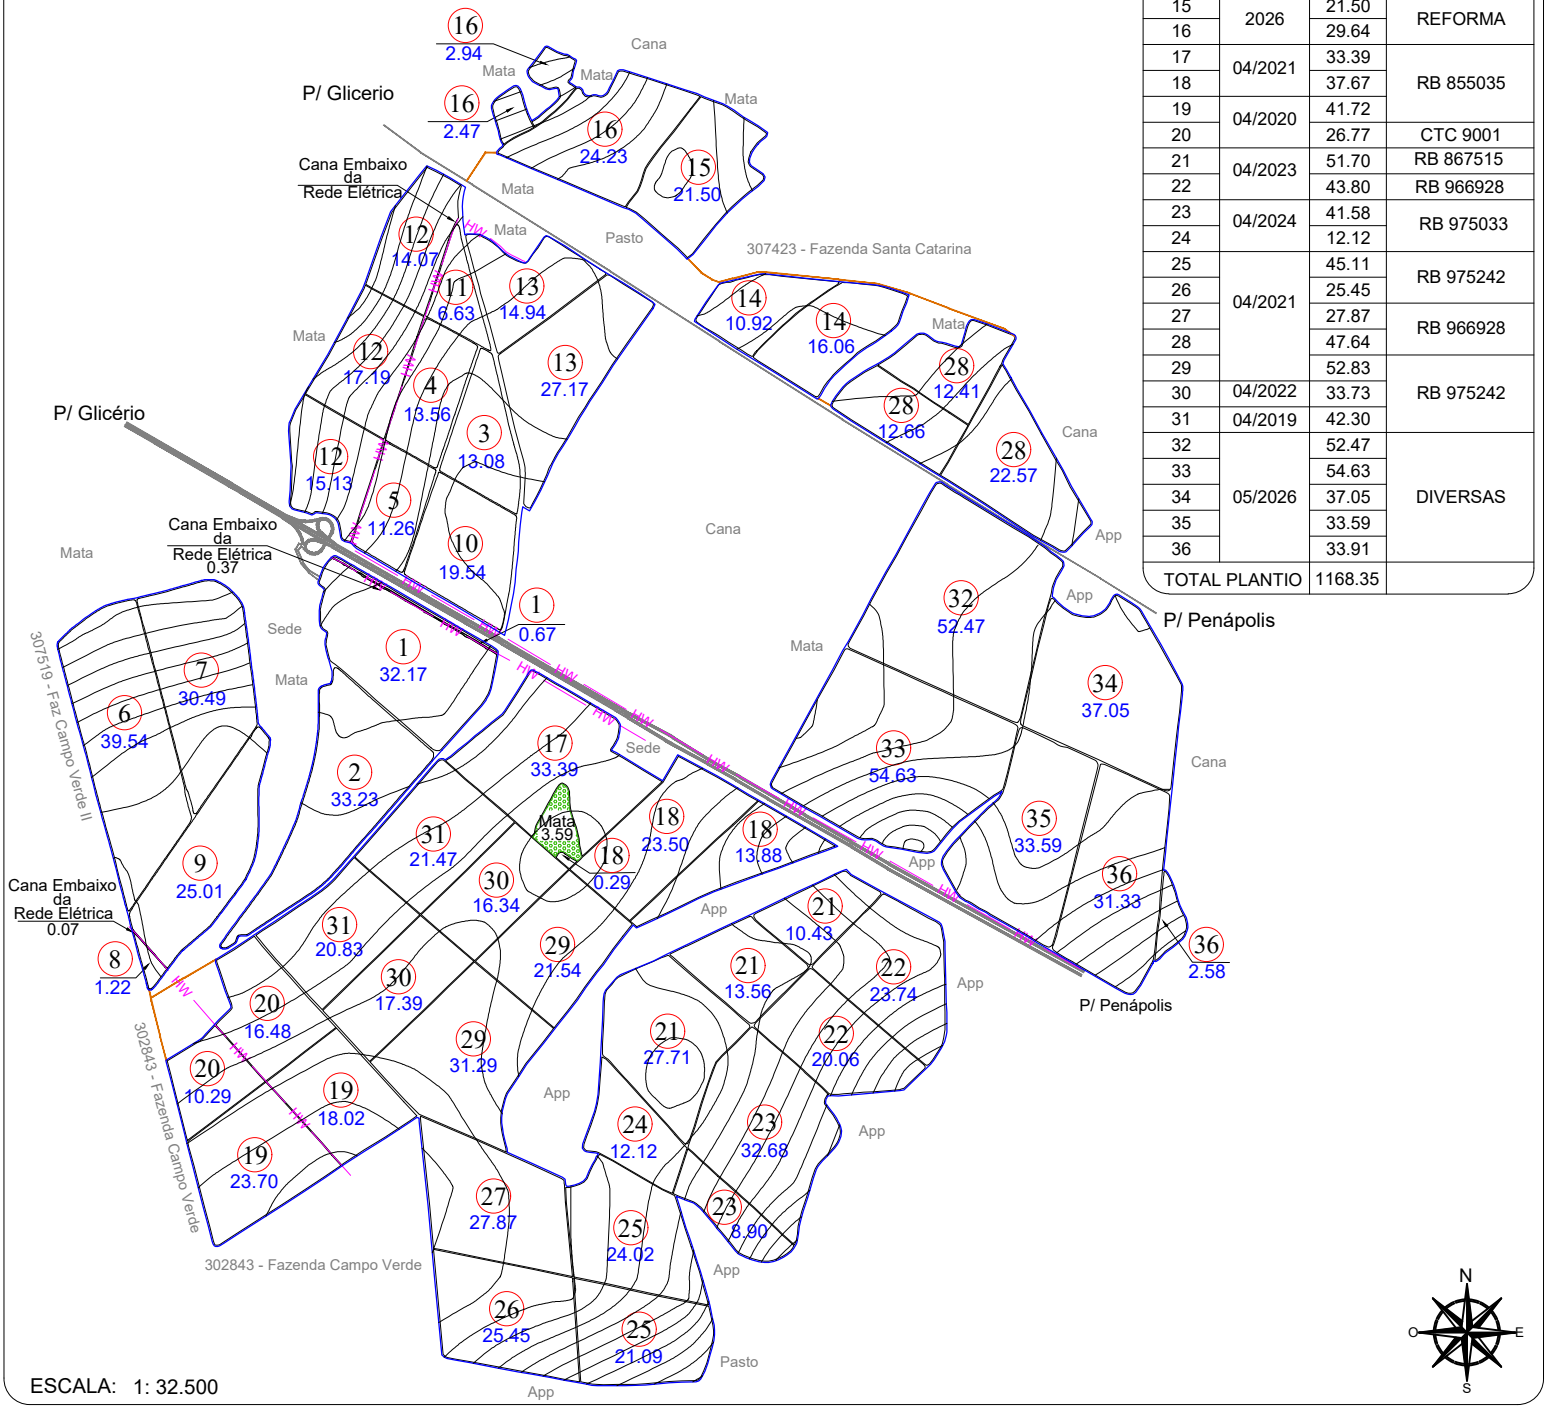

ESCALA: 1: 32.500

CROQUI DE ACESSO

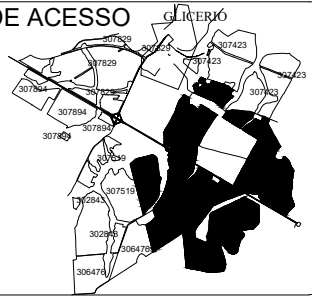

FAZENDA SÃO JOÃO

PROPRIETÁRIO: MARCELO CHAMIE HOUMSI
COMPRADOR: CLEALCO
MUNICÍPIO: COROADOS - SP

DISTÂNCIAS (km):
UNID. I - Asfalto: 31.00 Terra.: 4.47
UNID.I I - Asfalto: 67.50 Terra.: 2.00

COORDENADAS: E(X): 583658.15 N(Y): 7626812.28
LAT: -21°27'33.1889" LONG: -50°11'33.2443"

CLEALCO - AÇÚCAR E ALCOOL S/A - DEPARTAMENTO DE GEOTECNOLOGIA

LEVANTAMENTO VIA:
SATÉLITE
GPS / VANT
GOOGLE

UNIDADE: I
PARTE: A/B
FUNDO AGRÍCOLA: 306829

M:\01-Mapa de safra\Mapas Atualizados\Terceiro\306829 - Fazenda São João (Marcelo Chamie Houmsi)\306829 A - Fazenda São João (Marcelo Chamie Houmsi).dwg

Bruno Gamboa 14/09/26