
Clealco
Açúcar, Etanol e Energia

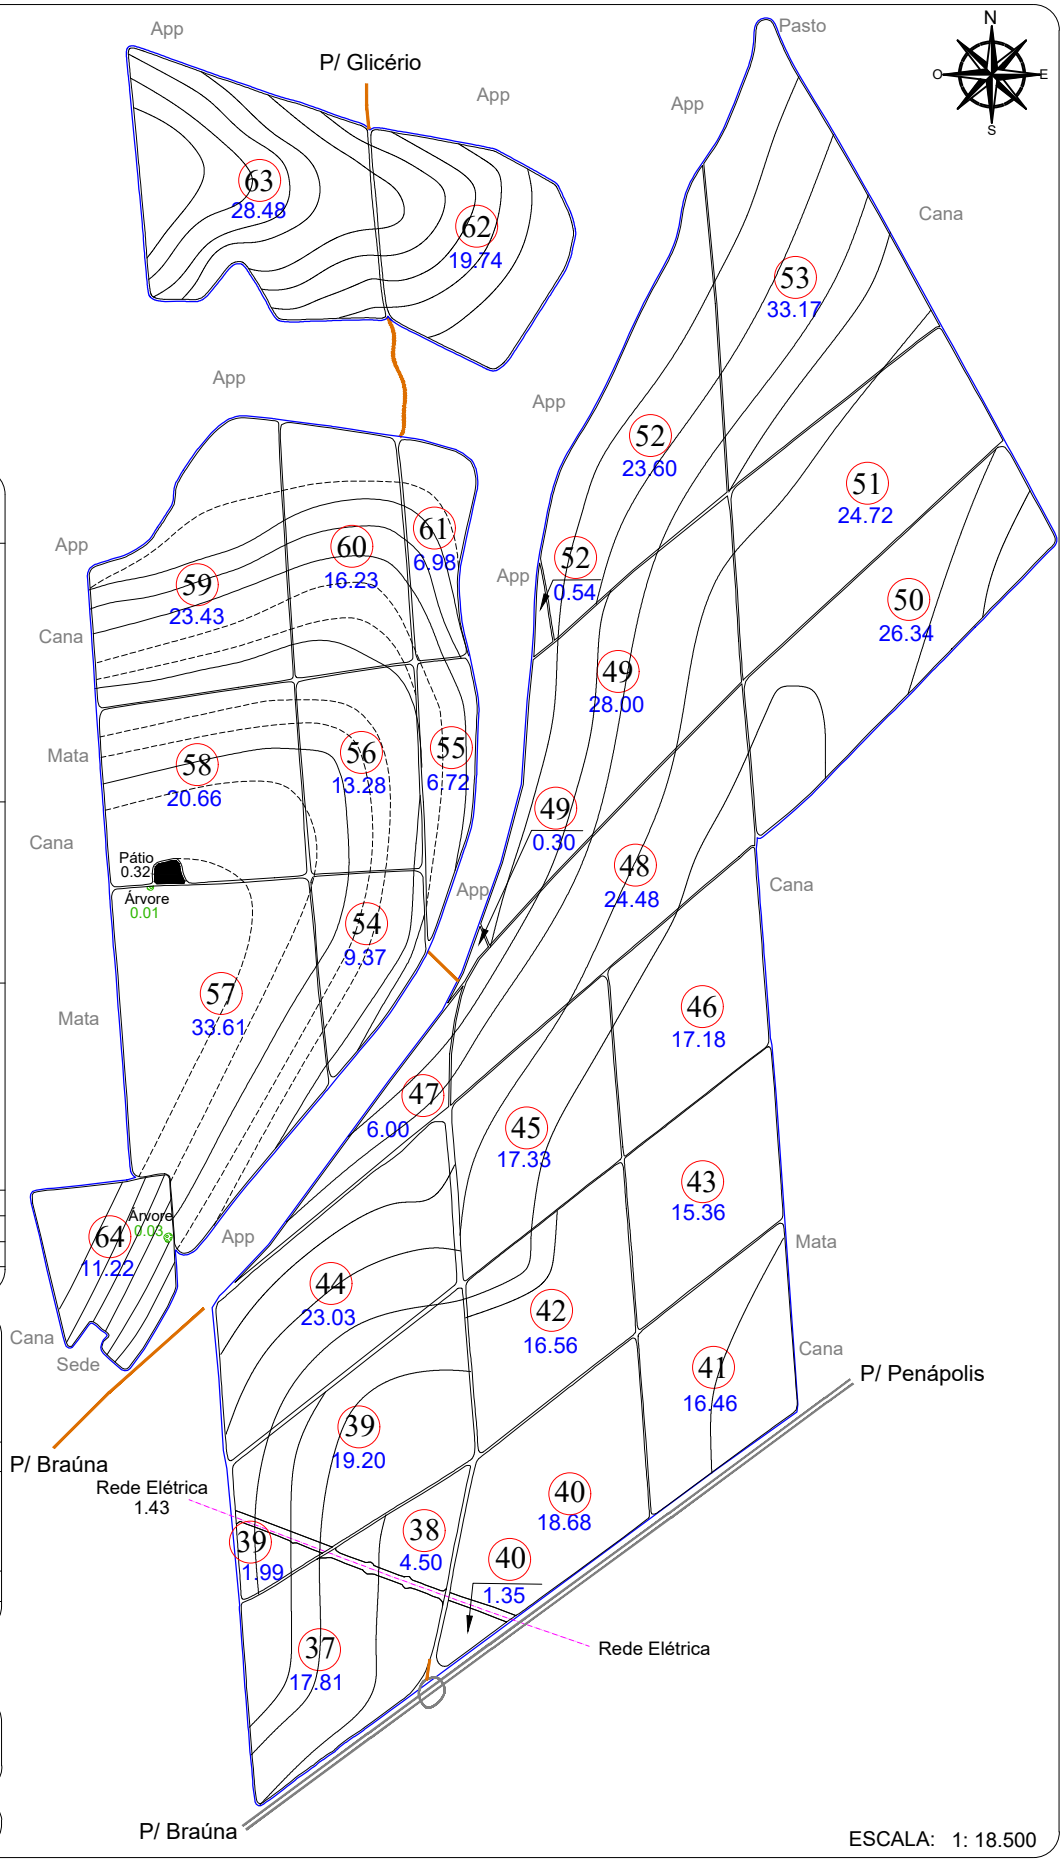

ZONA	Nº TAL.	DATA PL.	ÁREA (ha)	VAR.
999	37	04/2023	17.81	RB 975033
	38		4.50	
	39	05/2024	21.19	
	40		20.03	
	41		16.46	
	42		16.56	
	43		15.36	
	44		23.03	
	45	04/2023	17.33	
	46		17.18	
	47	04/2022	6.00	RB 867515
	48		24.48	
	49		28.30	
	50	04/2023	26.34	
	51		24.72	
	52	04/2022	24.14	
	53		33.17	
	54	05/2026	9.37	DIVERSAS
	55		6.72	
	56		13.28	
	57		33.61	
	58		20.66	
	59		23.43	
	60		16.23	
	61		6.98	
	62	04/2025	19.74	RB 966928
	63		28.48	RB 985033
	64	04/2023	11.22	RB 975033
TOTAL PLANTIO			526.32	--------

ÁREAS	(ha)	(%)
PLANTIO	526.32	96.35
CARREADORES	18.14	3.32
OUTROS	0.00	0.00
SUB TOTAL AGRICULTÁVEL	544.46	99.67
AP.P.	0.00	0.00
ÁRVORES	0.04	0.01
OUTROS	1.75	0.32
SUB TOTAL NÃO AGRICULT.	1.79	0.33
ÁREA TOTAL	546.25	100.00

C. NÍVEL: 34134.81 m/l 7.85 ha 1.44 %


LEGENDA

- FAZENDA
- TALHÃO
- REDE ELÉTRICA
- TERRAÇO BASE LARGA
- TERRAÇO EMBUTIDO
- (P.O.A) PATIO DE OPERAÇÃO

ESPAÇAMENTO: 1.50 x 1.50
TIRO MÉDIO ESTIMADO: 521.50 m
D.V: 2.76 %

ESCALA: 1: 18.500

CROQUI DE ACESSO

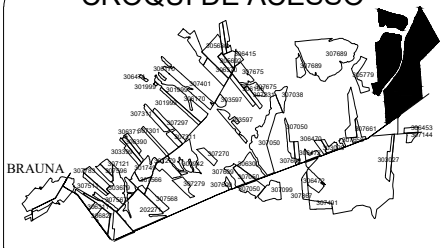

FAZENDA SÃO JOÃO

PROPRIETÁRIO: MARCELO CHAMIE HOUMSI
COMPRADOR: CLEALCO
MUNICÍPIO: COROADOS - SP

DISTÂNCIAS (km):
UNID. I - Asfalto: 31.00 Terra.: 4.47
UNID.I I - Asfalto: 67.50 Terra.: 2.00

COORDENADAS: E(X): 583658.15 N(Y): 7626812.28
LAT: -21°27'33.1889" LONG: -50°11'33.2443"

CLEALCO - AÇÚCAR E ALCOOL S/A - DEPARTAMENTO DE GEOTECNOLOGIA

LEVANTAMENTO VIA:
- SATÉLITE
- GPS / VANT
- GOOGLE

UNIDADE: I
PARTE: B/B
FUNDO AGRÍCOLA: 306829

M:\01-Mapa de safra\Mapas Atualizados\Terceiro\306829 - Fazenda São João (Marcelo Chamie Houmsi)\306829 B - Fazenda São João (Marcelo Chamie Houmsi).dwg

Bruno Gamboa 28/09/26