
Clealco
Açúcar, Etanol e Energia

ZONA	Nº TAL.	DATA PL.	ÁREA (ha)	VARIEDADE
999	1	04/2020	49.52	RB96 5242
	2		38.18	RB96 5201
	3		45.86	
TOTAL PLANTIO			133.56	

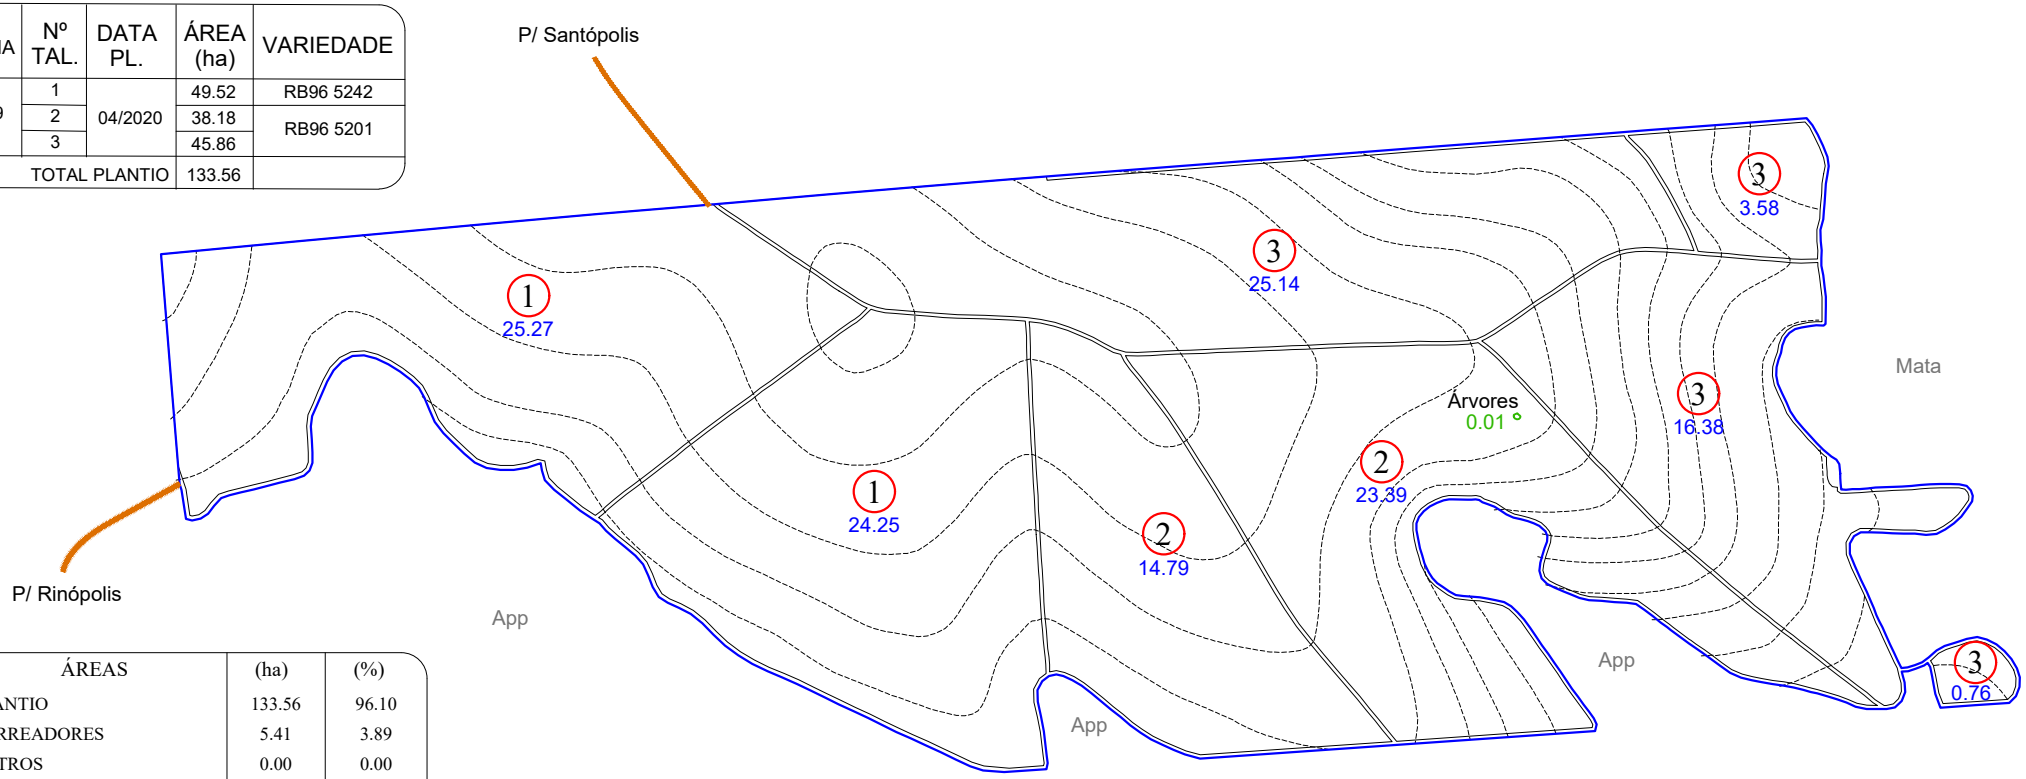

ÁREAS	(ha)	(%)
PLANTIO	133.56	96.10
CARREADORES	5.41	3.89
OUTROS	0.00	0.00
SUB TOTAL AGRICULTÁVEL	138.97	99.99
AP.P.	0.00	0.00
ÁRVORES	0.01	0.01
OUTROS	0.00	0.00
SUB TOTAL NÃO AGRICULT.	0.01	0.01
ÁREA TOTAL	138.98	100.00


C. NÍVEL: 17294.41 m/l 3.98 ha 2.86 %

ESCALA: 1: 10.500

LEGENDA
- FAZENDA
- TALHÃO
- REDE ELÉTRICA
- TERRAÇO BASE LARGA
- TERRAÇO EMBUTIDO
- VAZIO
- CARREGADO

ESPAÇAMENTO: 1.50 x 1.50
TIRO MÉDIO ESTIMADO: 255.30 m
D.V: 5.39 %

CROQUI DE ACESSO

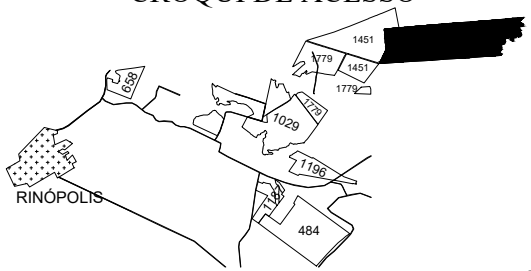

FAZENDA JARDIM 3

PROPRIETÁRIO: VILMAR JOSÉ GASTALDI
COMPRADOR: CLEALCO
MUNICÍPIO: RINÓPOLIS - SP

DISTÂNCIAS (km):
UNID. I - Asfalto: 30.50 Terra.: 2.50
UNID.I I - Asfalto: 67.50 Terra.: 2.50

COORDENADAS: E(X): 538076.82 N(Y): 7599967.22
LAT: -21°42'11.8970" LONG: -50°37'54.7526"
CLEALCO - AÇÚCAR E ALCOOL S/A - DEPARTAMENTO DE GEOTECNOLOGIA

LEVANTAMENTO VIA:
SATÉLITE
GPS / VANT
GOOGLE

UNIDADE: I
PARTE: A/A
FUNDO AGRÍCOLA: 306834

M:\01-Mapa de safra\Mapas Atualizados\Terceiro\306834 - Fazenda Jardim III (Vilmar José Gastaldi)\306834 - Fazenda Jardim III (Vilmar José Gastaldi).dwg

Peterson Santos 12/08/2026