ZONA DV	Nº TAL.	DATA PL.	ÁREA (ha)	VARIEDADE
999 5.00 %	1	04/2020	29.03	CTC 04
	2		24.43	RB 965201
	3		39.15	
TOTAL PLANTIO			92.61	--------

ÁREAS	(ha)	(%)
PLANTIO	92.61	94.17
CARREADORES	5.73	5.83
OUTROS	0.00	0.00
SUB TOTAL AGRICULTÁVEL	98.34	100.00
AP.P.	0.00	0.00
ÁRVORES	0.00	0.00
OUTROS	0.00	0.00
SUB TOTAL NÃO AGRICULT.	0.00	0.00
ÁREA TOTAL	98.34	100.00

C. NÍVEL: 9790.43 m/l 2.25 ha 2.29 %


LEGENDA

- FAZENDA
- TALHÃO
- CURVA DE NÍVEL
- CARREADOR
- CONFRONTANTE
- REDE ELÉTRICA
- TRAJETO VAZIO
- TRAJETO CARREGADO

PLANTIO MANUAL - ESPAÇAMENTO: 1.50 X 1.50
TIRO MÉDIO ESTIMADO: 248.35 m


Clealco
Açúcar, Etanol e Energia

NM

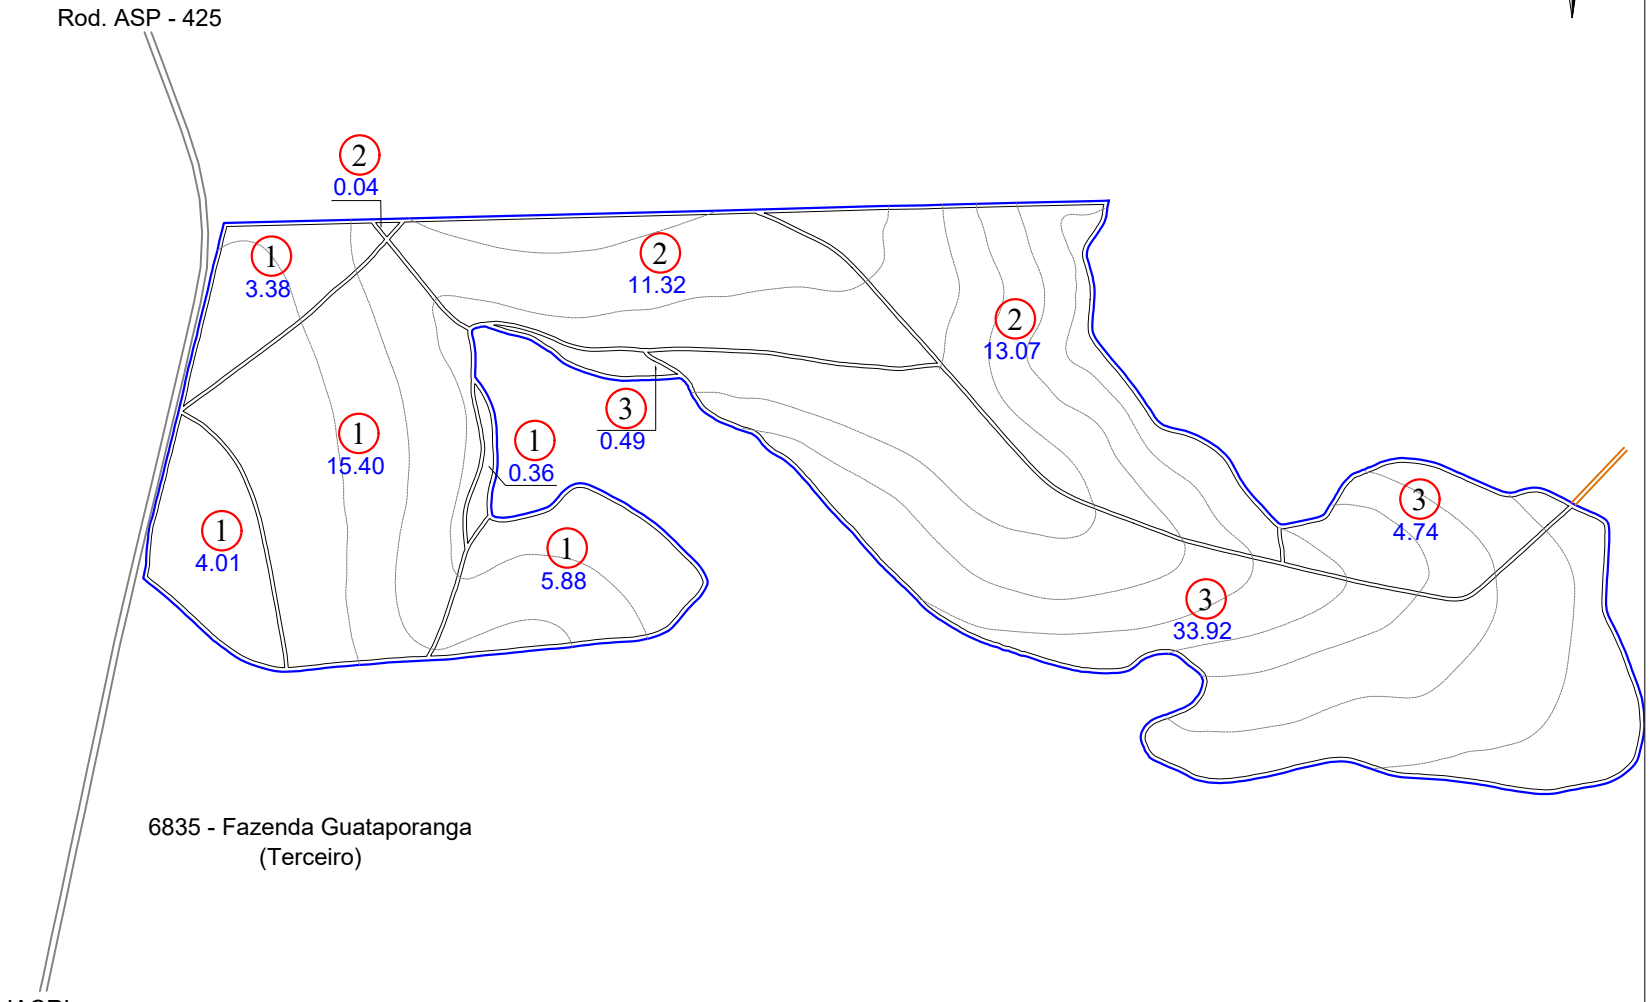

ESCALA: 1: 12.000

CROQUI DE ACESSO

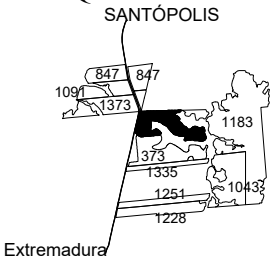

FAZENDA SÃO JOSÉ

PROPRIETÁRIO: VILMAR JOSÉ GASTALDI
COMPRADOR: CLEALCO S/A
MUNICÍPIO: IACRI

DISTÂNCIAS (km):
UNID. I - Asfalto: 26.80 Terra.: 00.00
UNID.I I - Asfalto: 50.00 Terra.: 00.00
UNID. III -Asfalto: 71.00 Terra.: 00.00

COORDENADAS: E(X): 543002.89 N(Y): 7599497.37
LAT: -21°42'26.7735" LONG: -50°35'3.2623"

CLEALCO - AÇÚCAR E ALCOOL S/A - DEPARTAMENTO DE TOPOGRAFIA

UNIDADE: I
PARTE: A/A
FUNDO AGRÍCOLA: 306836