ZONA DV	Nº TAL.	DATA PL.	ÁREA (ha)	VARIEDADE
999 3.75 %	1	06/2021	9.25	RB 975201
TOTAL PLANTIO			9.25	--------

ÁREAS	(ha)	(%)
PLANTIO	9.25	96.96
CARREADORES	0.25	2.62
OUTROS	0.00	0.00
SUB TOTAL AGRICULTÁVEL	9.50	99.58
AP.P.	0.00	0.00
MATA	0.04	0.42
OUTROS	0.00	0.00
SUB TOTAL NÃO AGRICULT.	0.04	0.42
ÁREA TOTAL	9.54	100.00

C. NÍVEL:	692.89 m/l	0.16 ha	1.67 %

LEGENDA

━ FAZENDA	━ CONFRONTANTE
━ TALHÃO	-·- REDE ELÉTRICA
▪▪▪▪ CURVA DE NÍVEL	⇾ TRAJETO VAZIO
— CARREADOR	→ TRAJETO CARREGADO

PLANTIO MANUAL - ESPAÇAMENTO: 1.50 X 1.50
TIRO MÉDIO ESTIMADO: 125.49 m

Clealco
Açúcar, Etanol e Energia

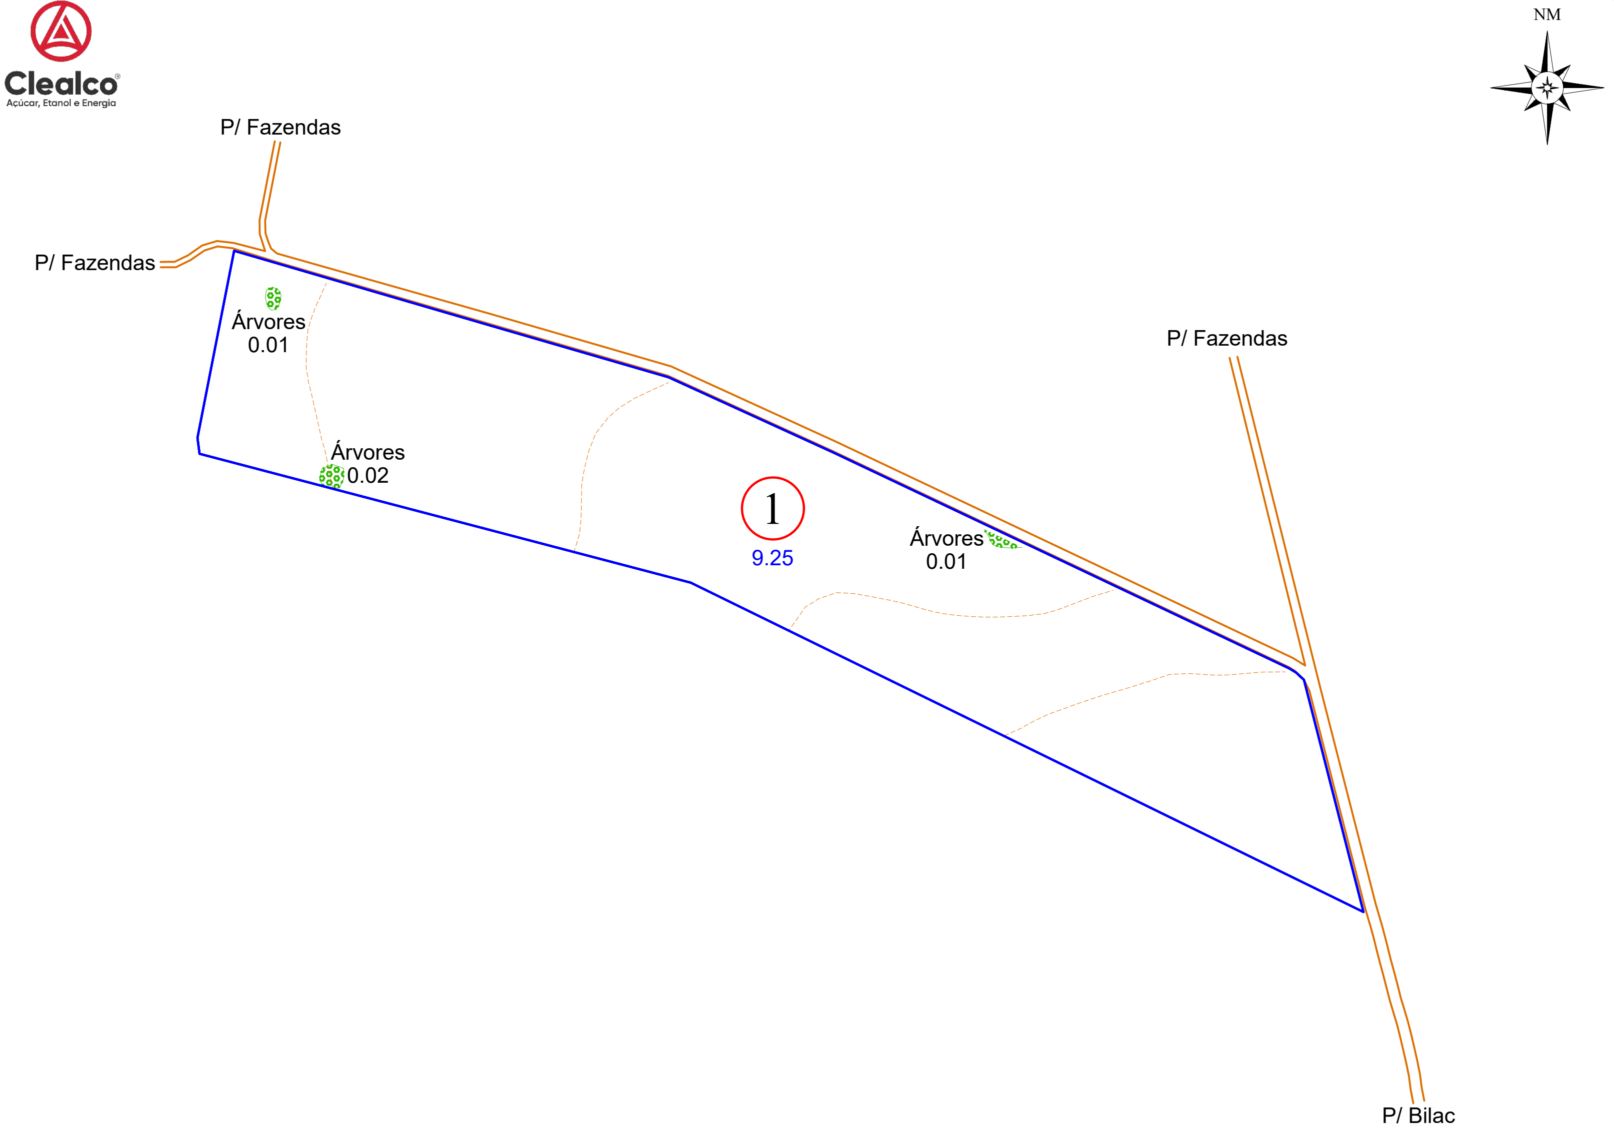

ESCALA: 1: 5.000

CROQUI DE ACESSO

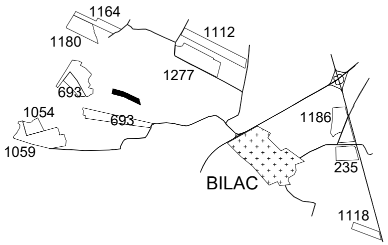

SÍTIO PROSPERIDADE II

PROPRIETÁRIO:	LUIS CARLOS GENARI
ARRENDATÁRIO:	CLEALCO S/A
MUNICÍPIO:	BILAC

DISTÂNCIAS (km):

	Asfalto:		Terra.:	
UNID. I -	Asfalto:	26.00	Terra.:	3.50
UNID.I I -	Asfalto:	81.50	Terra.:	3.50
UNID. III -	Asfalto:	68.00	Terra.:	3.50

COORDENADAS: E(X): 549837 N(Y): 7634388
LAT: 21°23'31,30974" LONG: 50°31'09,14655"

CLEALCO - AÇÚCAR E ALCOOL S/A - DEPARTAMENTO DE TOPOGRAFIA

UNIDADE:
I

PARTE:
A/A

FUNDO AGRÍCOLA:
306847

M:\01-Mapa de safra\Mapas Atualizados\Terceiro\306847 - Sítio Prosperidade II (Luiz Carlos Genari)\306847 - Sítio Prosperidade II (Luiz Carlos Genari).dwg

Fernanda Bezerra 25/10/21