ZONA	Nº TAL.	DATA PL.	ÁREA (ha)	VAR.
999	1	04/2021	47.09	RB 97 5242
	2		49.05	
	3		31.18	
	4		39.12	
	5		51.75	
	6		33.23	
	7		44.73	
	8		41.03	
	9		30.82	
	10		47.09	
	11		29.59	
TOTAL PLANTIO			444.68	--------


ÁREAS	(ha)	(%)
PLANTIO	444.68	91.17
CARREADORES	16.58	3.40
OUTROS	0.00	0.00
SUB TOTAL AGRICULTÁVEL	461.26	94.57
AP.P.	0.00	0.00
MATA	0.79	0.16
OUTROS	25.68	5.27
SUB TOTAL NÃO AGRICULT.	26.47	5.43
ÁREA TOTAL	487.73	100.00

C. NÍVEL: 39381.45 m/l 9.06 ha 1.86 %

LEGENDA


- FAZENDA
- TALHÃO
- CURVA DE NÍVEL
- CARREADOR
- CONFRONTANTE
- REDE ELÉTRICA
- TRAJETO VAZIO
- TRAJETO CARREGADO

PLANTIO MANUAL - ESPAÇAMENTO: 1.50 X 1.50

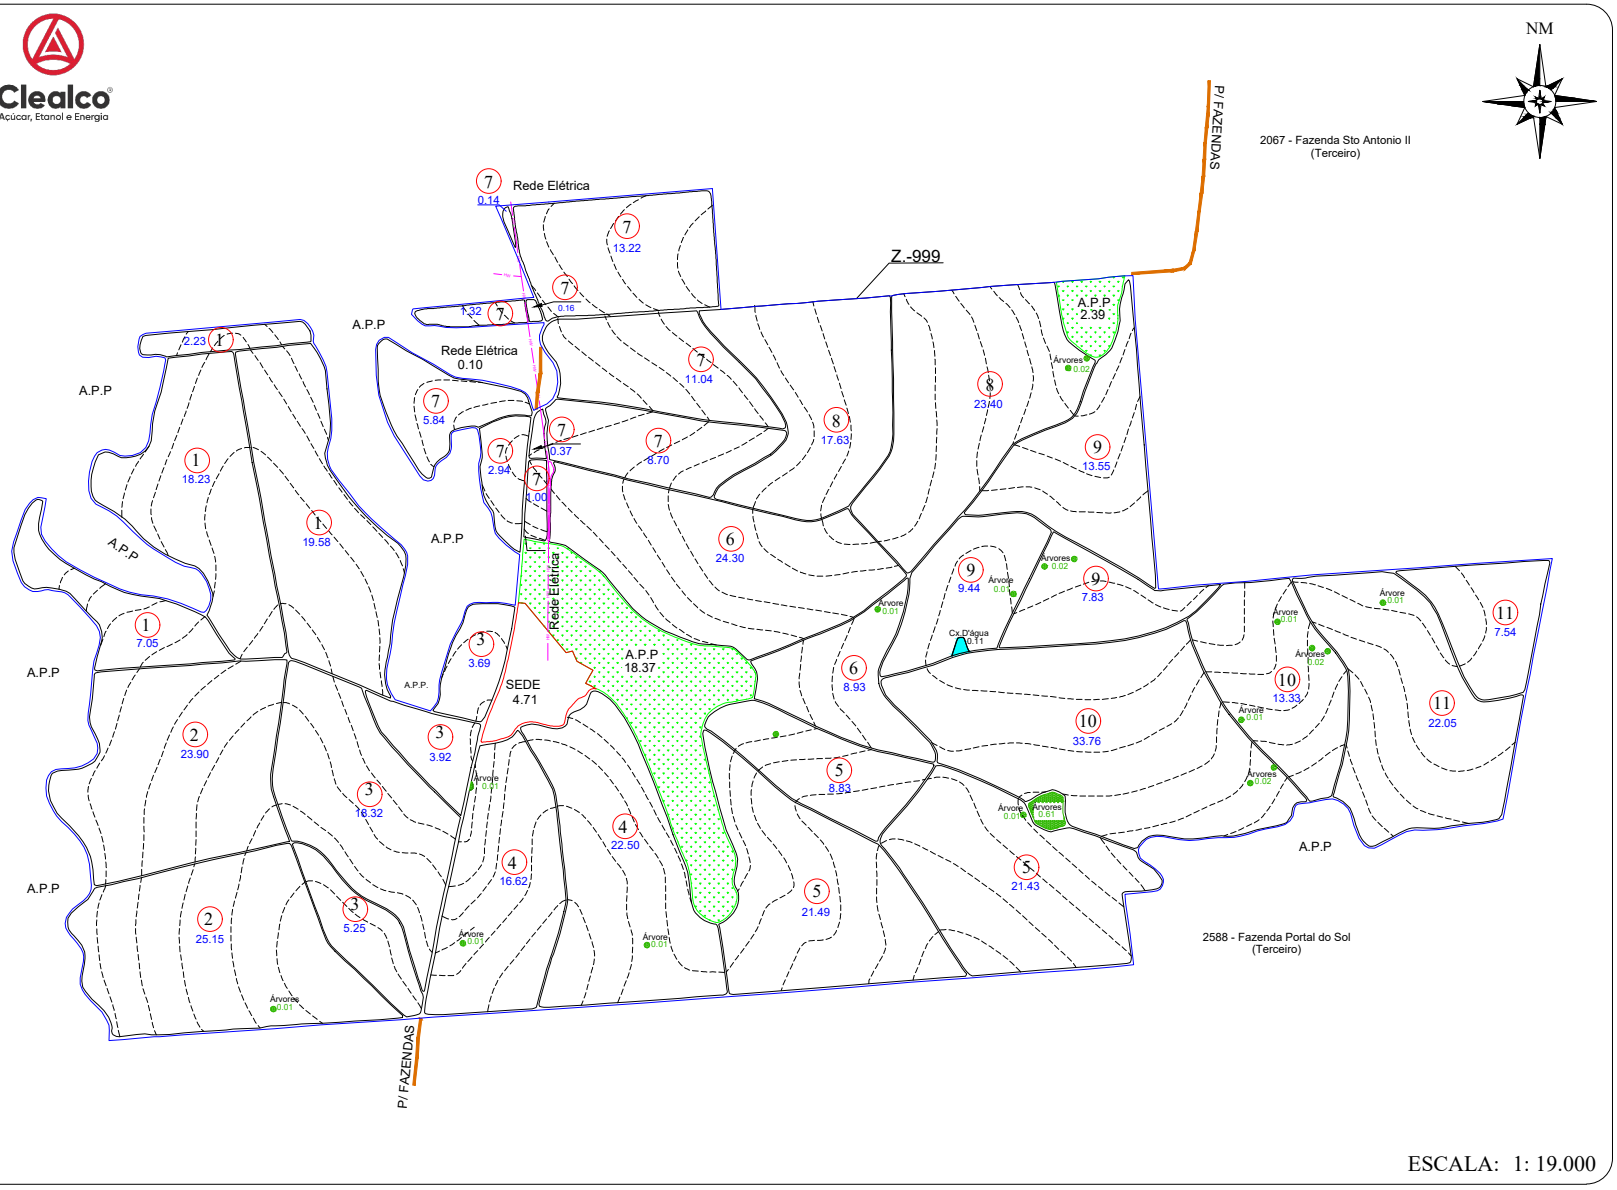

ESCALA: 1: 19.000

CROQUI DE ACESSO

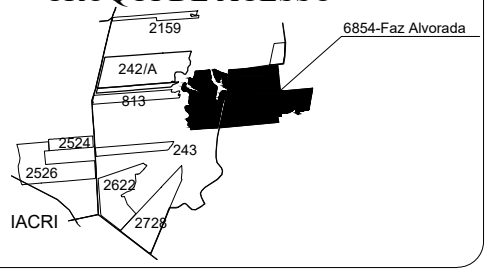

FAZENDA ALVORADASÍTIO

PROPRIETÁRIO: VILMAR JOSÉ GASTALDI
COMPRADOR: CLEALCO S/A
MUNICÍPIO: IACRI

DISTÂNCIAS (km):
UNID. I - Asfalto: 44.10 Terra.: 1.00
UNID.I I - Asfalto: 79.10 Terra.: 1.00
UNID. III -Asfalto: 90.10 Terra.: 1.00

COORDENADAS: E(X): 544.185,97 N(Y): 7.593.324,70
LAT: 21°45'47.4321" LONG: 50°34'21.4918"

CLEALCO - AÇÚCAR E ALCOOL S/A - DEPARTAMENTO DE TOPOGRAFIA

UNIDADE: II
PARTE: A/A
FUNDO AGRÍCOLA: 306854

M:\01-Mapa de safra\Mapas Atualizados\Terceiro\306854 - Fazenda Alvorada (Vilmar José Gastaldi)\306854 - Fazenda Alvorada (Vilmar José Gastaldi).dwg

Pedro Becker 23/08/21