ZONA	Nº TAL.	DATA PL.	ÁREA (ha)	VARIEDADE
999	1	05/2021	5.62	RB96 6928
	2		11.54	
	3		0.79	
	4		3.58	
	5		30.35	
	6		30.07	
TOTAL PLANTIO			81.95	--------


ÁREAS	(ha)	(%)
PLANTIO	81.95	92.55
CARREADORES	6.18	6.98
OUTROS	-	-
SUB TOTAL AGRICULTÁVEL	88.13	99.54
AP.P.	0.40	0.45
ÁRVORE	0.01	0.01
OUTROS	-	-
SUB TOTAL NÃO AGRICULT.	0.41	0.46
ÁREA TOTAL	88.54	100.00

C. NÍVE 13971.68 m/l 3.21 ha 3.63 %


LEGENDA

- FAZENDA
- TALHÃO
- CURVA DE NÍVEL
- CARREADOR
- CONFRONTANTE
- REDE ELÉTRICA
- TRAJETO VAZIO
- TRAJETO CARREGADO

PLANTIO MANUAL - ESPAÇAMENTO: 1.50 X 1.50

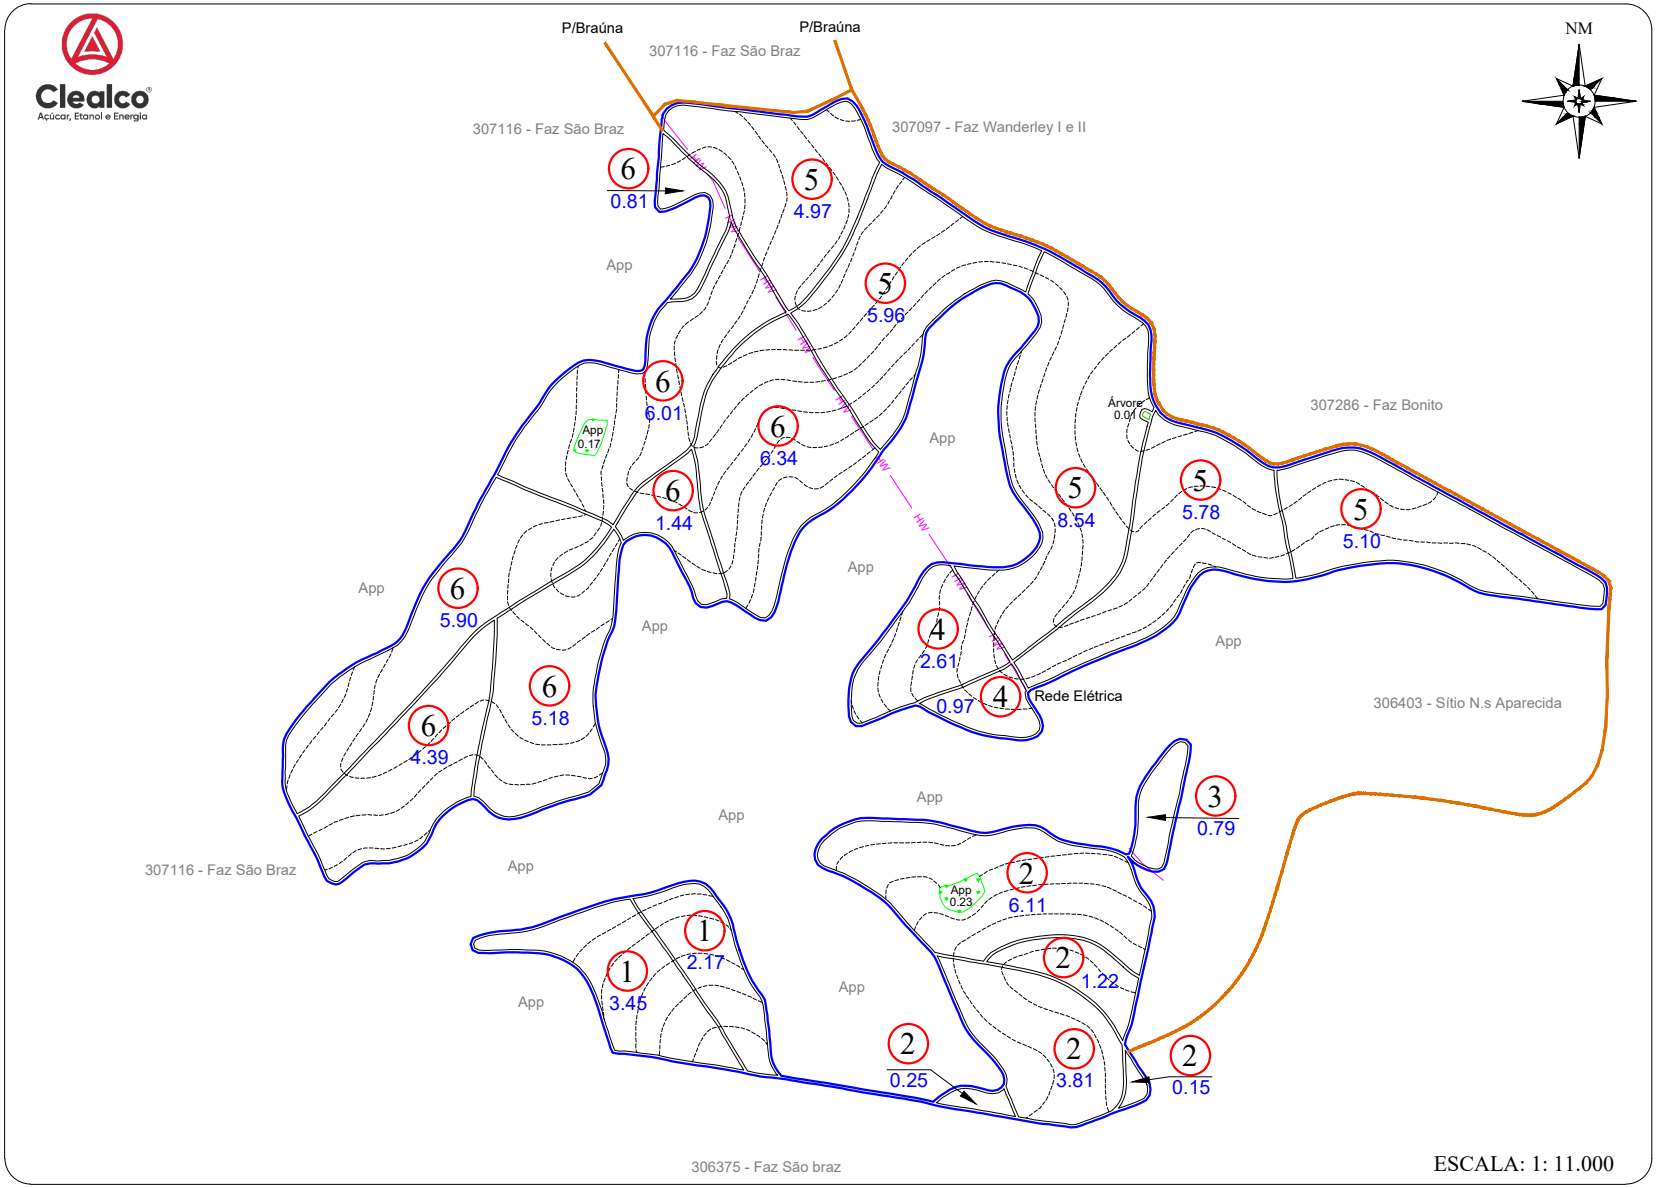

CROQUI DE ACESSO

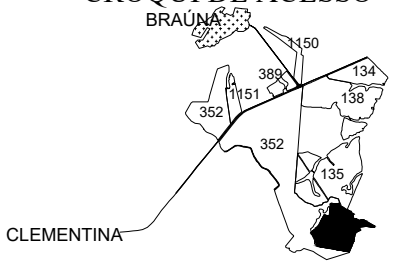

FAZENDA SILVANIA

PROPRIETÁRIO: ESIO NILTON PITTA
ARRENDATÁRIO: CLEALCO S/A
MUNICÍPIO: BRAÚNA

DISTÂNCIAS (km):
UNID. I - Asfalto: 14.50 Terra.: 5.00
UNID.I I - Asfalto: 20.00 Terra.: 18.00
UNID. III -Asfalto: 28.00 Terra.: 5.00

COORDENADAS: E(X): 573848.1653 N(Y): 7616065.8744
LAT: 21º 33' 24,01266" LONG: 50º 17' 12,38927"

CLEALCO - AÇÚCAR E ALCOOL S/A - DEPARTAMENTO DE TOPOGRAFIA

UNIDADE: I
PARTE: A/A
FUNDO AGRÍCOLA: 306863

M:\01-Mapa de safra\Mapas Atualizados\Terceiro\306863 - Fazenda Silvana (Esio Nilton Pitta)\306863 - Fazenda Silvana (Esio Nilton Pitta).dwg

Fernanda Bezerra 01/09/21