ZONA	Nº TAL.	DATA PL.	ÁREA (ha)	VAR.
999	1	06/2021	42.61	RB 86 7515
TOTAL PLANTIO			42.61	--------


ÁREAS	(ha)	(%)
PLANTIO	42.61	93.98
CARREADORES	2.34	5.16
OUTROS	0.00	0.00
SUB TOTAL AGRICULTÁVEL	44.95	99.14
AP.P.	0.00	0.00
MATA	0.00	0.00
OUTROS	0.39	0.86
SUB TOTAL NÃO AGRICULT.	0.39	0.86
ÁREA TOTAL	45.34	100.00

C. NÍVEL: 4322.57 m/l 0.99 ha 2.19 %

LEGENDA


- FAZENDA
- TALHÃO
- CURVA DE NÍVEL
- CARREADOR
- CONFRONTANTE
- REDE ELÉTRICA
- TRAJETO VAZIO
- TRAJETO CARREGADO

PLANTIO MANUAL - ESPAÇAMENTO: 1.50 X 1.50

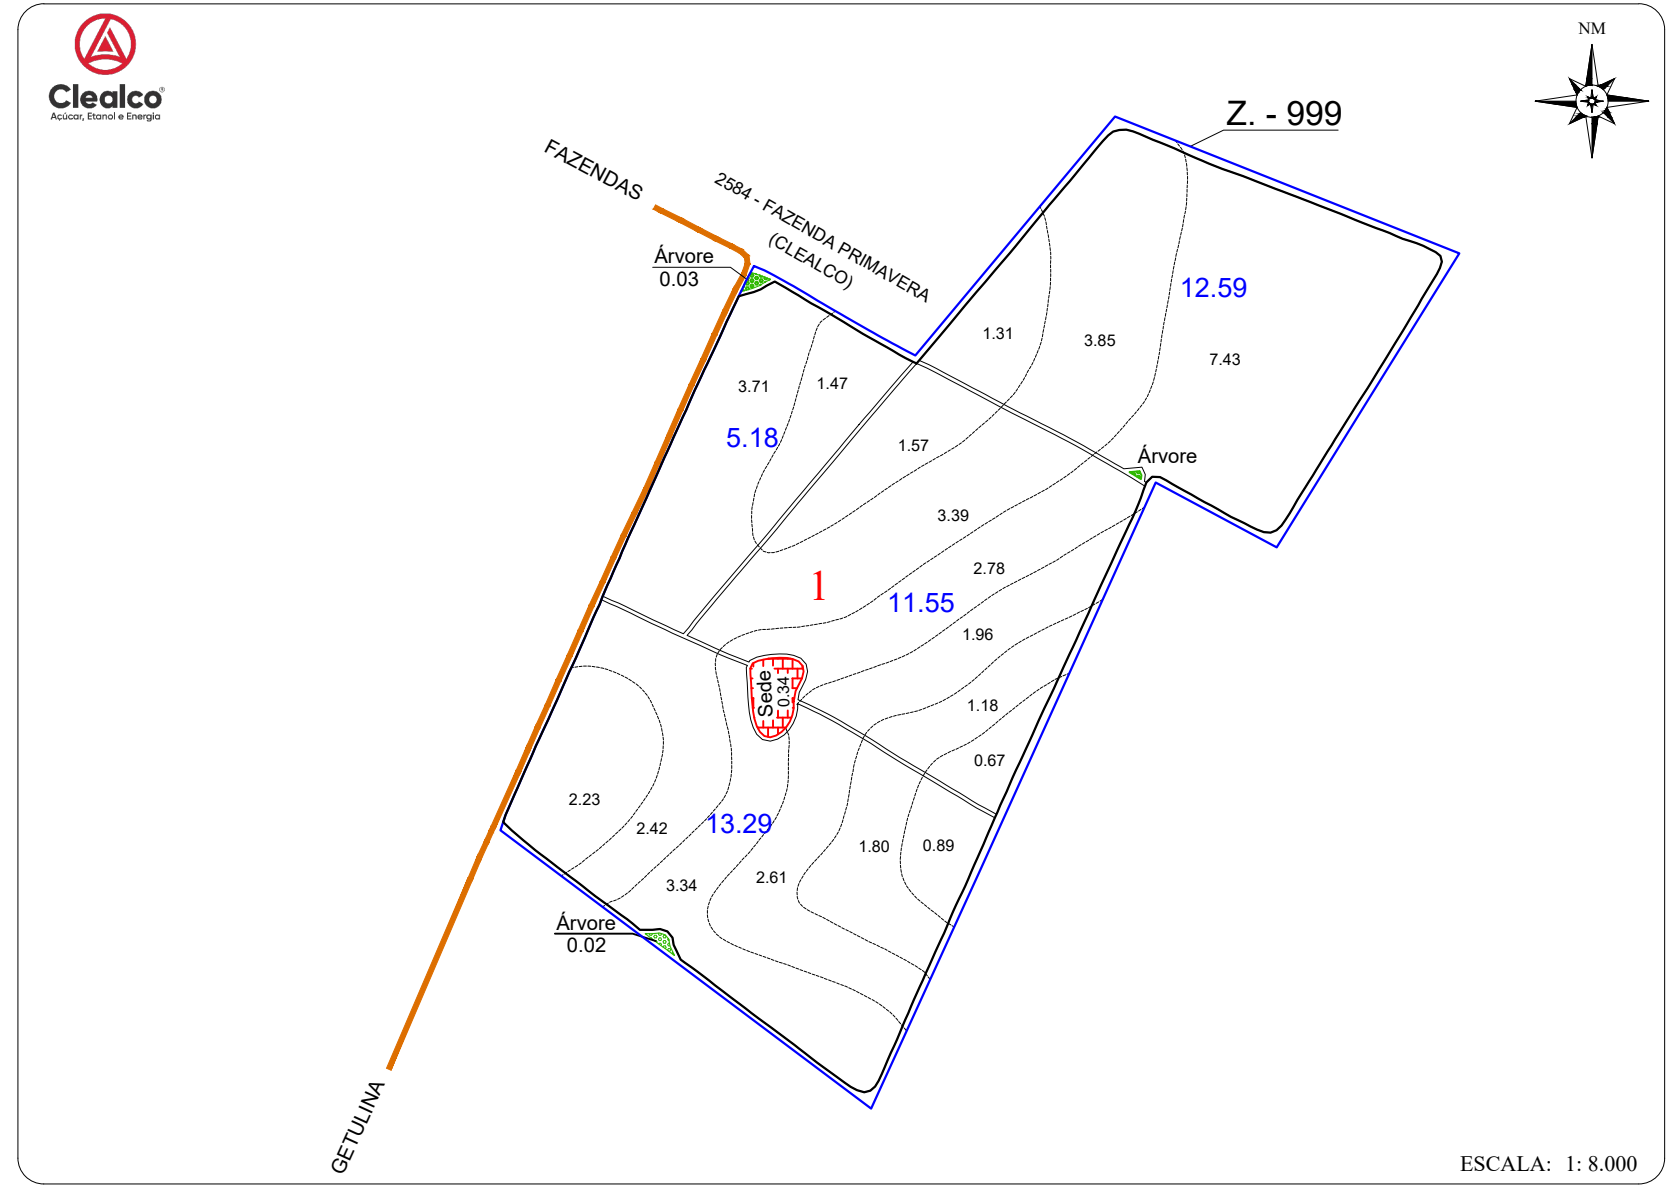

ESCALA: 1: 8.000

CROQUI DE ACESSO

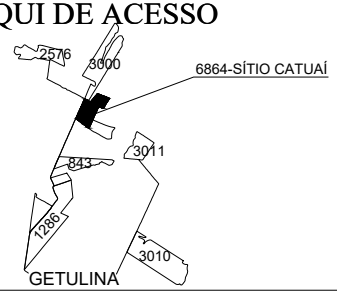

SÍTIO CATUAÍ

PROPRIETÁRIO: ALBERTO CARLOS LOLATO
ARRENDATÁRIO MÁRCIO ROS DE OLIVEIRA
MUNICÍPIO: GETULINA

DISTÂNCIAS (km):
UNID. I - Asfalto: 91.10 Terra.: 11.40
UNID.I I - Asfalto: 37.40 Terra.: 11.40
UNID. III -Asfalto: 90.40 Terra.: 11.40

COORDENADAS: E(X): 610.287,90 N(Y): 7.596.979,16
LAT: 21°43'38.1978" LONG: 49°56'0.9839"

CLEALCO - AÇÚCAR E ALCOOL S/A - DEPARTAMENTO DE TOPOGRAFIA

UNIDADE: II
PARTE: A/A
FUNDO AGRÍCOLA: 306864

M:\01-Mapa de safra\Mapas Atualizados\Terceiro\306864 - Sítio Catuai (Marcio Ros de Oliveira)\306864 - Sítio Catuai (Marcio Ros de Oliveira).dwg

Pedro Becker 19/08/21