ZONA DV	CLA	Nº Talhão	Data Plantio	Área (ha)	Variedade
999	CR	1	05/2021	26.01	RB97 5201
		2		28.13	
		3		26.99	
TOTAL PLANTIO				81.13	--------


ÁREAS	(ha)	(%)
PLANTIO	81.13	94.99
CARREADORES	4.28	5.01
OUTROS	-	-
SUB TOTAL AGRICULTÁVEL	85.41	--------
VÁRZEA	-	-
MATA	-	-
OUTROS	-	-
SUB TOTAL NÃO AGRICULT.	-	--------
ÁREA TOTAL	85.41	100.00

C. NÍVEL 1501.76 m/l 3.57 ha 4.39 %


LEGENDA

- FAZENDA
- TALHÃO
- CURVA DE NÍVEL
- CARREADOR
- CONFRONTANTE
- REDE ELÉTRICA
- TRAJETO VAZIO
- TRAJETO CARREGADO

PLANTIO MANUAL - ESPAÇAMENTO: 1.50 x 1.50

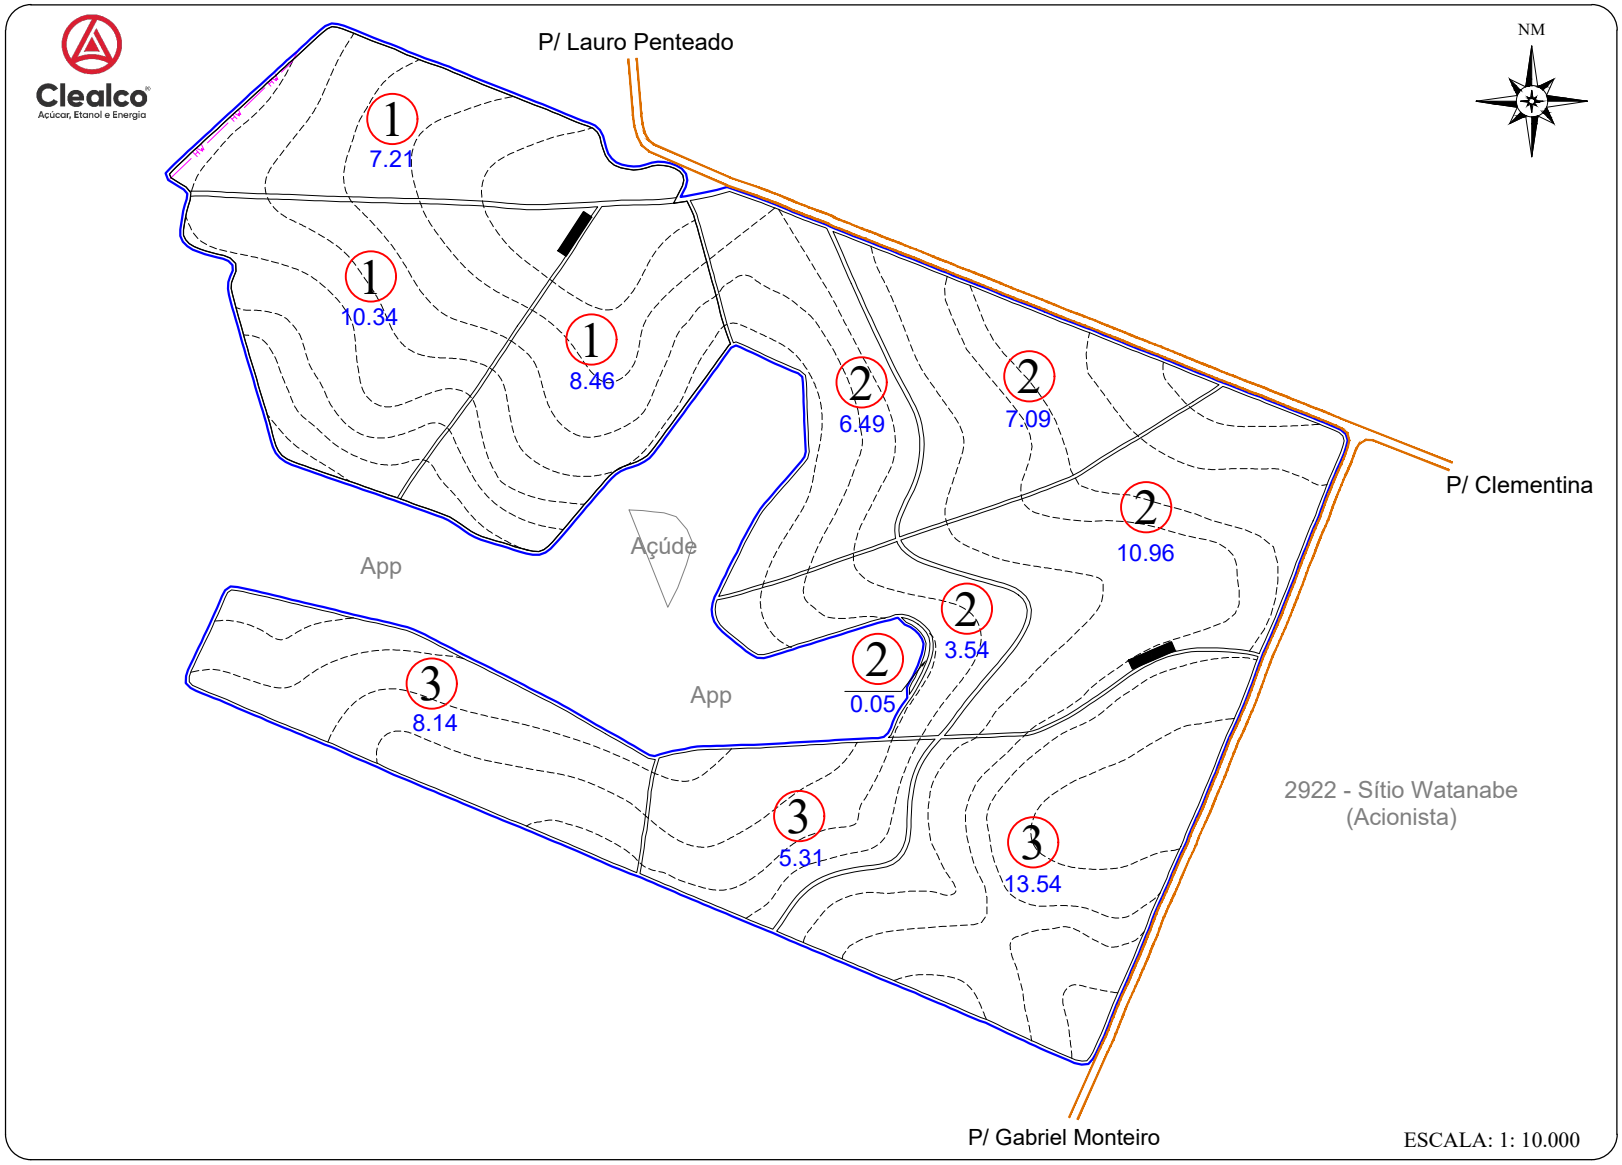

CROQUI DE ACESSO

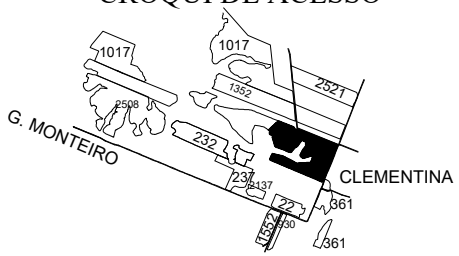

FAZENDA SANTO ANTÔNIO

PROPRIETÁRIO: PAULO BENTO BOGO
COMPRADOR: CLEALCO S/A
MUNICÍPIO: CLEMENTINA

DISTÂNCIAS (km):
UNID. I - Asfalto: 3.50 Terra.: 4.50
UNID.I I - Asfalto: 60.50 Terra.: 4.50
UNID. III -Asfalto: 45.30 Terra.: 4.50

COORDENADAS: E(X): 553405 N(Y): 7617355
LAT: 21° 32' 44,94364" LONG: 50° 29' 03,28363"

CLEALCO - AÇÚCAR E ALCOOL S/A - DEPARTAMENTO DE TOPOGRAFIA

UNIDADE: I
PARTE: A/A
FUNDO AGRÍCOLA: 306874

M:\01-Mapa de safra\Mapas Atualizados\Terceiro\306874 - Fazenda Santo Antonio (Paulo Bento Bogo)\306874 - Fazenda Santo Antonio (Paulo Bento Bogo).dwg

Fernanda Bezerra 15/06/21