ZONA	Nº TAL.	DATA PL.	ÁREA (ha)	VAR.
999	1	05/2021	22.52	RB 97 5242
	2		31.68	
	3		30.71	
	4		2.79	
	5		21.92	
TOTAL PLANTIO			109.62	--------

ÁREAS	(ha)	(%)
PLANTIO	109.62	92.96
CARREADORES	6.16	5.23
OUTROS	0.00	0.00
SUB TOTAL AGRICULTÁVEL	115.78	98.19
AP.P.	0.66	0.56
MATA	0.00	0.00
OUTROS	1.48	1.26
SUB TOTAL NÃO AGRICULT.	2.14	1.81
ÁREA TOTAL	117.92	100.00

C. NÍVEL: 13489.76 m/l 3.10 ha 2.63 %


LEGENDA

- FAZENDA
- TALHÃO
- CURVA DE NÍVEL
- CARREADOR
- CONFRONTANTE
- REDE ELÉTRICA
- TRAJETO VAZIO
- TRAJETO CARREGADO

PLANTIO MANUAL - ESPAÇAMENTO: 1.50 X 1.50


Clealco
Açúcar, Etanol e Energia

NM

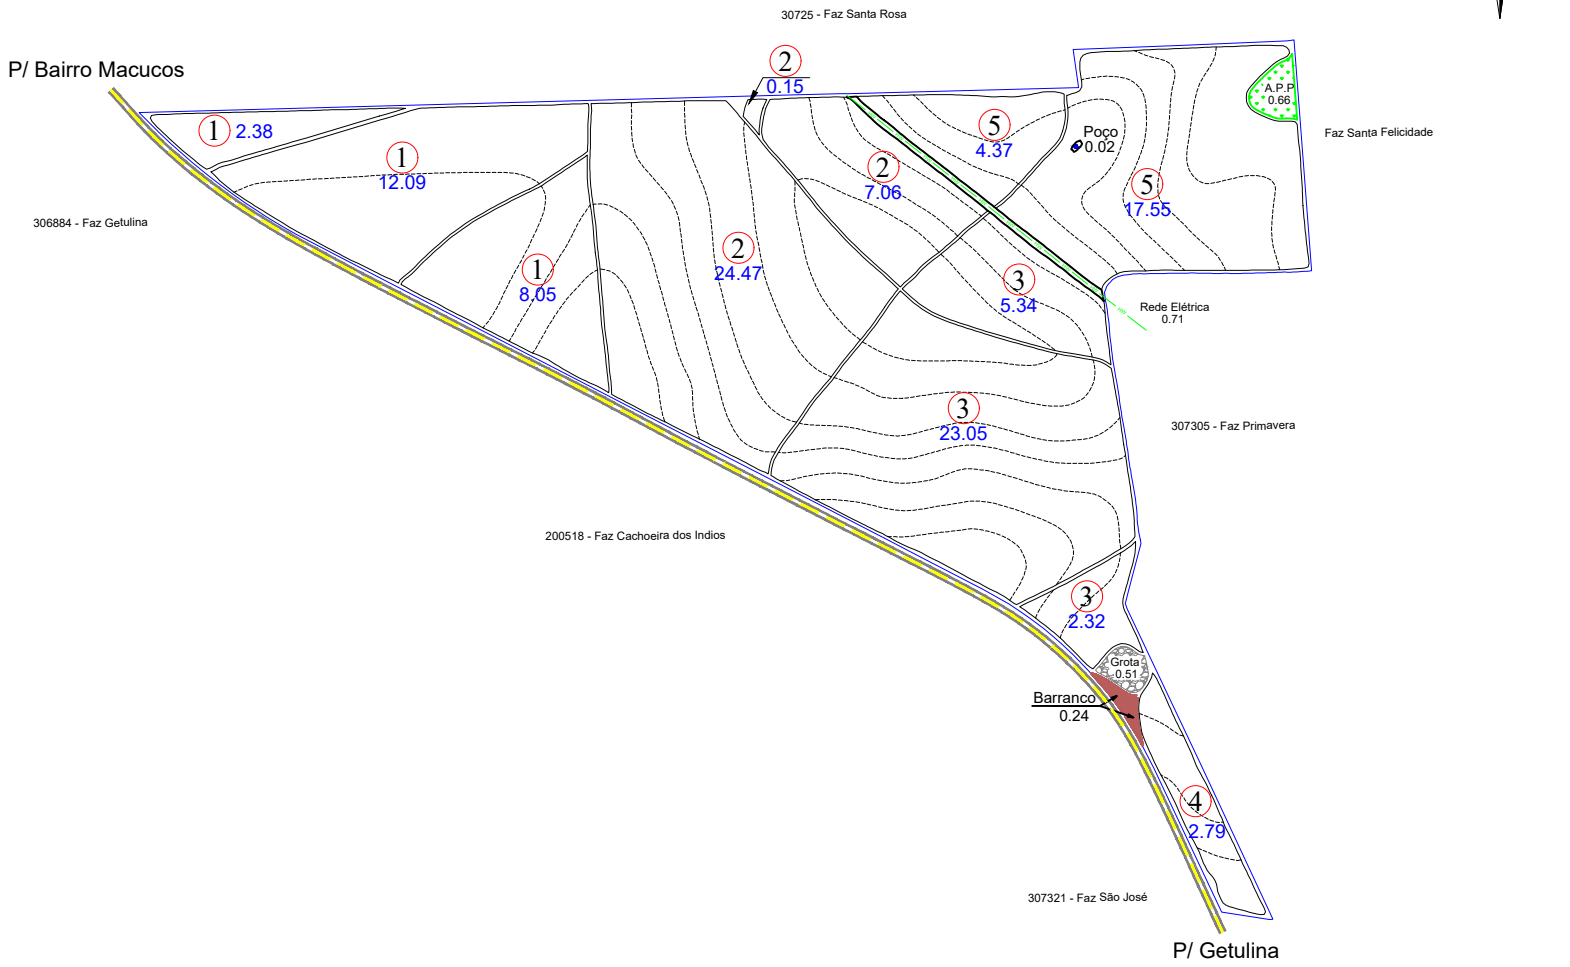

ESCALA: 1: 14.000

CROQUI DE ACESSO

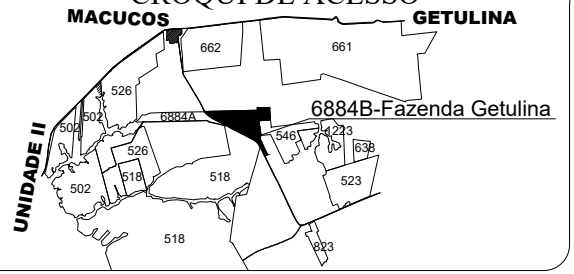

FAZENDA GETULINA

PROPRIETÁRIO: JÚLIO CÉSAR RIOS DE BARROS
COMPRADOR: CLEALCO S/A
MUNICÍPIO: GETULINA

DISTÂNCIAS (km):
UNID. I - Asfalto: 71.90 Terra.: 3.70
UNID.I I - Asfalto: 18.10 Terra.: 3.70
UNID. III -Asfalto: 68.10 Terra.: 3.70

COORDENADAS: E(X): 594.606,14 N(Y): 7.592.264,48
LAT: 21°46'14.7896" LONG: 50°5'5.8221"

CLEALCO - AÇÚCAR E ALCOOL S/A - DEPARTAMENTO DE TOPOGRAFIA

UNIDADE:
II
PARTE:
A/B
FUNDO AGRÍCOLA:
306884

M:\01-Mapa de safra\Mapas Atualizados\Terceiro\306884 - Fazenda Getulina (Julio Cesar Rios de Barros)\306884 A - Fazenda Getulina (Julio Cesar Rios de Barros).dwg

Pedro Becker 26/07/21