| ZONA DV | Nº TAL. | DATA PL. | ÁREA (ha) | VAR. |
|---|---|---|---|---|
| 999 | 1 | 04/2021 | 13.25 | CTC 4 |
| | 2 | | 19.70 | |
| | 3 | | 17.60 | |
| | 4 | | 47.60 | |
| | 5 | | 21.30 | |
| TOTAL PLANTIO | | | 119.45 | |

| ÁREAS | (ha) | (%) |
|---|---|---|
| PLANTIO | 119.45 | 92.35 |
| CARREADORES | 7.29 | 5.64 |
| - | - | - |
| SUB TOTAL AGRICULTÁVEL | 126.74 | -------- |
| APP | 1.70 | 1.31 |
| SEDE | 0.90 | 0.70 |
| - | - | - |
| SUB TOTAL NÃO AGRICULT. | 2.60 | -------- |
| ÁREA TOTAL | 129.34 | 100.00 |

C. NÍVEL 18846.66 m/l 4.33 ha 3.72 %


LEGENDA

- FAZENDA
- TALHÃO
- CURVA DE NÍVEL
- CARREADOR
- CONFRONTANTE
- REDE ELÉTRICA
- TRAJETO VAZIO
- TRAJETO CARREGADO


PLANTIO MANUAL - ESPAÇAMENTO: 1.50 x 1.50

Clealco
Açúcar, Etanol e Energia

NM

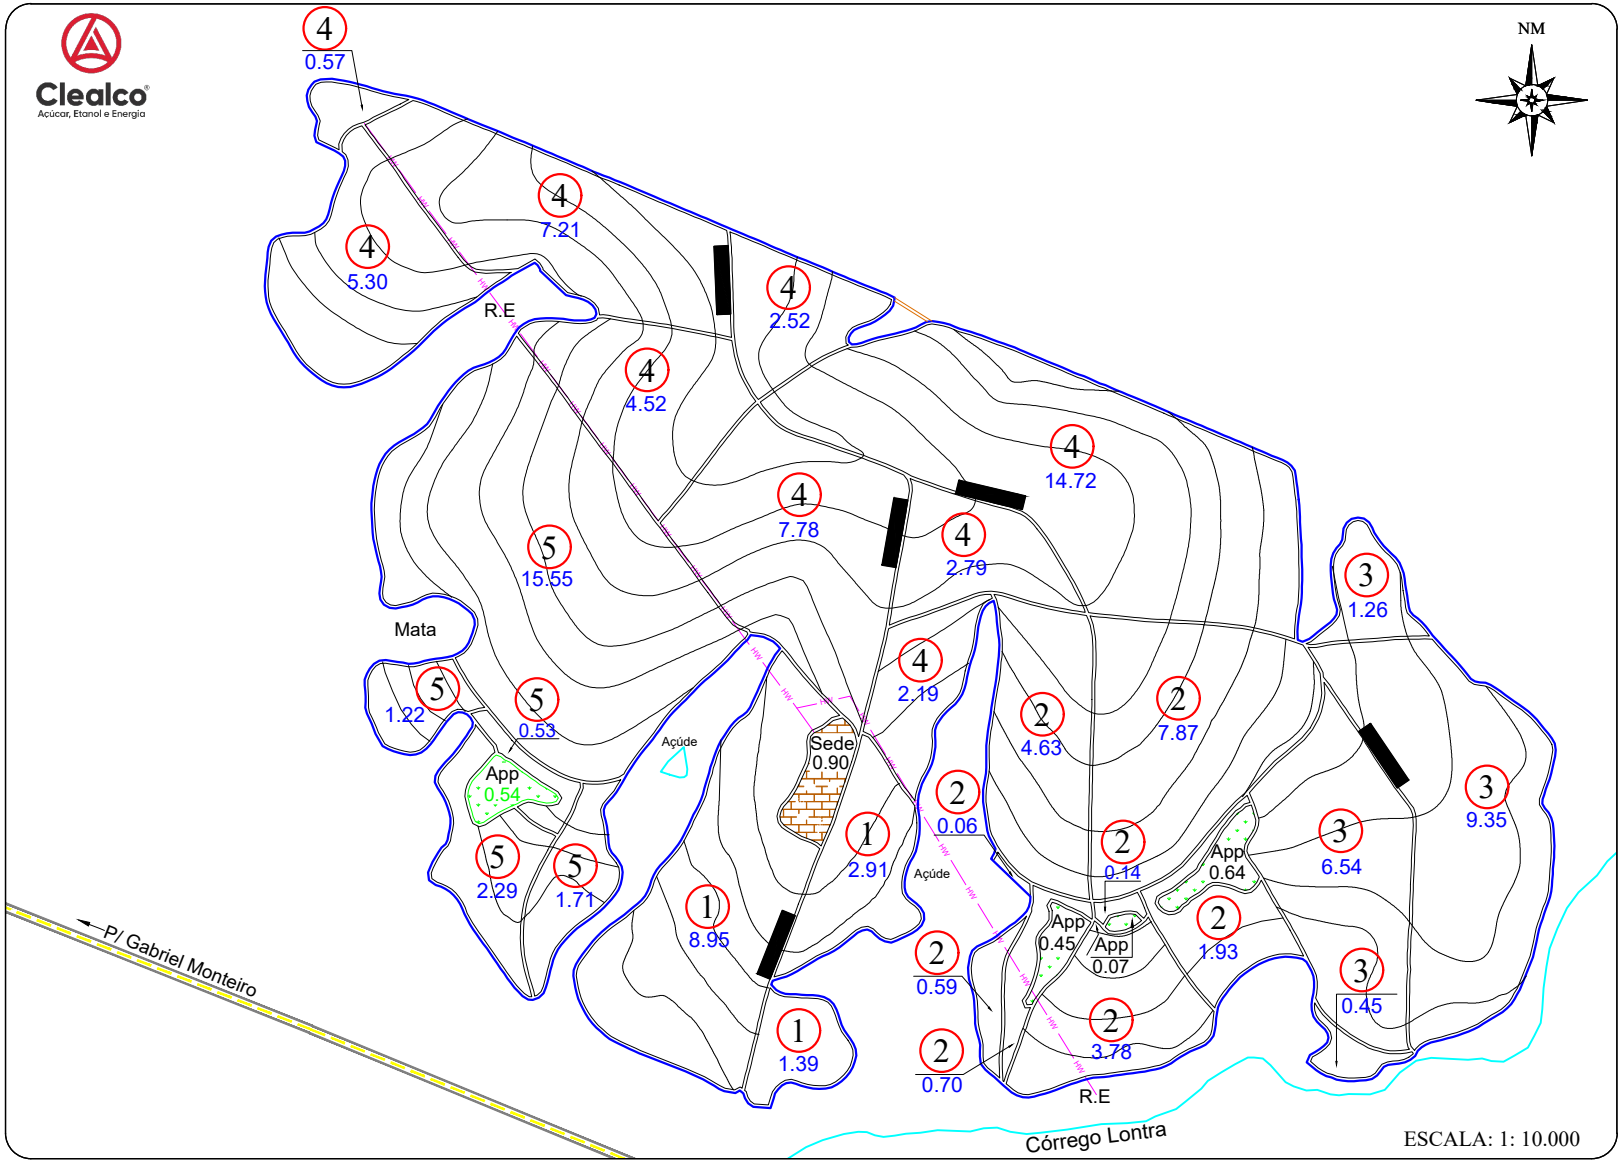


CROQUI DE ACESSO

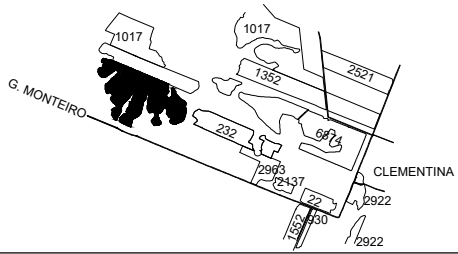


# FAZENDA CISNE BRANCO

FORNECEDOR: WALDEMIR APARICIO CAPUTO
COMPRADOR: CLEALCO S/A
MUNICÍPIO: GABRIEL MONTEIRO

DISTÂNCIAS (km):

| | | | |
|---|---|---|---|
| UNID. I - Asfalto: | 3.10 | Terra.: | 10.50 |
| UNID.I I - Asfalto: | 59.30 | Terra.: | 10.50 |
| UNID. III -Asfalto: | 47.00 | Terra.: | 10.50 |

COORDENADAS: E(X): 550481.28 N(Y): 7618057.17
LAT: 21º 32' 22" LONG: 50º 30' 45"

CLEALCO - AÇÚCAR E ALCOOL S/A - DEPARTAMENTO DE TOPOGRAFIA

UNIDADE: I

PARTE: A/A

FUNDO AGRÍCOLA: 306889

M:\01-Mapa de safra\Mapas Atualizados\Terceiro\306889 - Fazenda Cisne Branco (Waldemir Aparicio Caputo)\306889 - Fazenda Cisne Branco (Waldemir Aparicio Caputo).dwg

Fernanda Bezerra 13/07/21