ZONA D.V.	Nº TAL.	DATA PL.	ÁREA (ha)	VARIEDADE
999	1	03/2020	7.41	CTC 04
TOTAL PLANTIO			7.41	--------

ÁREAS	(ha)	(%)
PLANTIO	7.41	93.63
CARREADORES	0.50	6.37
OUTROS	0.00	0.00
SUB TOTAL AGRICULTÁVEL	7.91	100.00
AP.P.	0.00	0.00
ÁRVORES	0.00	0.00
OUTROS	0.00	0.00
SUB TOTAL NÃO AGRICULT.	0.00	0.00
ÁREA TOTAL	7.91	100.00

C. NÍVEL: 0.00 m/l 0.00 ha 0.00 %

LEGENDA

🟦	FAZENDA	▬	CONFRONTANTE
▬	TALHÃO	─·─	REDE ELÉTRICA
▪▪▪	CURVA DE NÍVEL	⇨	TRAJETO VAZIO
─	CARREADOR	→	TRAJETO CARREGADO

PLANTIO MANUAL - ESPAÇAMENTO: 1.50 X 1.50

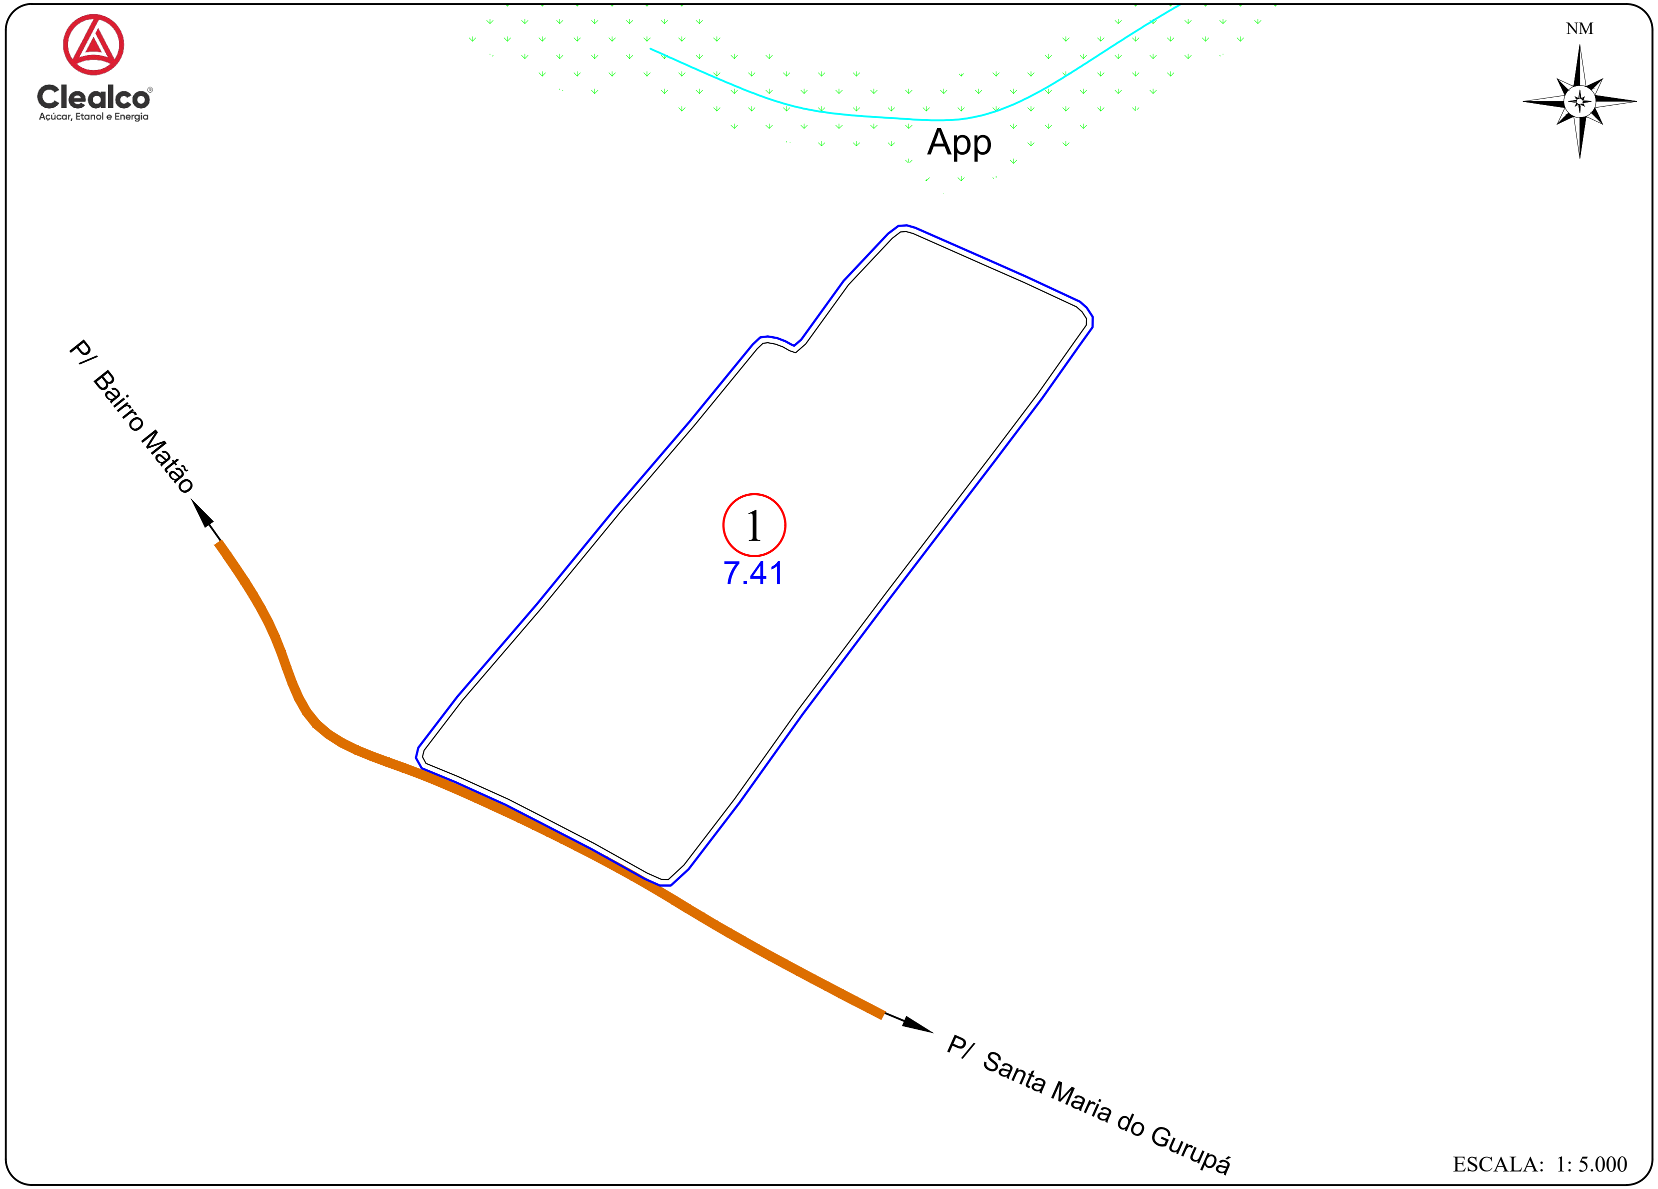
Clealco
Açúcar, Etanol e Energia
App
NM
P/ Bairro Matão
1
7.41
P/ Santa Maria do Gurupá

ESCALA: 1: 5.000

CROQUI DE ACESSO

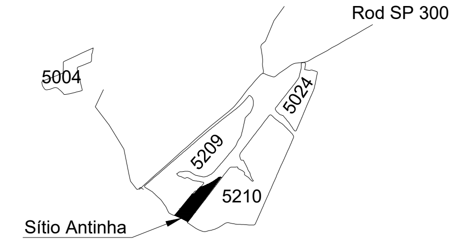
Rod SP 300
5004
5024
5209
5210
Sítio Antinha

SÍTIO ANTINHA

PROPRIETÁRIO:	RAFAEL PONTIN E OUTRO	DISTÂNCIAS (km):			
COMPRADOR:	CLEALCO S/A	UNID. I - Asfalto:	51.60	Terra.:	11.50
MUNICÍPIO:	PROMISSÃO	UNID.I I - Asfalto:	46.50	Terra.:	1.50
		UNID. III -Asfalto:	13.50	Terra.:	13.50

COORDENADAS: E(X): 598409.66 N(Y): 7609833.26
LAT: -21°36'42.6853" LONG: -50°2'57.1498"

CLEALCO - AÇÚCAR E ALCOOL S/A - DEPARTAMENTO DE TOPOGRAFIA

UNIDADE:
II

PARTE:
A/A

FUNDO AGRÍCOLA:
306890

M:\03-Projetos (Sistematização, Pré, Pós e outros)\Terceiro_2024\306890 - Sitio Antinha (Rafael Pontin e Outro).dwg

Fernanda Bezerra 04/04/24