
Clealco
Açúcar, Etanol e Energia

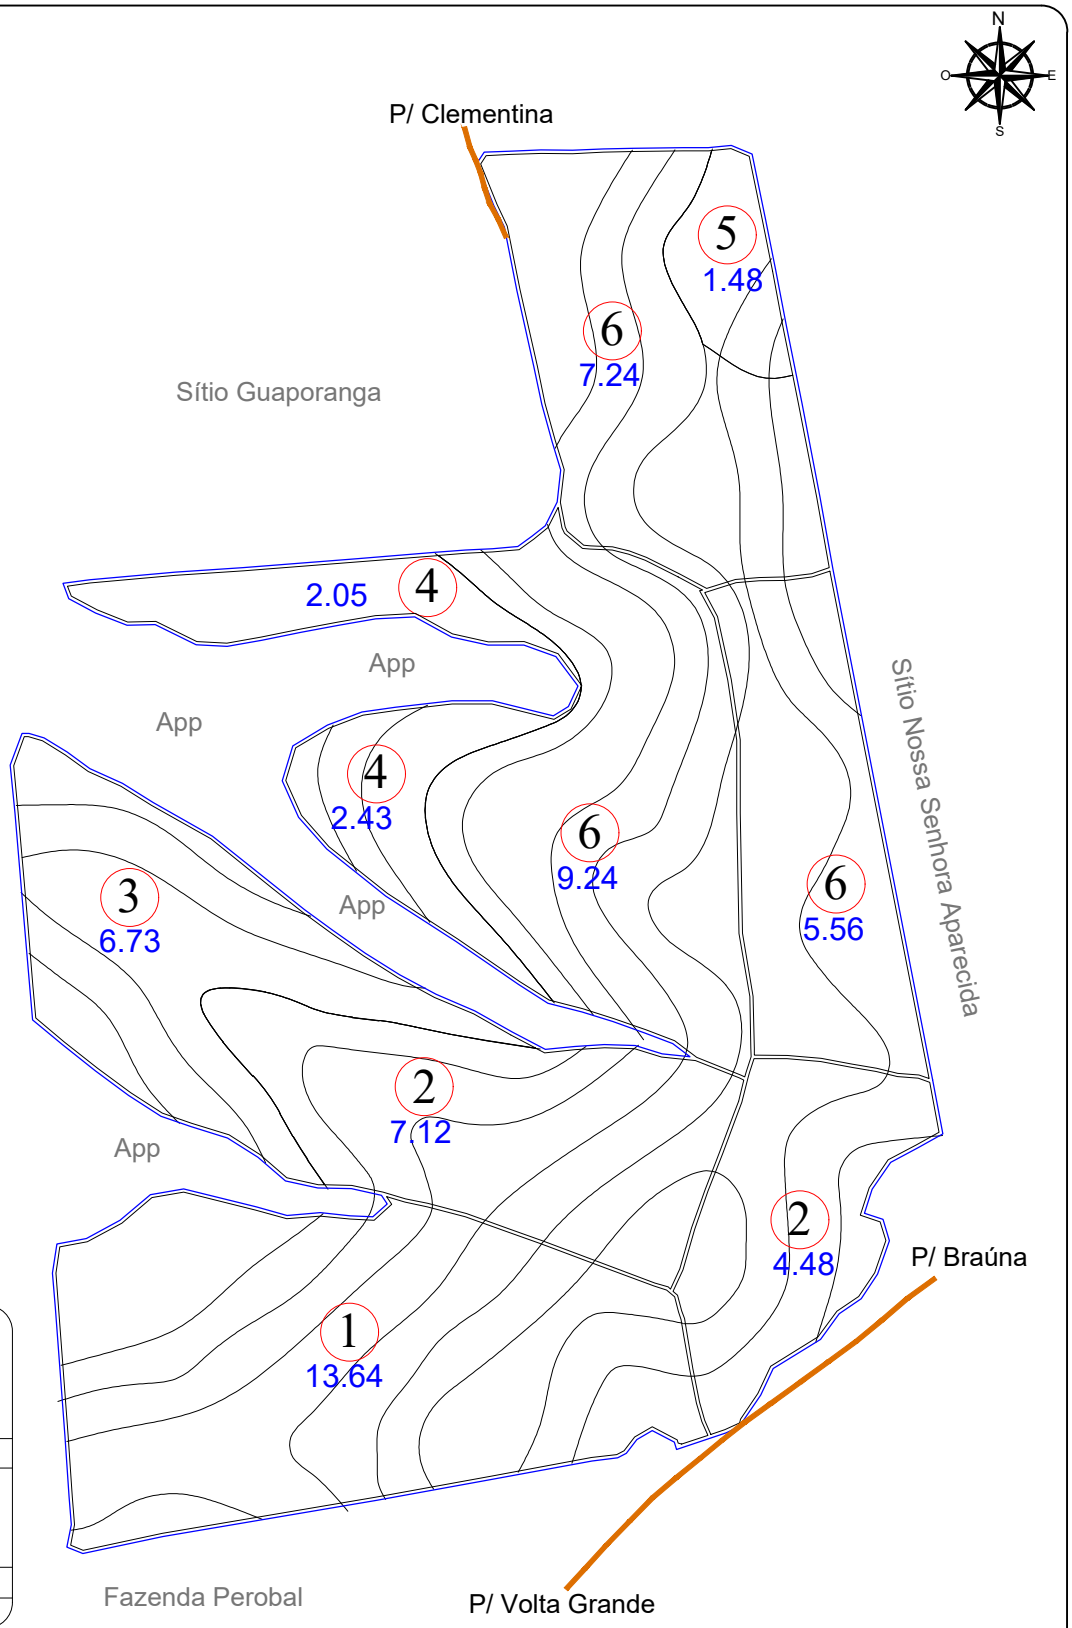

Nº TAL.	DATA PL.	ÁREA (ha)	VARIEDADE
1	04/2026	13.64	RB07 5322
2		11.60	
3		6.73	
4		4.48	
5		1.48	
6		22.04	
TOTAL PLANTIO		59.97	

ÁREAS	(ha)	(%)
PLANTIO	59.97	96.28
CARREADORES	2.32	3.72
OUTROS	0.00	0.00
SUB TOTAL AGRICULTÁVEL	62.29	100.00
AP.P.	0.00	0.00
ÁRVORES	0.00	0.00
OUTROS	0.00	0.00
SUB TOTAL NÃO AGRICULT.	0.00	0.00
ÁREA TOTAL	62.29	100.00

C. NÍVEL: 12068.19 m/l 2.78 ha 4.46 %


LEGENDA

- FAZENDA
- TALHÃO
- REDE ELÉTRICA
- TERRAÇO BASE LARGA
- TERRAÇO EMBUTIDO
- (P.O.A) PATIO DE OPERAÇÃO

ESPAÇAMENTO: 1.50 x 1.50
TIRO MÉDIO ESTIMADO: 000.00 m
D.V: 5.47 %

ESCALA: 1: 9.000

CROQUI DE ACESSO

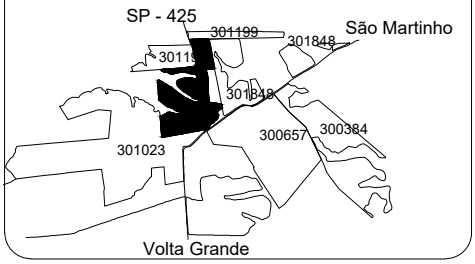

SÍTIO NOSSA SENHORA APARECIDA

PROPRIETÁRIO: RODOLFO PEREIRA BARRETO
COMPRADOR: CLEALCO
MUNICÍPIO: BRAÚNA - SP

DISTÂNCIAS (km):
UNID. I - Asfalto: 20.60 Terra.: 8.90
UNID.I I - Asfalto: 25.00 Terra.: 9.00

COORDENADAS: E(X): 569990.18 N(Y): 7613276.59
LAT: -21°34'55.5292" LONG: -50°19'26.0833"

CLEALCO - AÇÚCAR E ALCOOL S/A - DEPARTAMENTO DE GEOTECNOLOGIA

LEVANTAMENTO VIA:
SATÉLITE
GPS / VANT
GOOGLE

UNIDADE: I
PARTE: A/A
FUNDO AGRÍCOLA: 306900

M:\01-Mapa de safra\Mapas Atualizados\Terceiro\306900 - Sítio Nossa Senhora Aparecida (Rodolfo Pereira Barreto)\306900 - Sítio Nossa Senhora Aparecida (Rodolfo Pereira Barreto).dwg

Benati 23/02/2026