
Clealco
Açúcar, Etanol e Energia

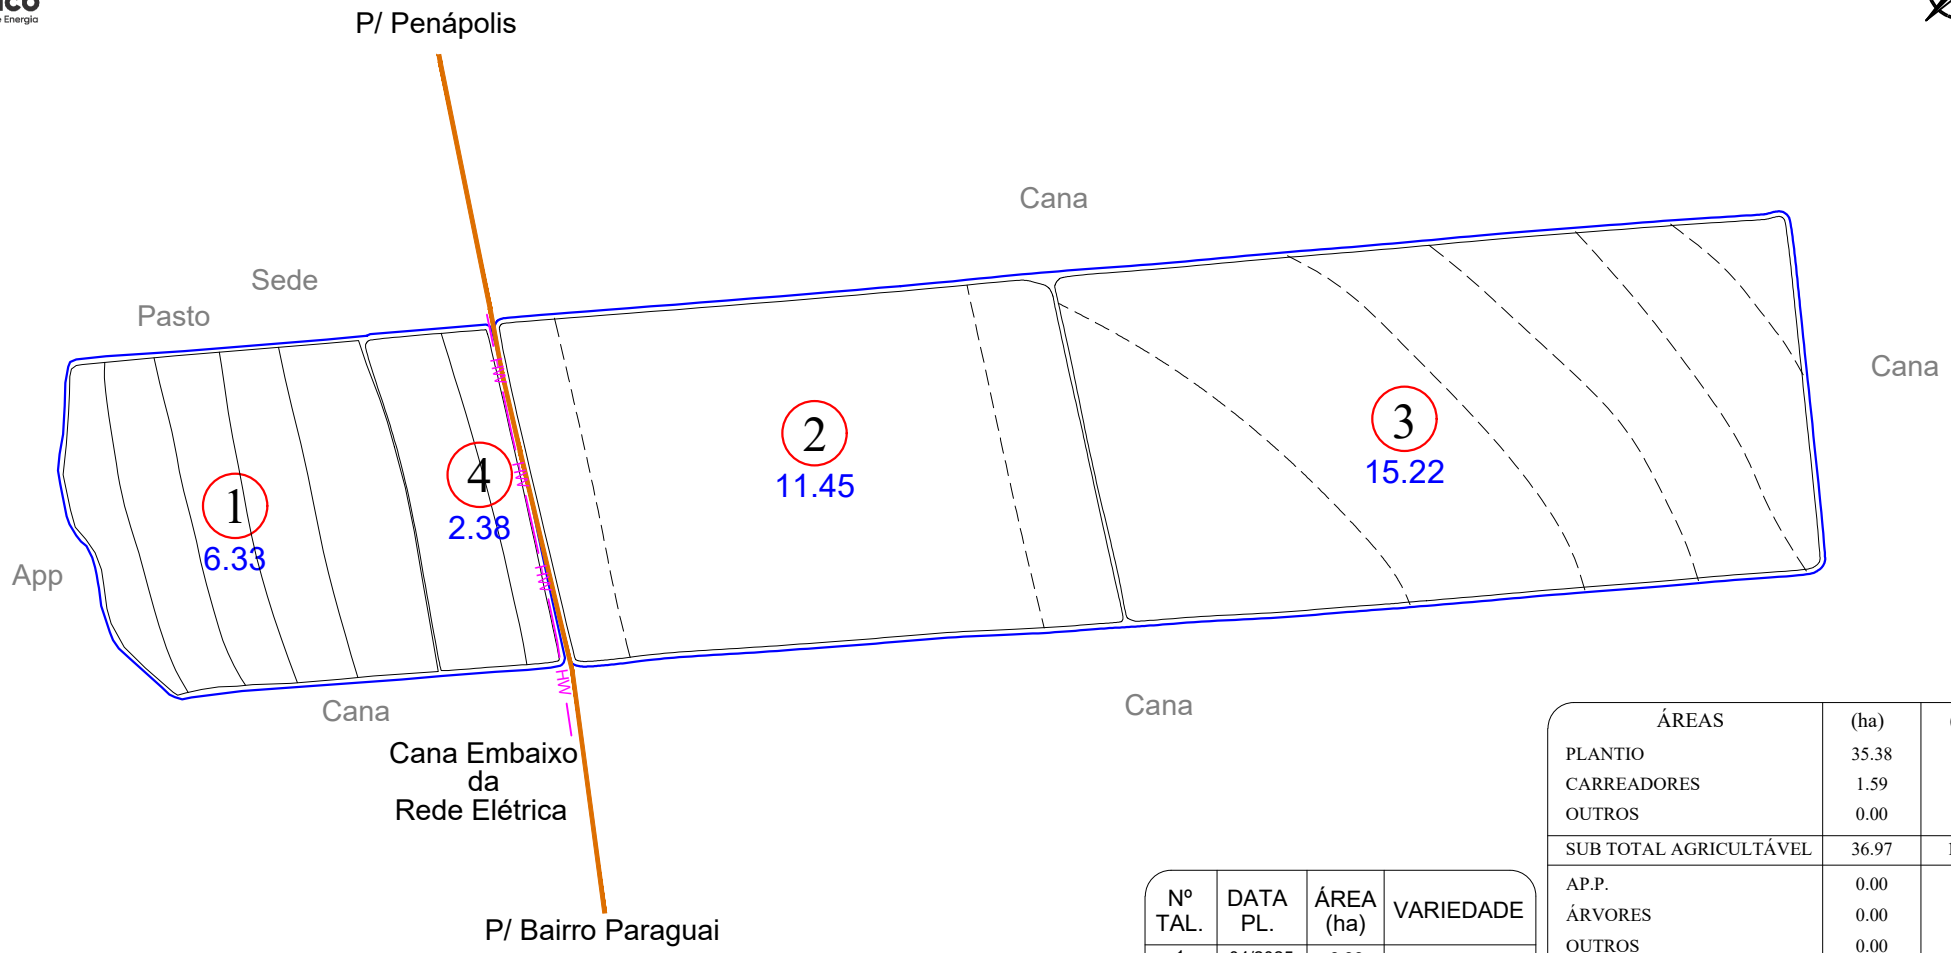

ESCALA: 1: 6.000

Nº TAL.	DATA PL.	ÁREA (ha)	VARIEDADE
1	04/2025	6.33	RB07 5322
2	03/2026	11.45	
3		15.22	
4		2.38	
TOTAL		35.38	


ÁREAS	(ha)	(%)
PLANTIO	35.38	95.71
CARREADORES	1.59	4.29
OUTROS	0.00	0.00
SUB TOTAL AGRICULTÁVEL	36.97	100.00
AP.P.	0.00	0.00
ÁRVORES	0.00	0.00
OUTROS	0.00	0.00
SUB TOTAL NÃO AGRICULT.	0.00	0.00
ÁREA TOTAL	36.97	100.00

C. NÍVEL: 1325.87 m/l 0.30 ha 0.82 %

LEGENDA
- FAZENDA
- TALHÃO
- REDE ELÉTRICA
- TERRAÇO BASE LARGA
- TERRAÇO EMBUTIDO

ESPAÇAMENTO: 1.50 x 1.50
TIRO MÉDIO ESTIMADO: 254.98 m
D.V: 3.53 %

CROQUI DE ACESSO

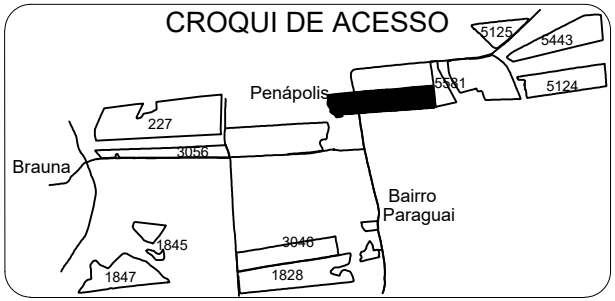

SÍTIO SÃO JOÃO

PROPRIETÁRIO: WESLEI A. DE SOUZA ANDRADE
COMPRADOR: CLEALCO
MUNICÍPIO: PENÁPOLIS - SP

DISTÂNCIAS (km):
UNID. I - Asfalto: 48.00 Terra.: 5.00
UNID.I I - Asfalto: 56.00 Terra.: 5.00

COORDENADAS: E(X): 587952.33 N(Y): 7621718.60
LAT: -21°30'18.1117" LONG: -50°9'3.0919"
CLEALCO - AÇÚCAR E ALCOOL S/A - DEPARTAMENTO DE GEOTECNOLOGIA

LEVANTAMENTO VIA:
- SATÉLITE
- GPS / VANT
- GOOGLE

UNIDADE: I
PARTE: A/A
FUNDO AGRÍCOLA: 306901

M:\01-Mapa de safra\Mapas Atualizados\Terceiro\306901 - Sítio São João (Weslei Antonio de Souza Andrade)\306901 - Sítio São João (Weslei Antonio de Souza Andrade).dwg

Bruno Gamboa 13/08/26