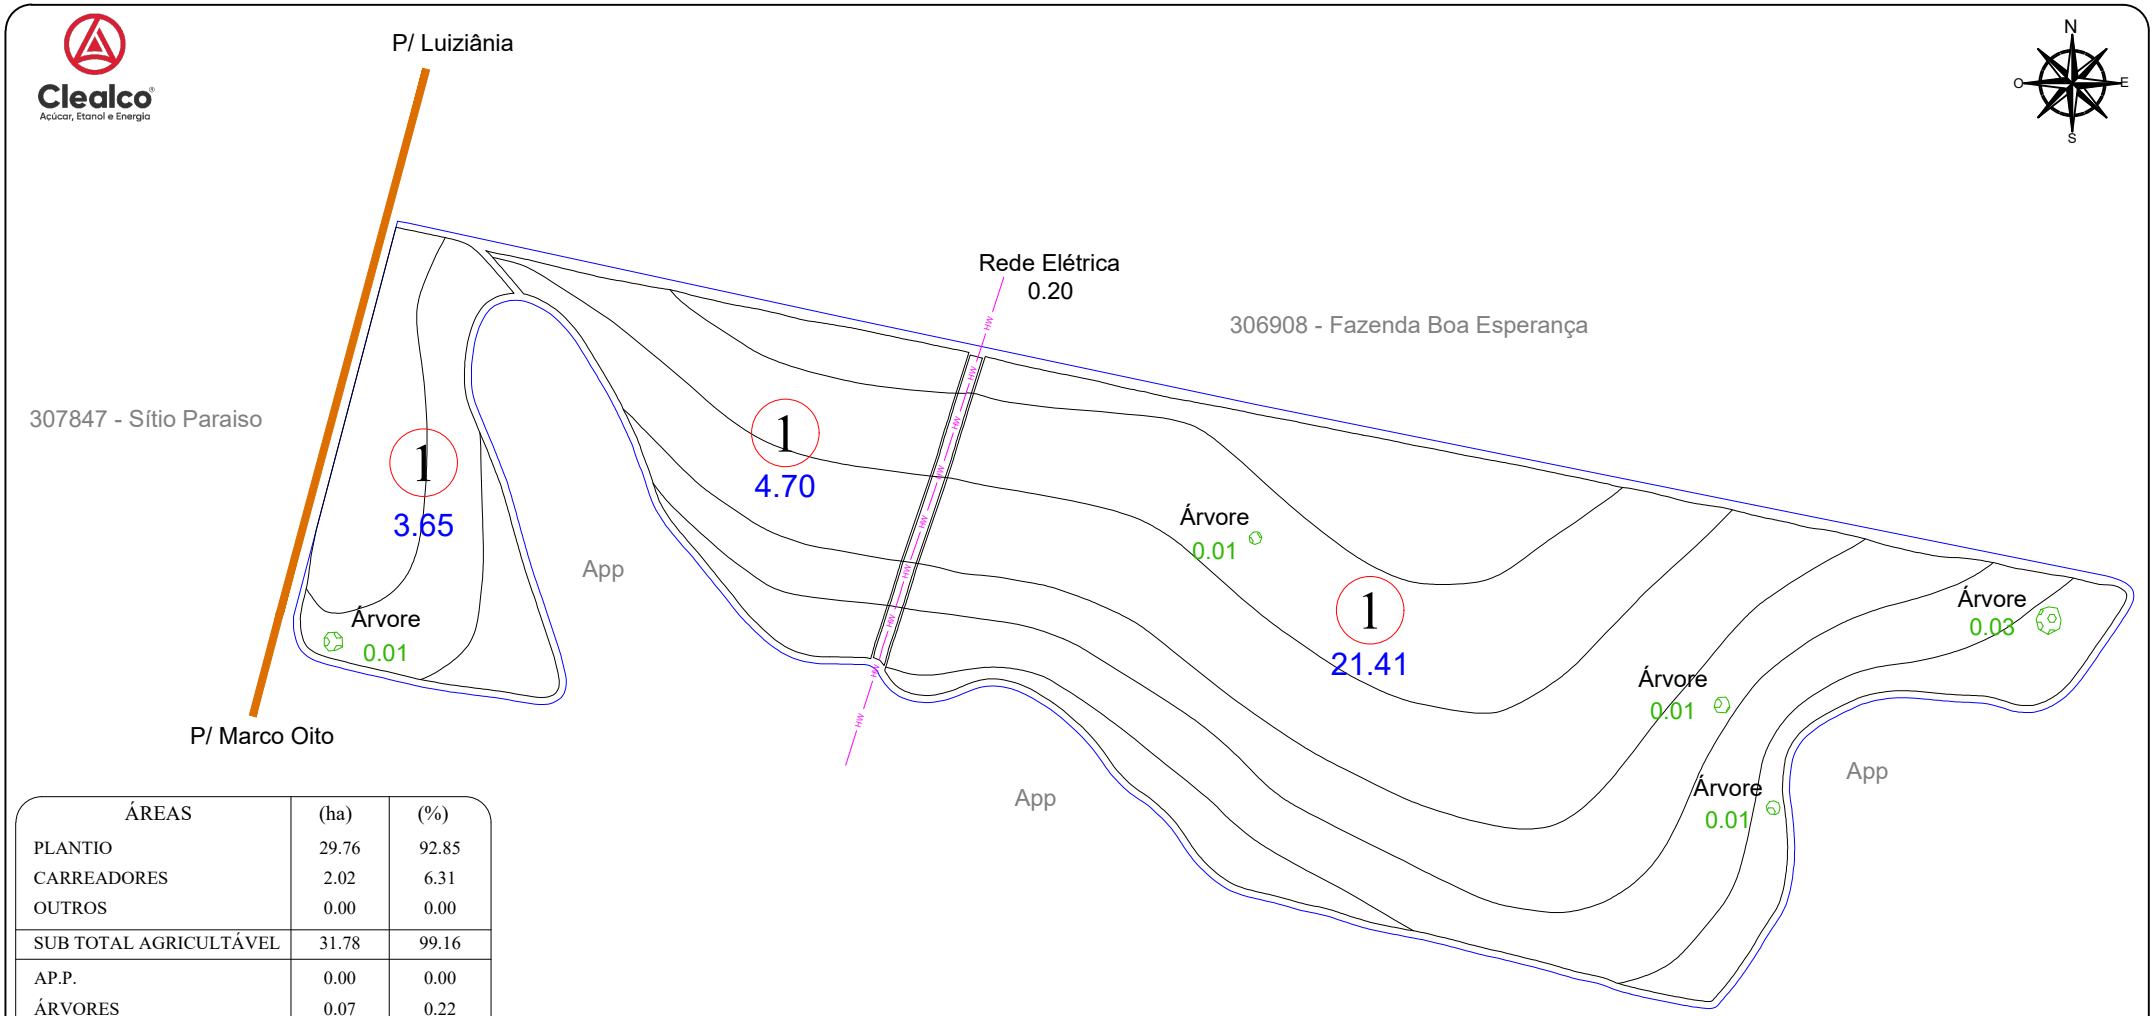


ÁREAS	(ha)	(%)
PLANTIO	29.76	92.85
CARREADORES	2.02	6.31
OUTROS	0.00	0.00
SUB TOTAL AGRICULTÁVEL	31.78	99.16
AP.P.	0.00	0.00
ÁRVORES	0.07	0.22
OUTROS	0.20	0.62
SUB TOTAL NÃO AGRICULT.	0.27	0.84
ÁREA TOTAL	32.05	100.00

C. NÍVEL: 5420.65 m/l 1.25 ha 3.89 %


Nº TAL.	DATA PL.	ÁREA (ha)	VARIEDADE
1	06/2020	29.76	RB 975162
TOTAL PLANTIO		29.76	

ESCALA: 1: 5.500

LEGENDA
- FAZENDA
- TALHÃO
- REDE ELÉTRICA
- TERRAÇO BASE LARGA
- TERRAÇO EMBUTIDO
- VAZIO
- CARREGADO

ESPAÇAMENTO: 1.50 x 1.50
TIRO MÉDIO ESTIMADO: 000.00 m
D.V: 5.37%

CROQUI DE ACESSO

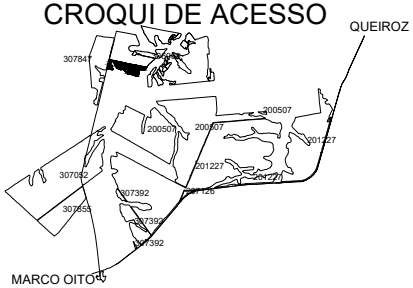

SÍTIO ELDORADO

PROPRIETÁRIO: FELIPE DE FIGUEIREDO FERRAZ
COMPRADOR: CLEALCO
MUNICÍPIO: QUEIROZ - SP

DISTÂNCIAS (km):
UNID. I - Asfalto: 32.00 Terra.: 16.00
UNID.I I - Asfalto: 16.50 Terra.: 7.20

COORDENADAS: E(X): 570536.87 N(Y): 7587869.59
LAT: -21°48'41.7719" LONG: -50°19'3.1825"
CLEALCO - AÇÚCAR E ALCOOL S/A - DEPARTAMENTO DE GEOTECNOLOGIA

LEVANTAMENTO VIA:
- SATÉLITE
- GPS / VANT
- GOOGLE

UNIDADE: II
PARTE: A/A
FUNDO AGRÍCOLA: 306909

M:\01-Mapa de safra\Mapas Atualizados\Terceiro\306909 - Sitio Eldorado (Felipe de Figueiredo Ferraz)\306909 - Sitio Eldorado (Felipe de Figueiredo Ferraz).dwg

Bruno Gamboa 09/06/26