| ZONA D.V. | Nº TAL. | DATA PL. | ÁREA (ha) | VARIEDADE |
|---|---|---|---|---|
| 999<br>4.42 % | 1 | 04/2023 | 3.73 | RB 966928 |
| | | | | |
| | | | | |
| TOTAL PLANTIO | | | 3.73 | -------- |

| ÁREAS | (ha) | (%) |
|---|---|---|
| PLANTIO | 3.73 | 91.26 |
| CARREADORES | 0.36 | 8.74 |
| OUTROS | 0.00 | 0.00 |
| SUB TOTAL AGRICULTÁVEL | 4.09 | 100.00 |
| AP.P. | 0.00 | 0.00 |
| ÁRVORES | 0.00 | 0.00 |
| OUTROS | 0.00 | 0.00 |
| SUB TOTAL NÃO AGRICULT. | 0.00 | 0.00 |
| ÁREA TOTAL | 4.09 | 100.00 |

| | | | |
|---|---|---|---|
| C. NÍVEL: | 345.67 m/l | 0.08 ha | 1.95 % |

## LEGENDA

| | |
|---|---|
| ▬ FAZENDA | ▬ CONFRONTANTE |
| ▬ TALHÃO | - - REDE ELÉTRICA |
| ▪▪▪▪ CURVA DE NÍVEL | ⇨ TRAJETO VAZIO |
| — CARREADOR | ➞ TRAJETO CARREGADO |

PLANTIO MANUAL - ESPAÇAMENTO: 1.50 X 1.50
TIRO MÉDIO ESTIMADO: 74.59 m

Clealco
Açúcar, Etanol e Energia

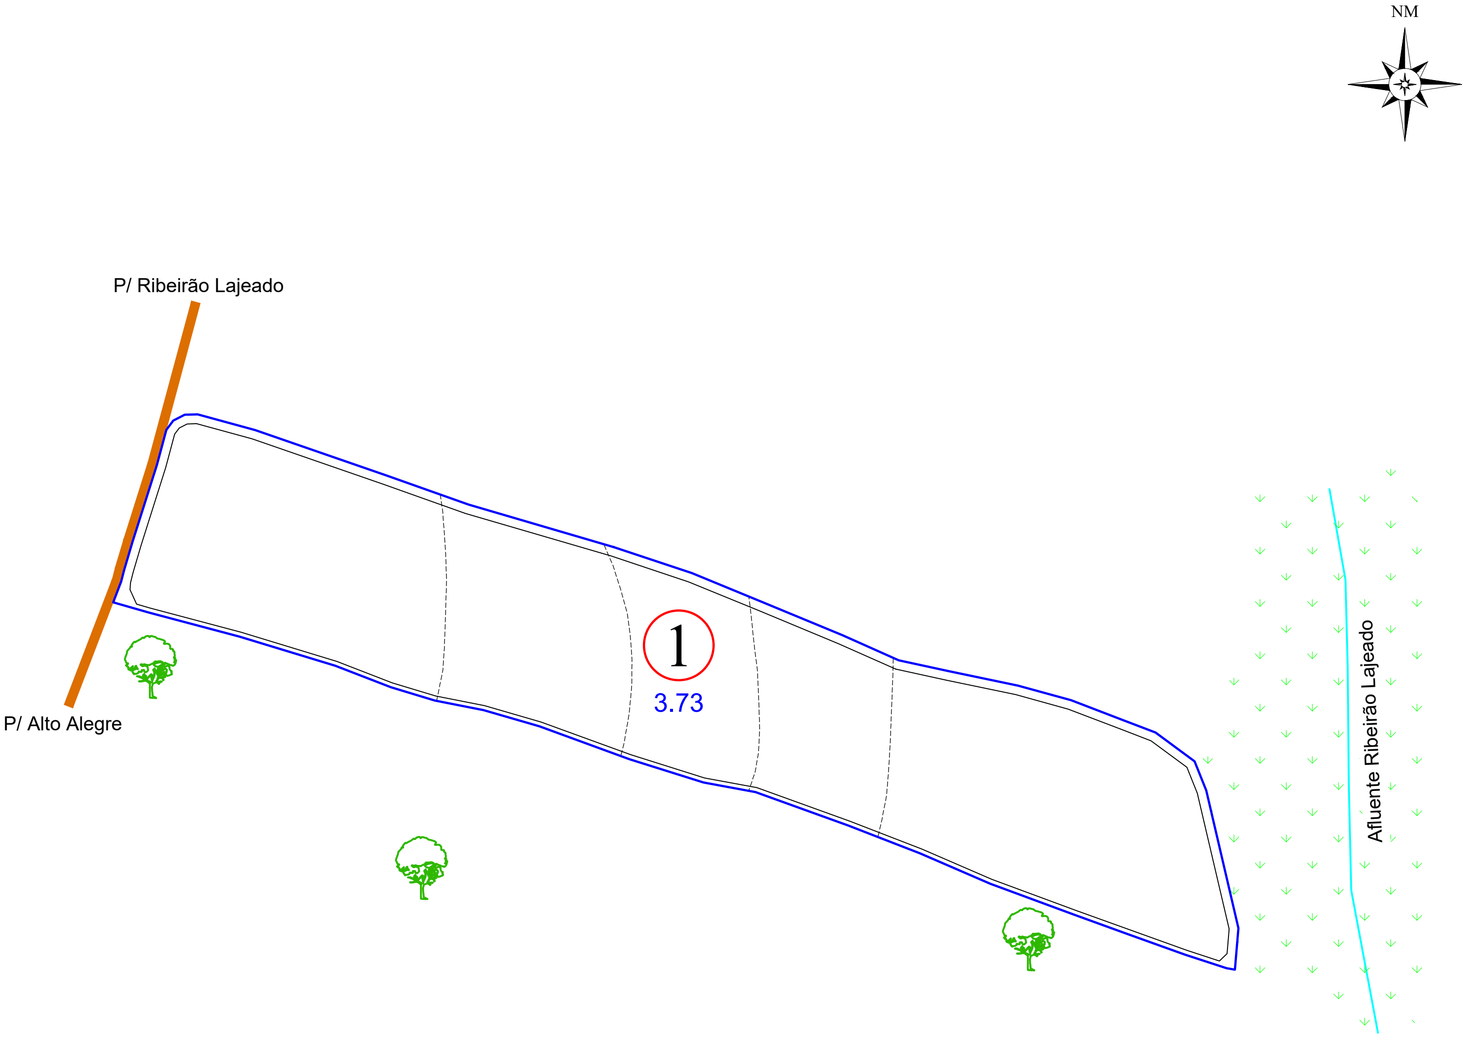

ESCALA: 1: 4.000

## CROQUI DE ACESSO

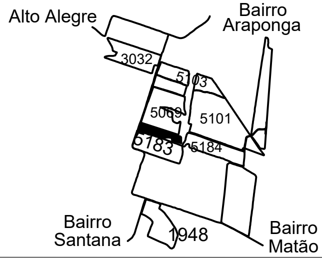

# CHÁCARA SANTO ANTÔNIO

| | |
|---|---|
| PROPRIETÁRIO: | ANTONIO IRVANDRO DE ANDRADE |
| COMPRADOR: | CLEALCO S/A |
| MUNICÍPIO: | PENÁPOLIS |

DISTÂNCIAS (km):

| | | | | |
|---|---|---|---|---|
| UNID. I - | Asfalto: | 51.60 | Terra.: | 6.20 |
| UNID.I I - | Asfalto: | 46.00 | Terra.: | 4.00 |
| UNID. III - | Asfalto: | 11.00 | Terra.: | 4.00 |

| COORDENADAS: | | | | |
|---|---|---|---|---|
| | E(X): | 593379.63 | N(Y): | 7613844.39 |
| | LAT: | -21°34'33.2095" | LONG: | -50°5'52.8937" |

CLEALCO - AÇÚCAR E ALCOOL S/A - DEPARTAMENTO DE TOPOGRAFIA

UNIDADE:
I

PARTE:
A/A

FUNDO AGRÍCOLA:
306910

M:\01-Mapa de safra\Mapas Atualizados\Terceiro\306910 - Chácara Santo Antonio (Antonio Irvandro de Andrade)\306910 - Chácara Santo Antonio (Antonio Irvandro de Andrade).dwg

Bruno Gamboa 17/07/24