ZONA	Nº TAL.	DATA PL.	ÁREA (ha)	VAR.
999	1	05/2021	20.97	CTC 04
	2		16.54	
TOTAL PLANTIO			37.51	--------


ÁREAS	(ha)	(%)
PLANTIO	37.51	93.43
CARREADORES	2.20	5.47
OUTROS	0.37	0.92
SUB TOTAL AGRICULTÁVEL	40.08	99.83
AP.P.	0.00	0.00
MATA	0.07	0.17
OUTROS	0.00	0.00
SUB TOTAL NÃO AGRICULT.	0.07	0.17
ÁREA TOTAL	40.15	100.00


C. NÍVEL:	6309.24 m/l	1.45 ha	3.61 %

LEGENDA

- FAZENDA
- TALHÃO
- CURVA DE NÍVEL
- CARREADOR
- CONFRONTANTE
- REDE ELÉTRICA
- TRAJETO VAZIO
- TRAJETO CARREGADO

PLANTIO MANUAL - ESPAÇAMENTO: 1.50 X 1.50

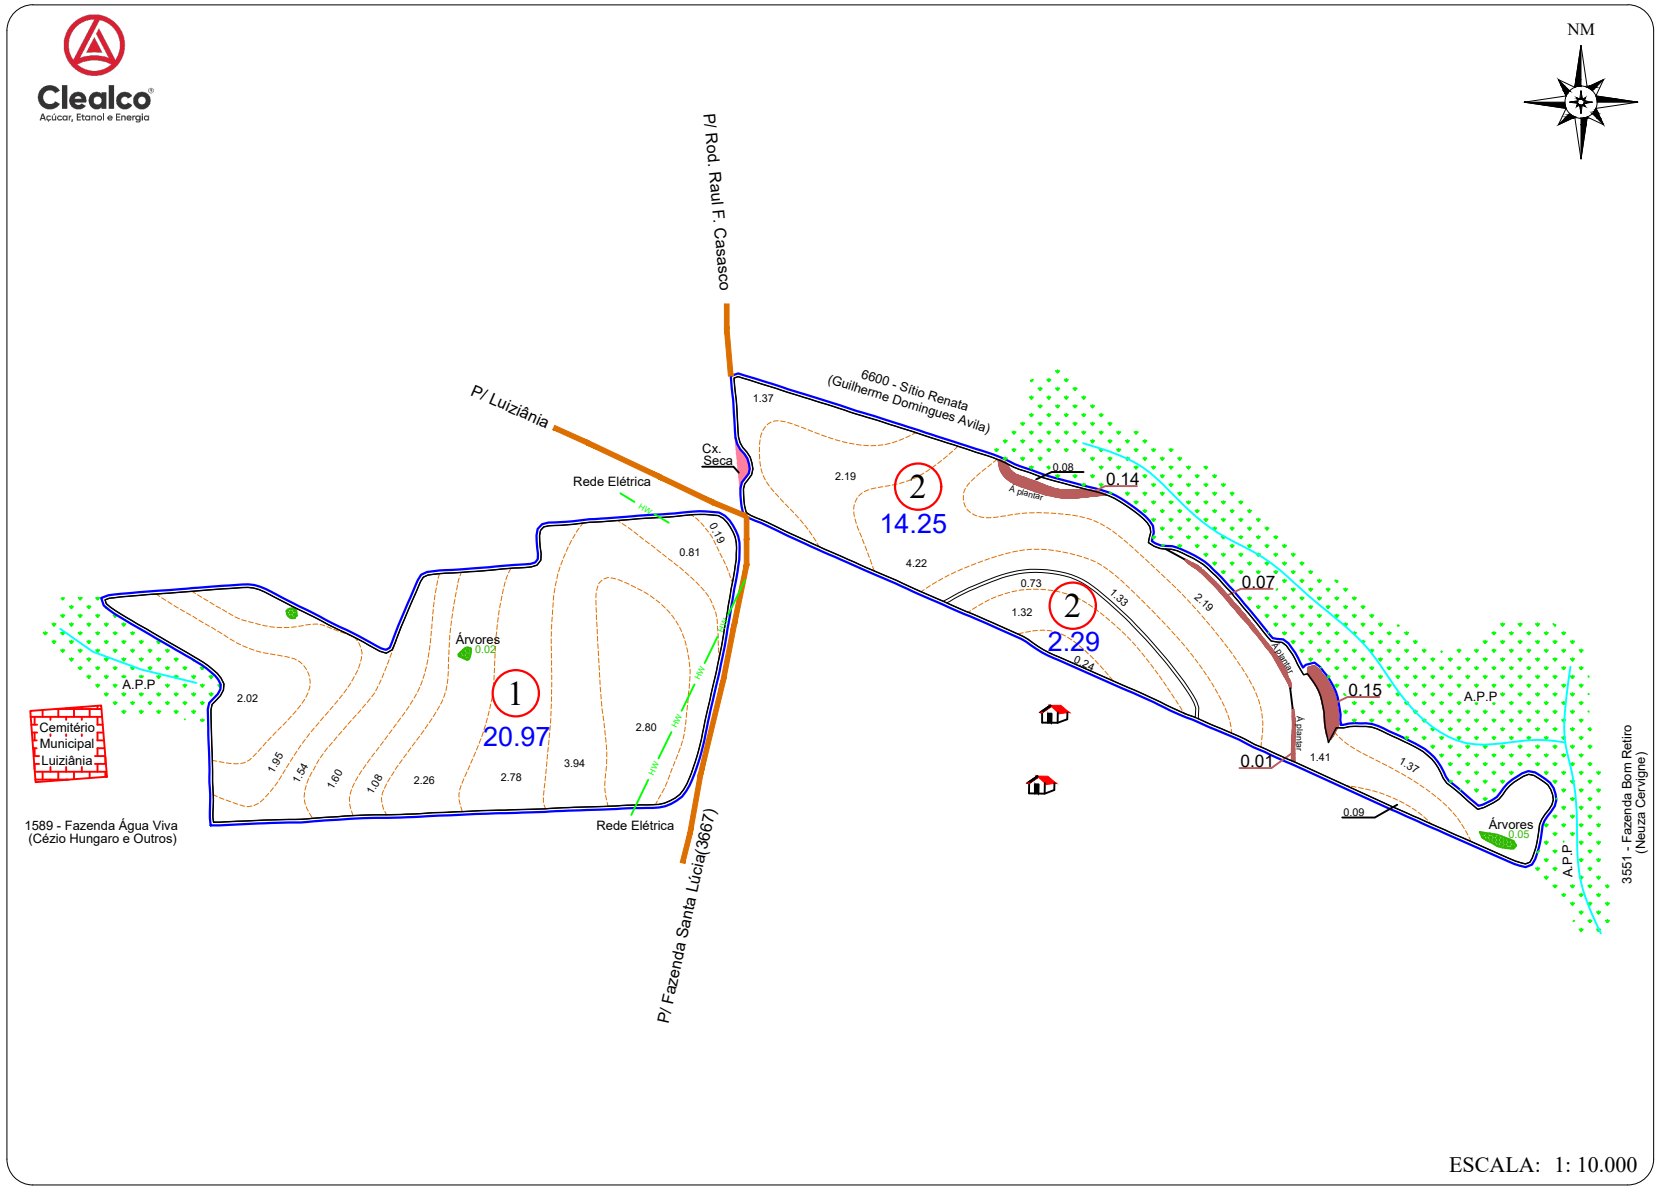

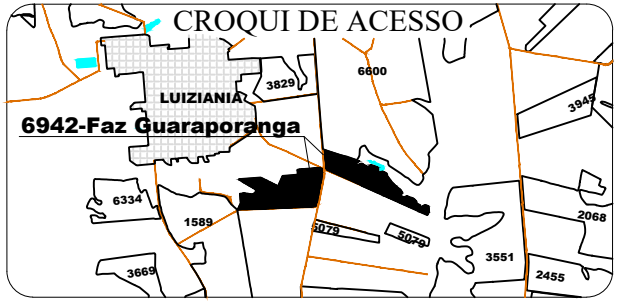

FAZENDA GUARAPORANGA

PROPRIETÁRIO: CLÉZIO HUNGARO
COMPRADOR: CLEALCO S/A
MUNICÍPIO: LUIZIÂNIA

DISTÂNCIAS (km):
UNID. I - Asfalto: 35.00 Terra.: 5.00
UNID.I I - Asfalto: 26.00 Terra.: 3.30
UNID. III -Asfalto: 34.00 Terra.: 3.50

COORDENADAS: E(X): 570.937,70 N(Y): 7.602.067,79
LAT: 21°40'59.9445" LONG: 50°18'51.4152"

CLEALCO - AÇÚCAR E ALCOOL S/A - DEPARTAMENTO DE TOPOGRAFIA

UNIDADE: I
PARTE: A/A
FUNDO AGRÍCOLA: 306942

M:\01-Mapa de safra\Mapas Atualizados\Terceiro\306942 - Fazenda Guaporanga (Clézio Hungaro)\306942 - Fazenda Guaporanga (Clézio Hungaro).dwg

Fernanda Bezerra 20/06/23